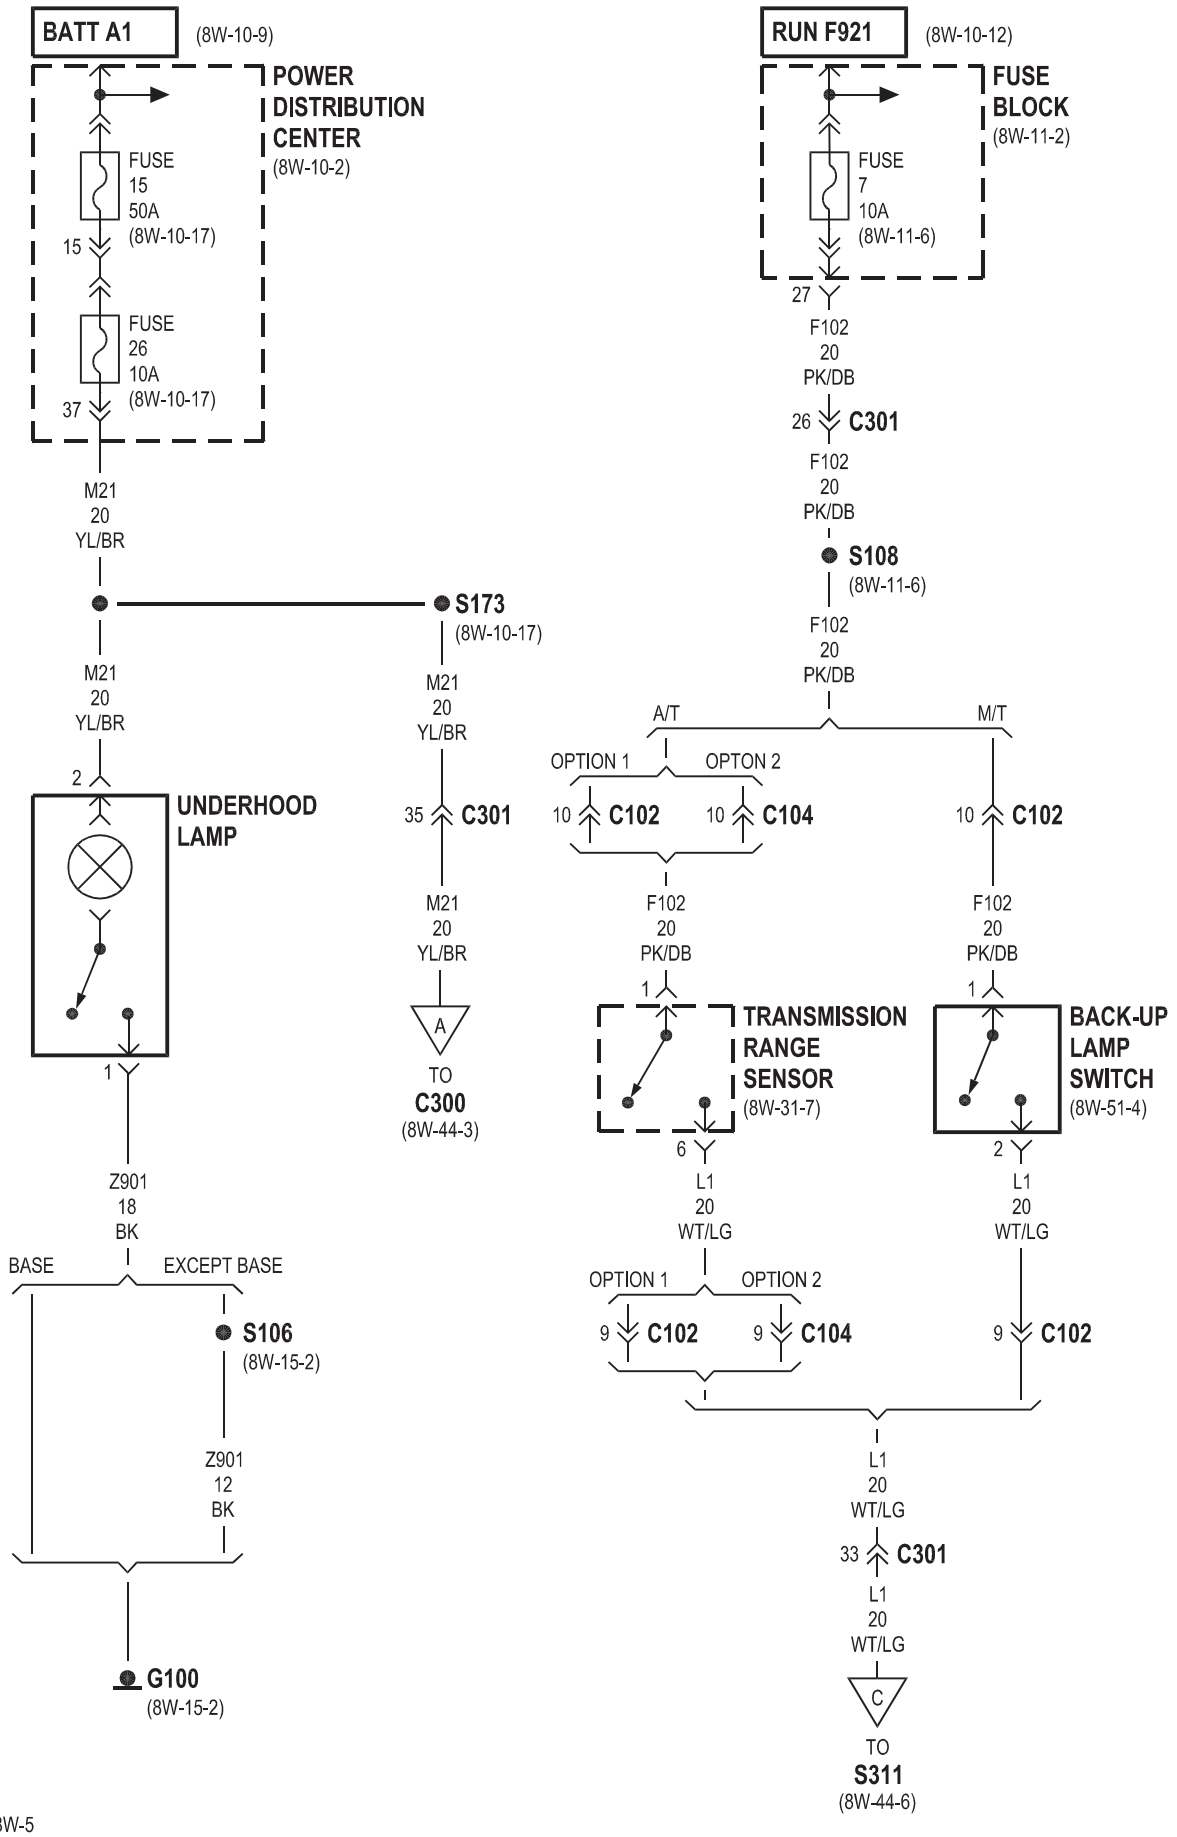

BATT A1
(8W-10-9)
POWER DISTRIBUTION CENTER
(8W-10-2)
FUSE 15 50A (8W-10-17)
FUSE 26 10A (8W-10-17)
15
37
M21 20 YL/BR
S173
(8W-10-17)
2
UNDERHOOD LAMP
1
Z901 18 BK
BASE
EXCEPT BASE
S106
(8W-15-2)
Z901 12 BK
G100
(8W-15-2)
35 C301
A
TO C300
(8W-44-3)
RUN F921
(8W-10-12)
FUSE BLOCK
(8W-11-2)
FUSE 7 10A (8W-11-6)
27
F102 20 PK/DB
26 C301
S108
(8W-11-6)
A/T
M/T
OPTION 1
OPTON 2
10 C102
10 C104
10 C102
1
TRANSMISSION RANGE SENSOR
(8W-31-7)
BACK-UP LAMP SWITCH
(8W-51-4)
6
2
L1 20 WT/LG
9 C102
9 C104
9 C102
33 C301
C
TO S311
(8W-44-6)