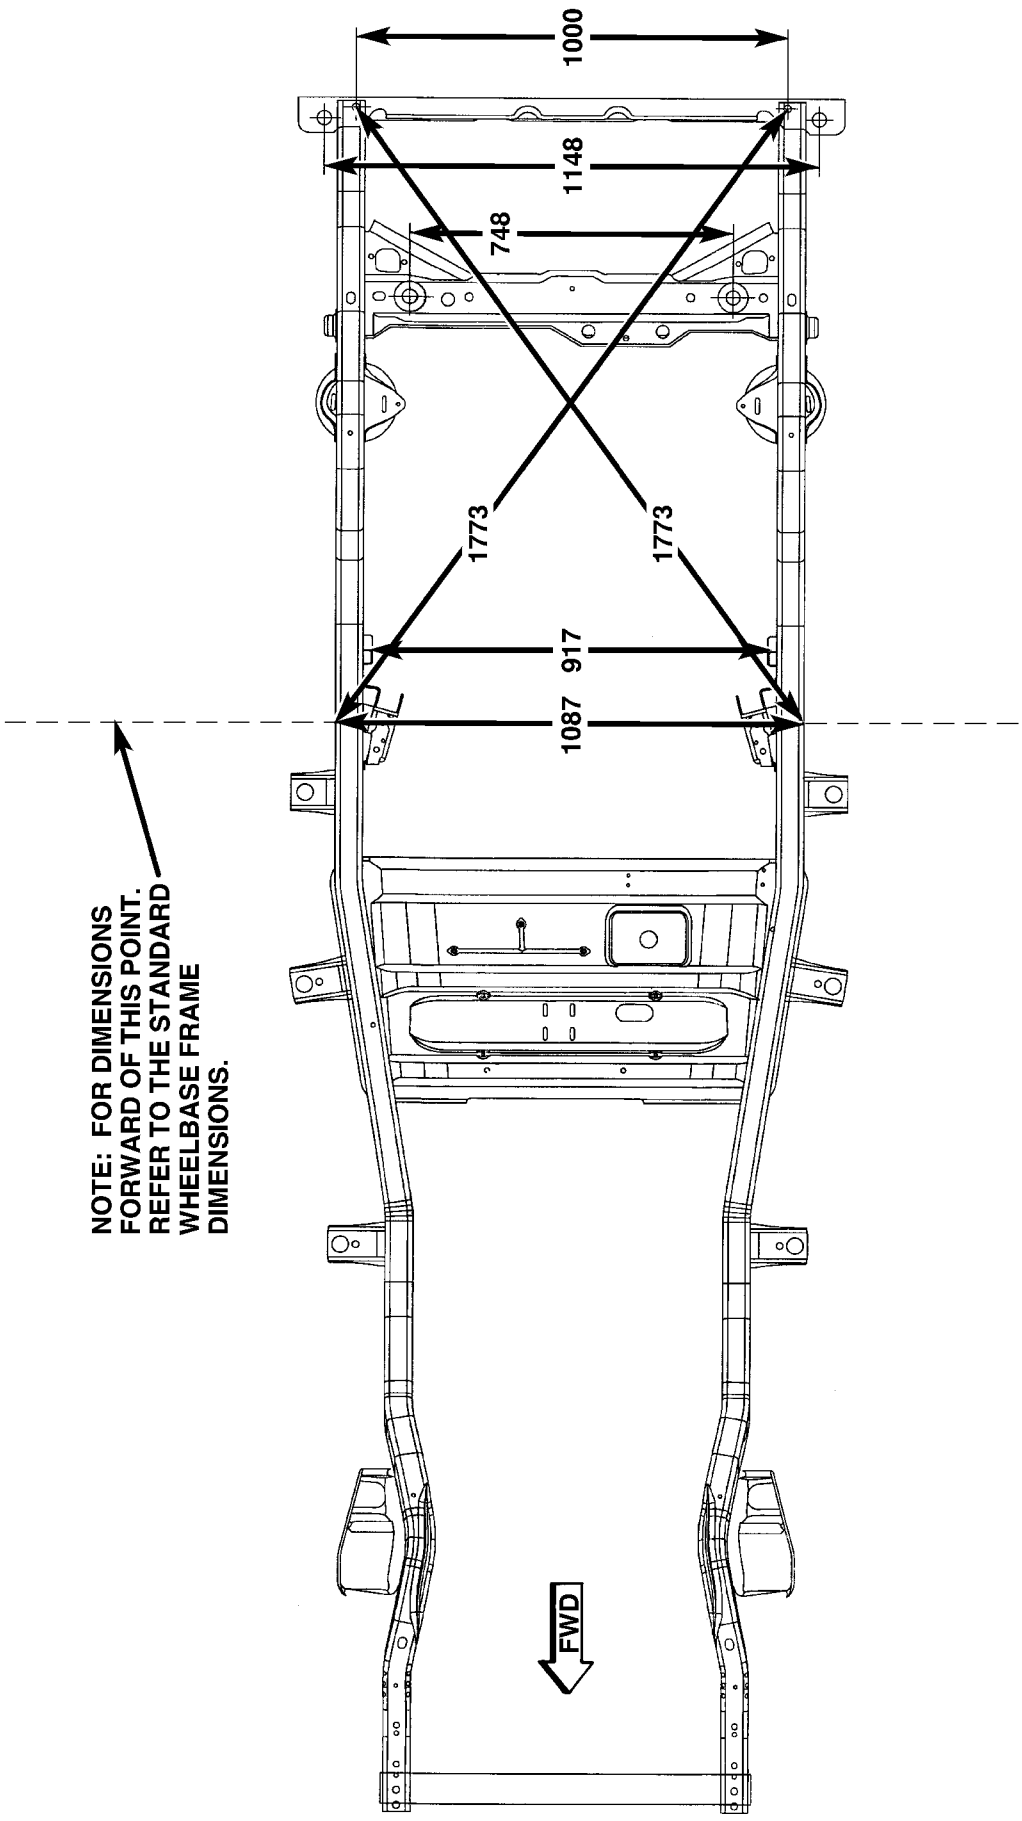

Fig. 9 FRAME TOP VIEW LWB