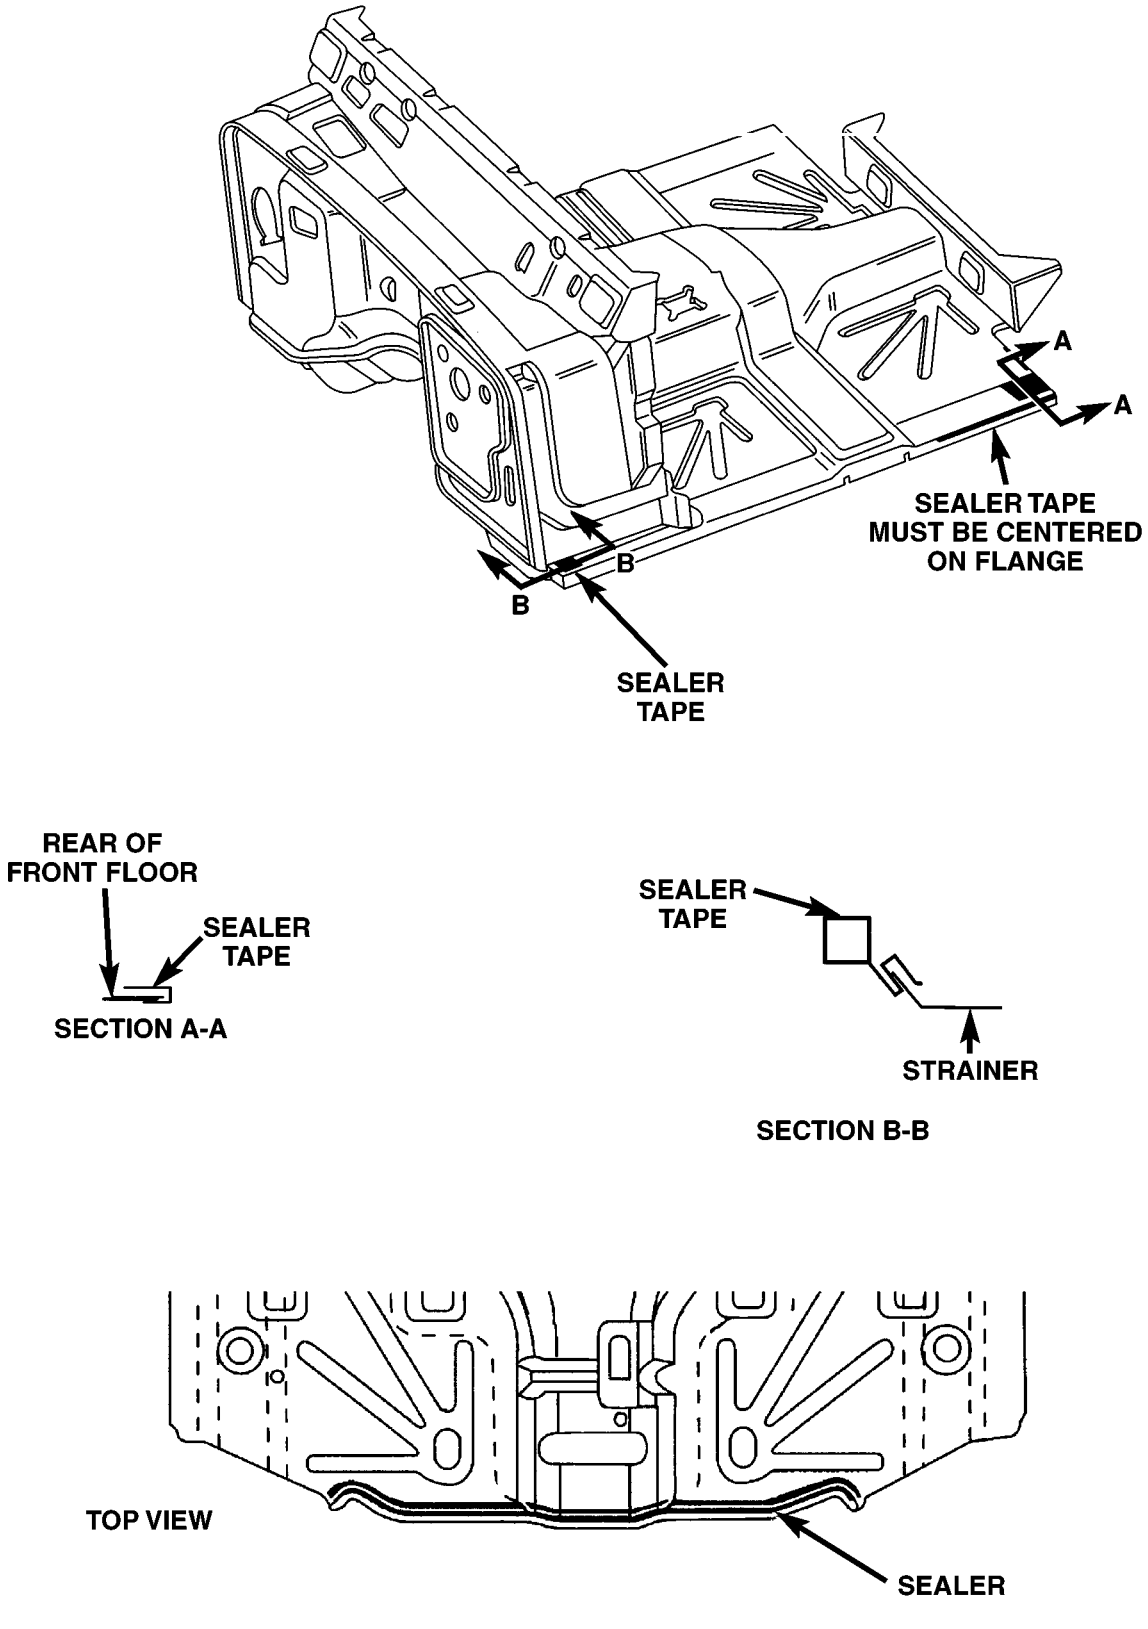

Fig. 23 FRONT FLOOR, STRAINER, REINFORCEMENT AND COWL SIDE LOWER