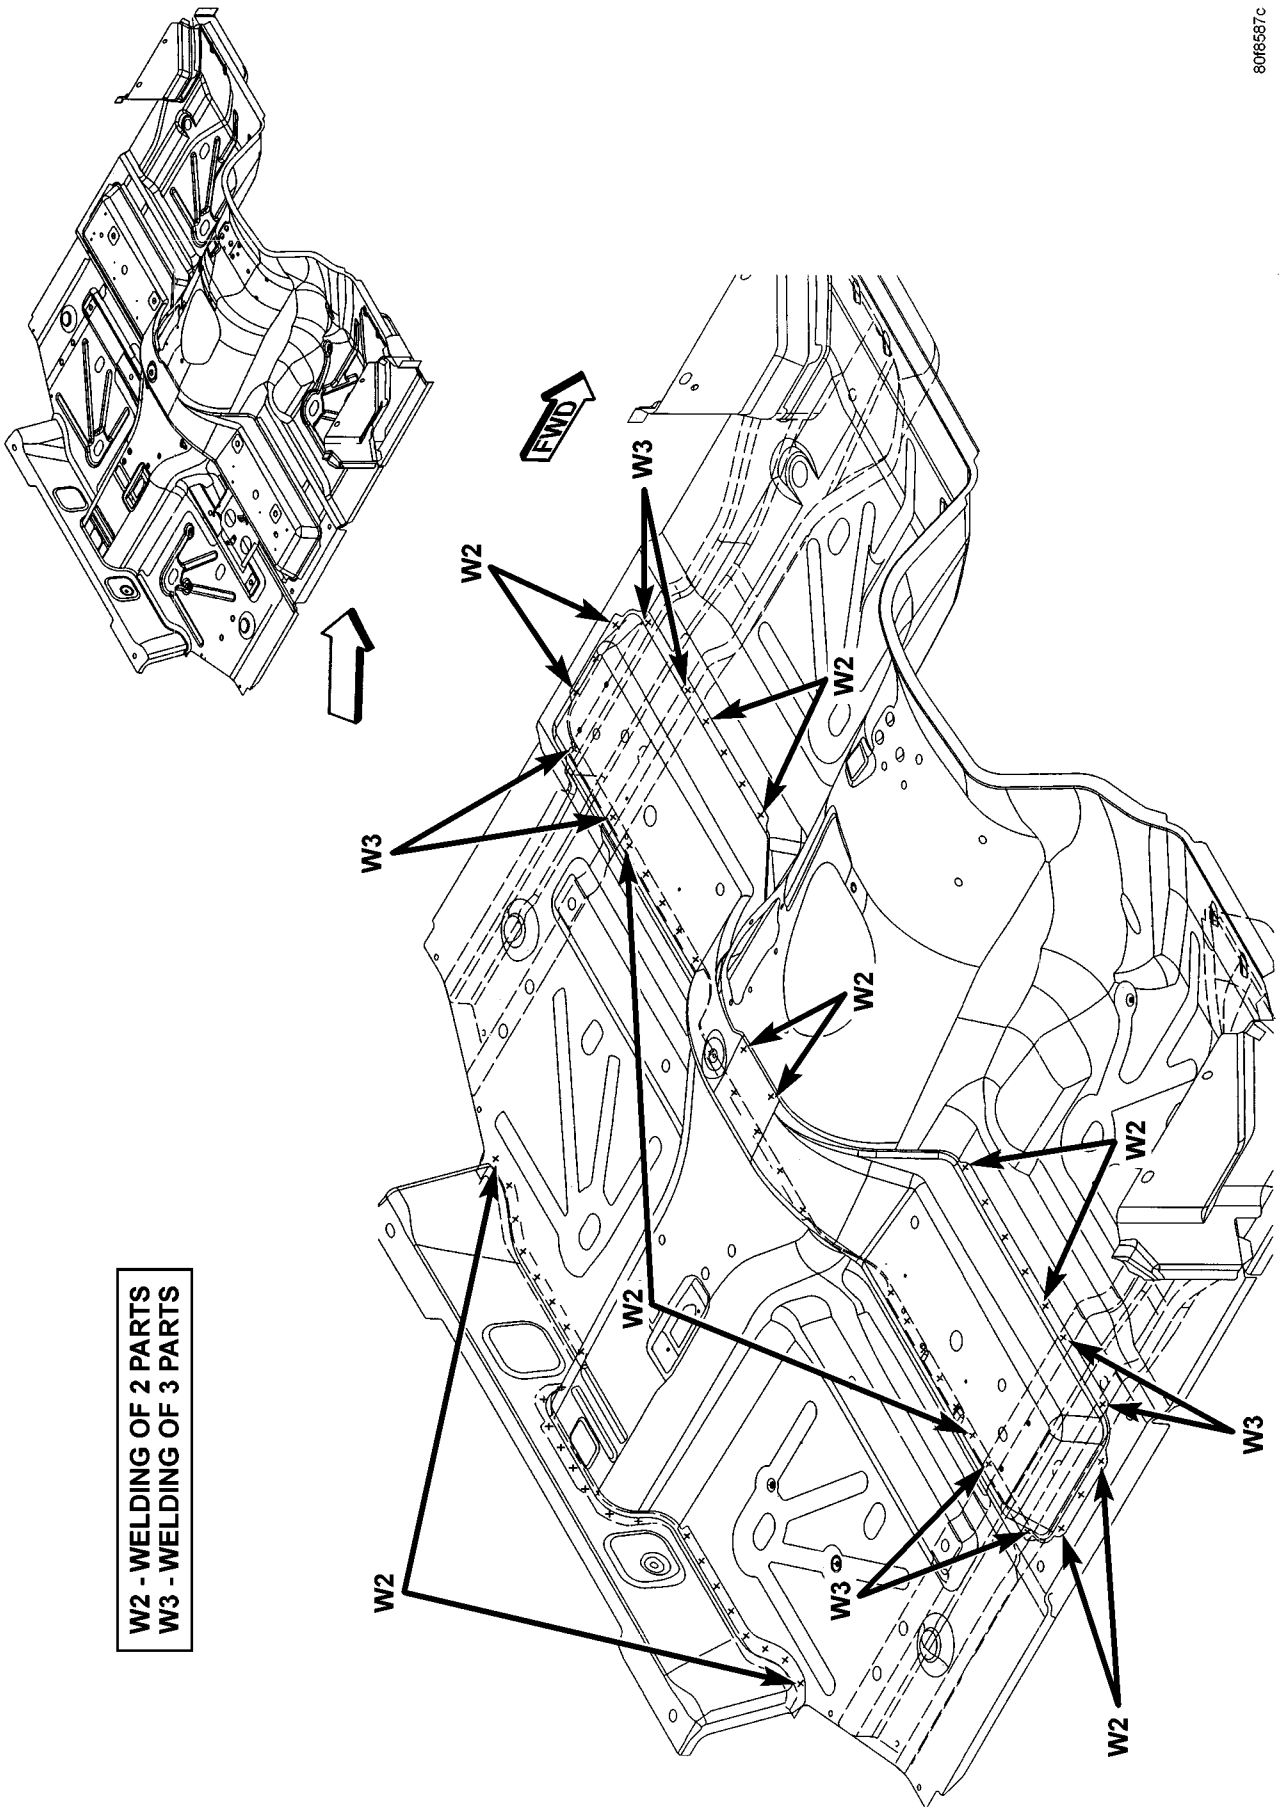


Fig. 41 FRONT FLOOR PAN (2 OF 3)