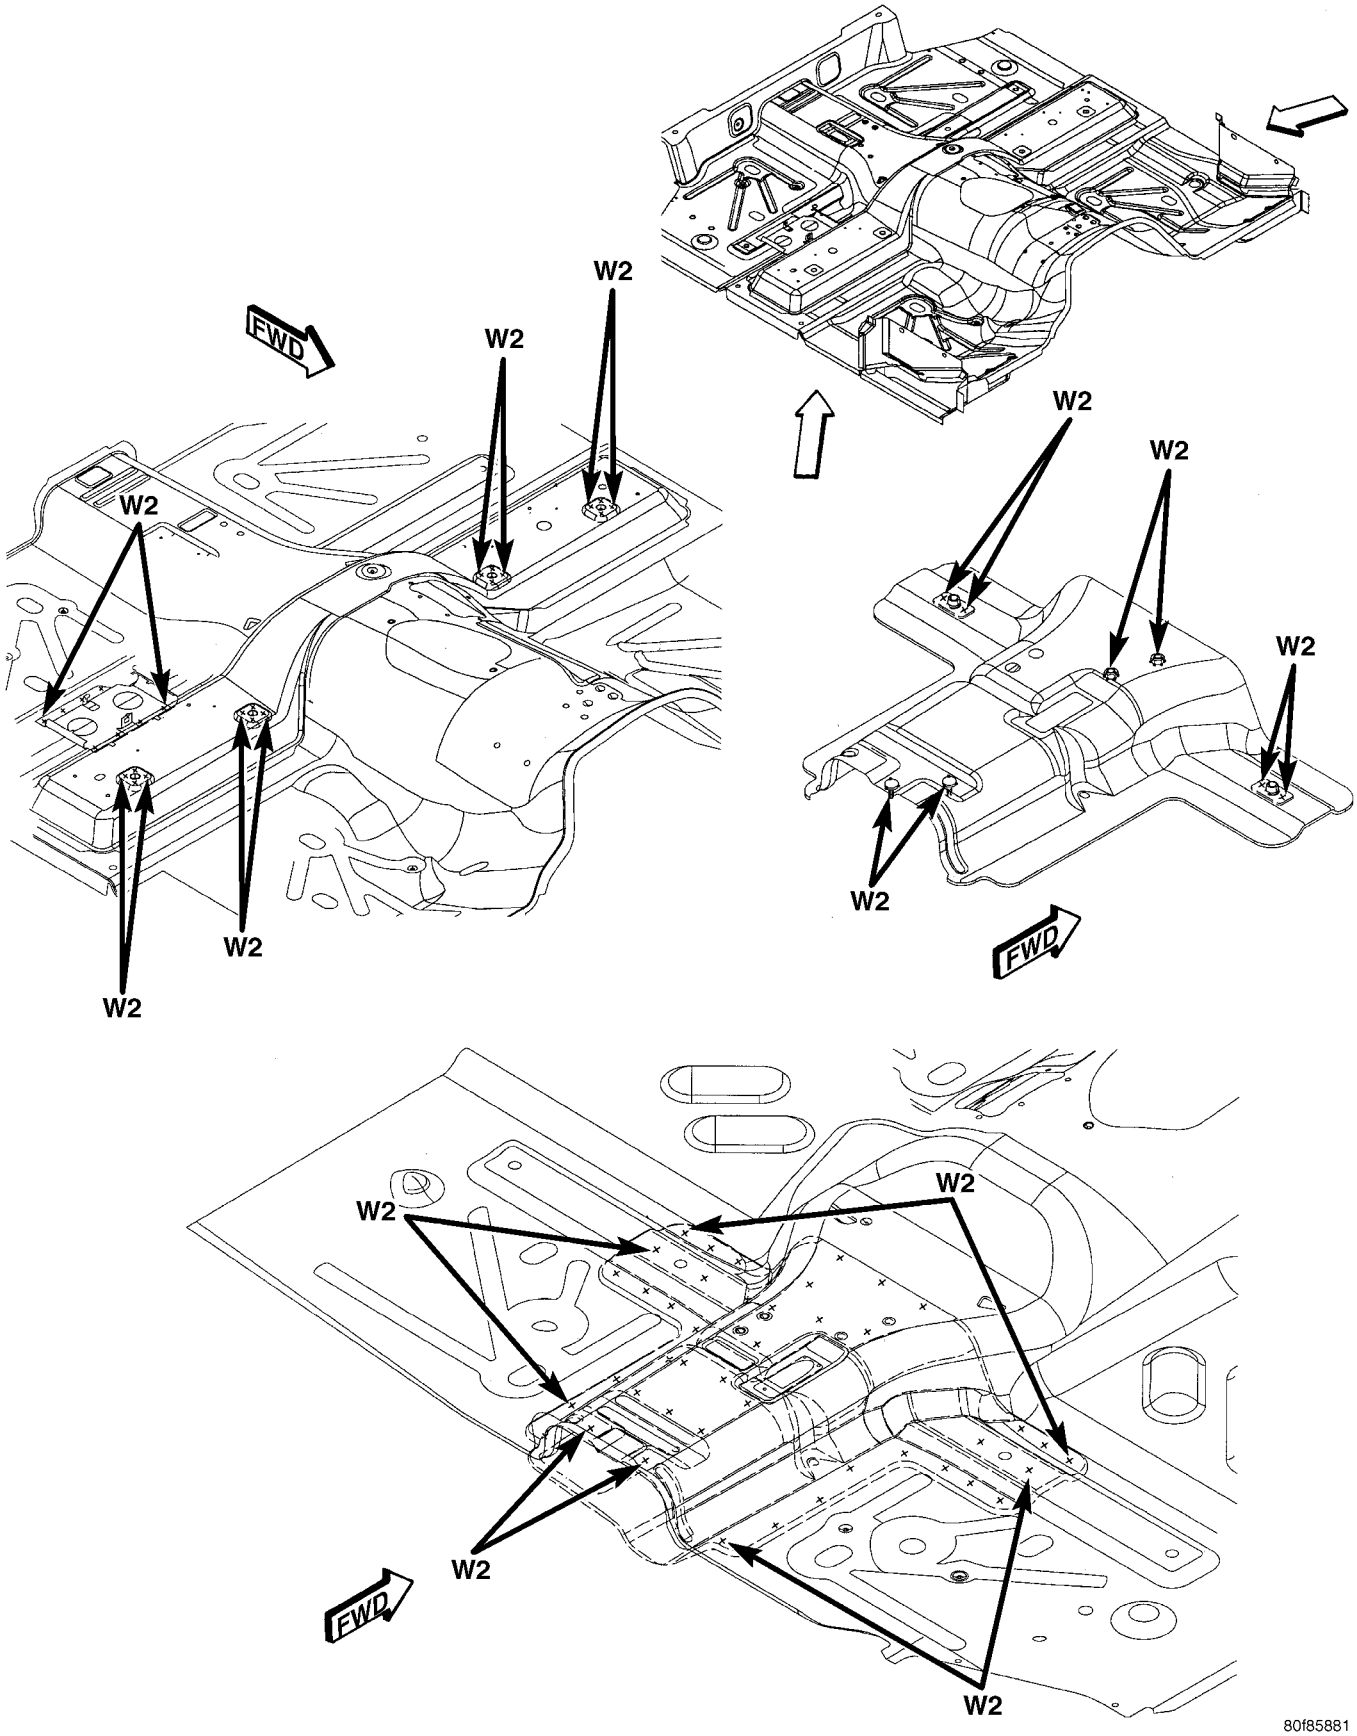


Fig. 42 FRONT FLOOR PAN (3 OF 3)