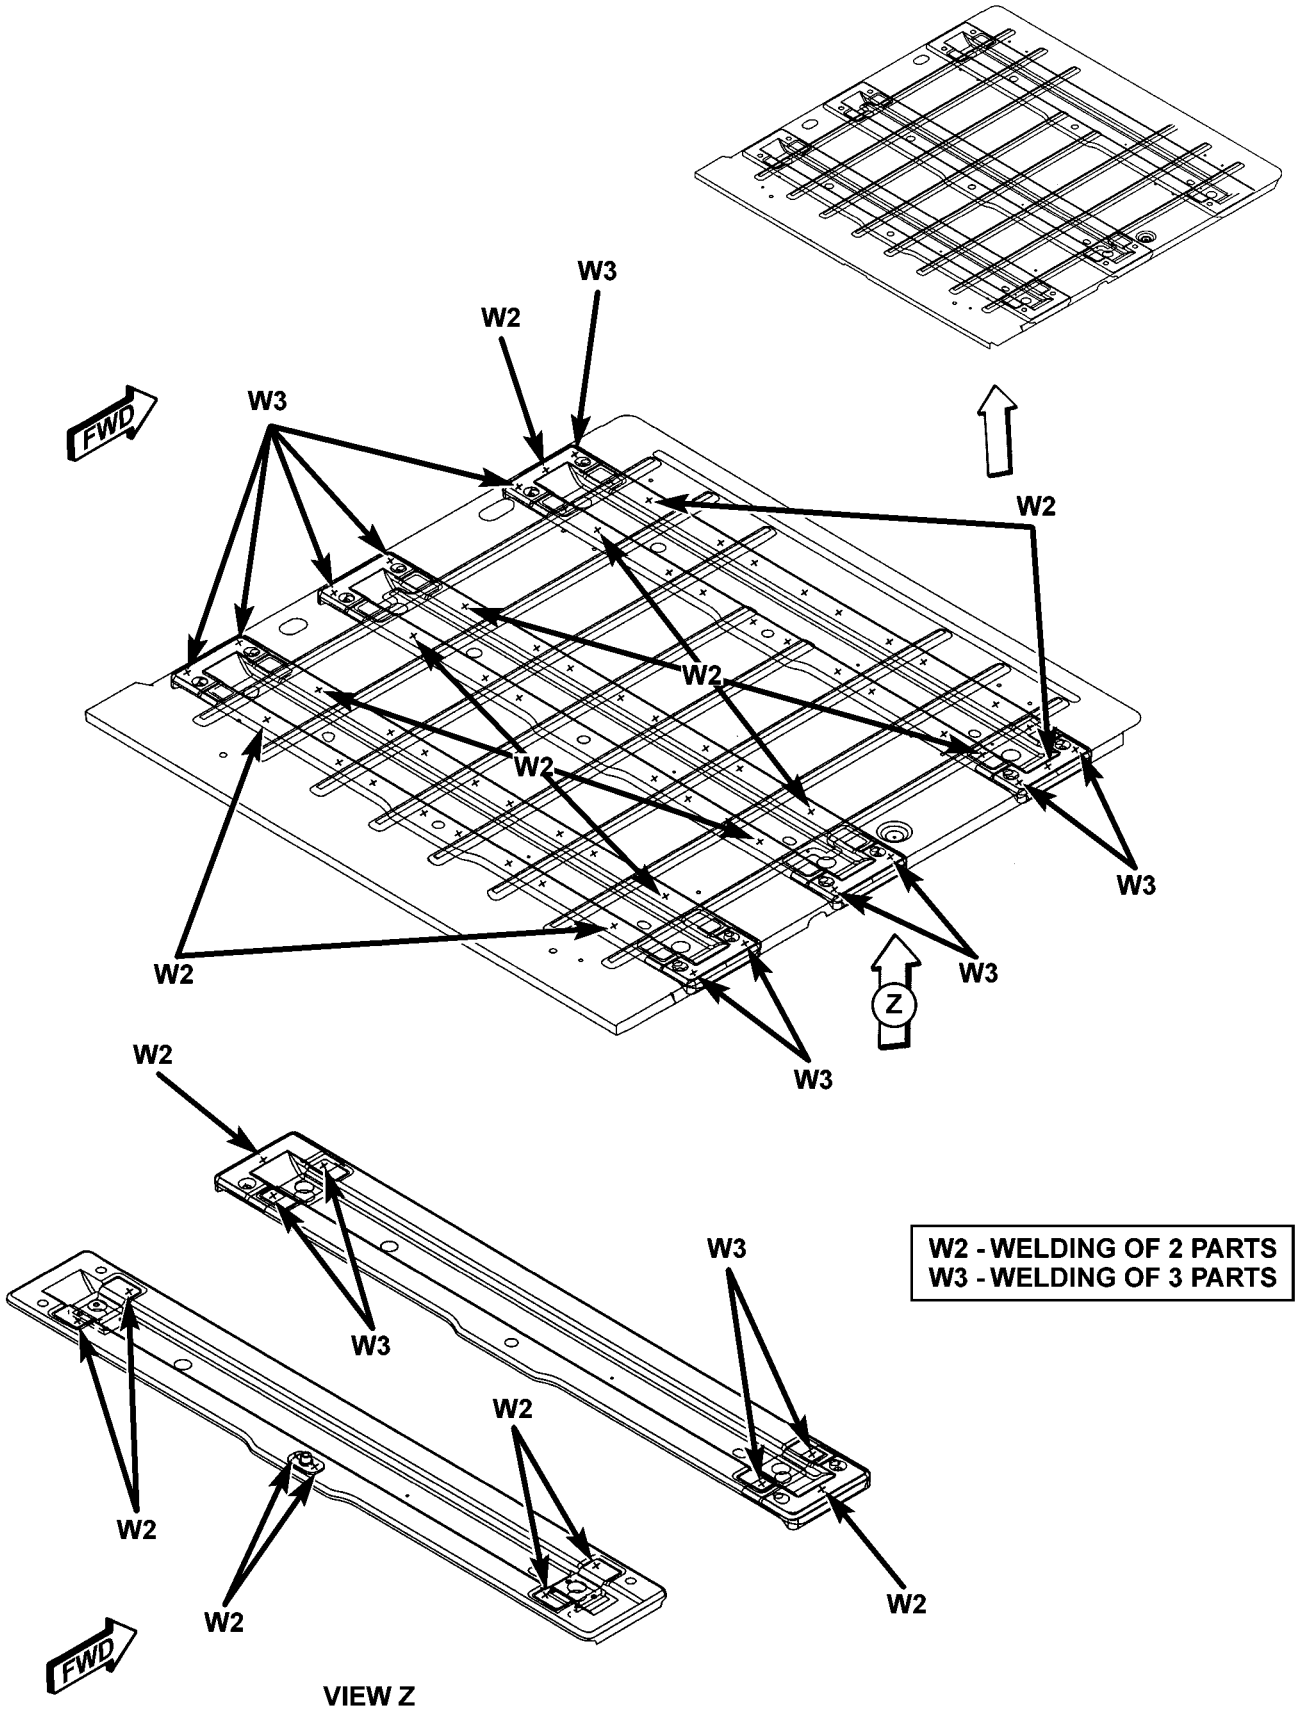


Fig. 43 REAR FLOOR PAN (1 OF 2)