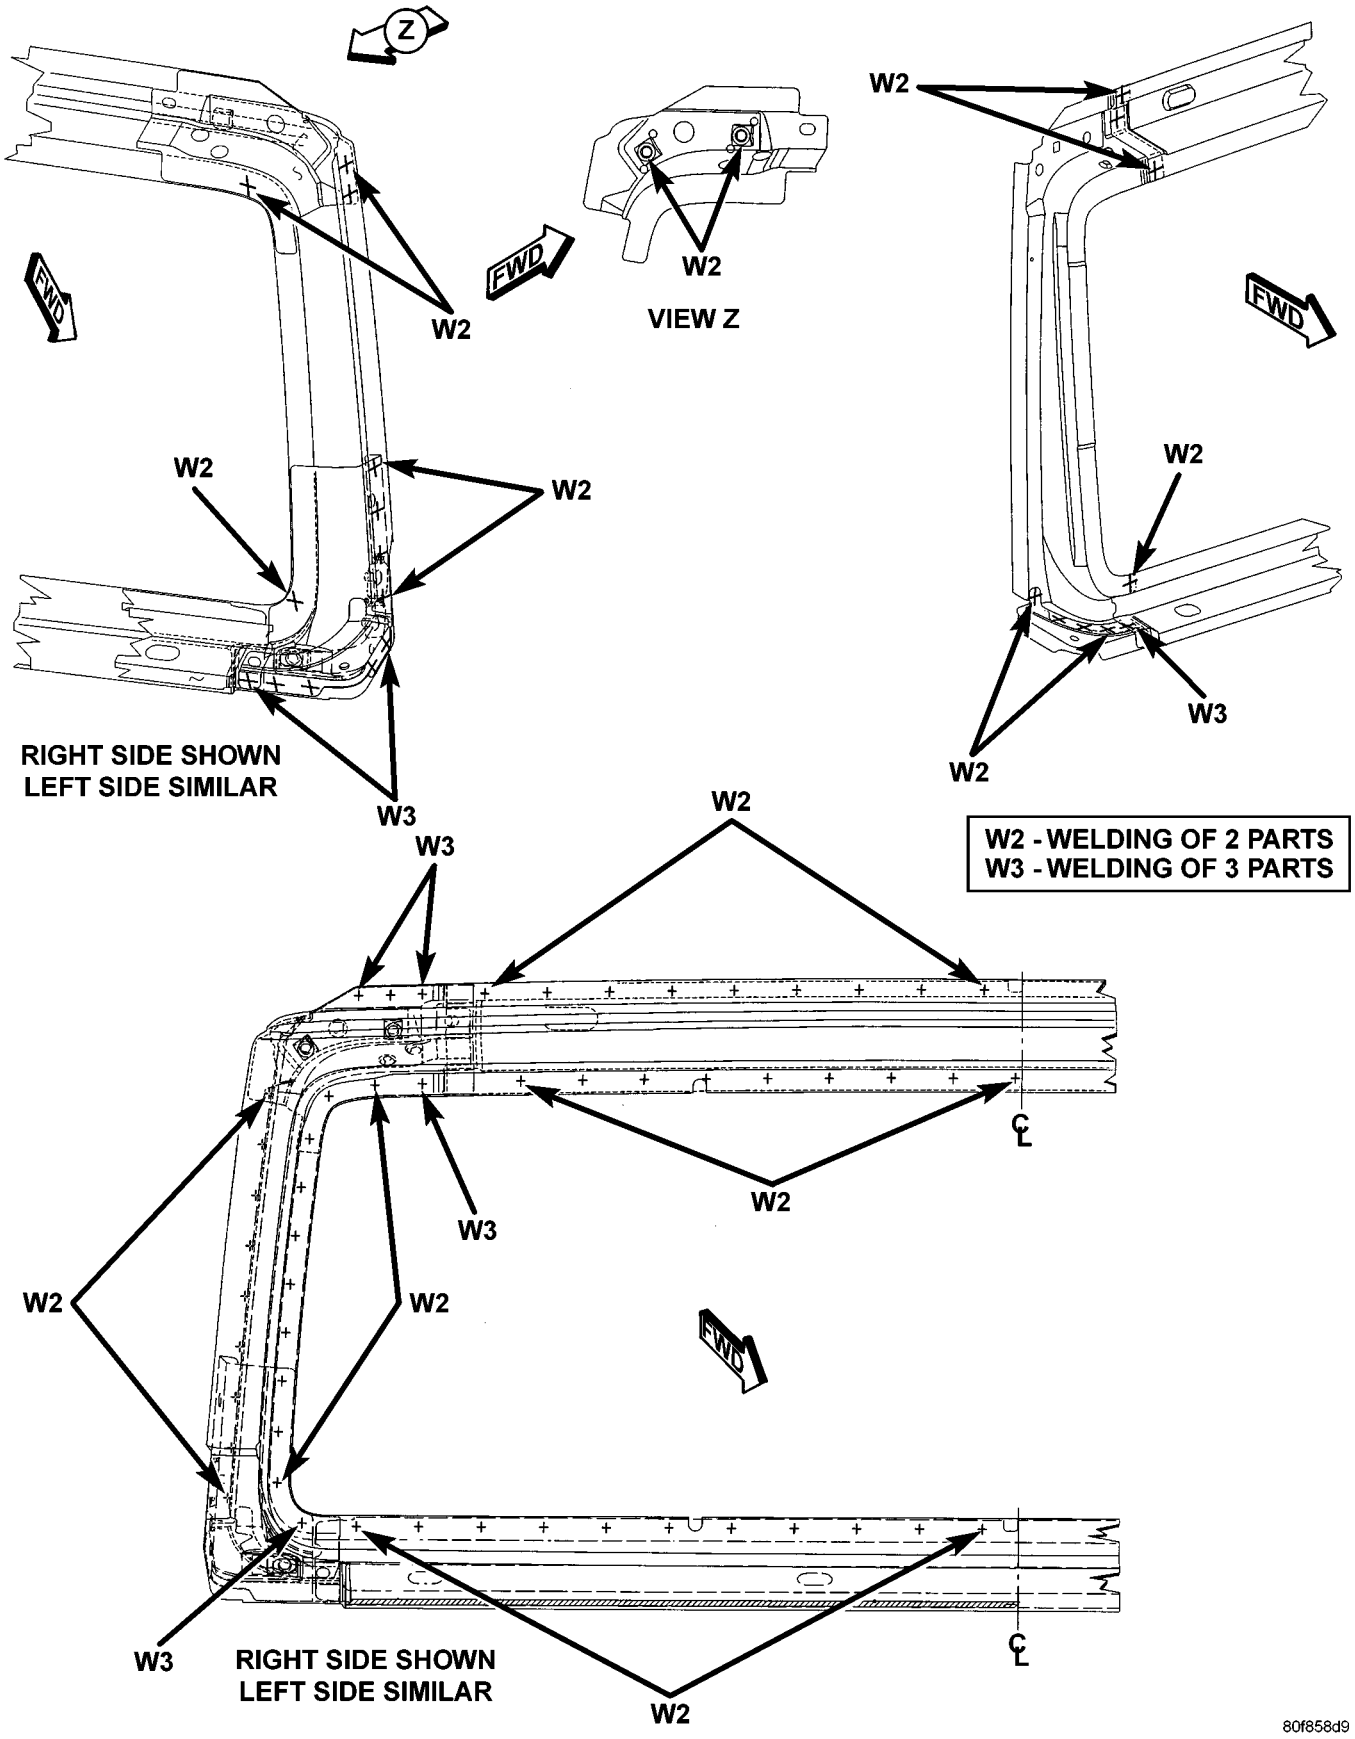

Fig. 50 WINDSHIELD FRAME