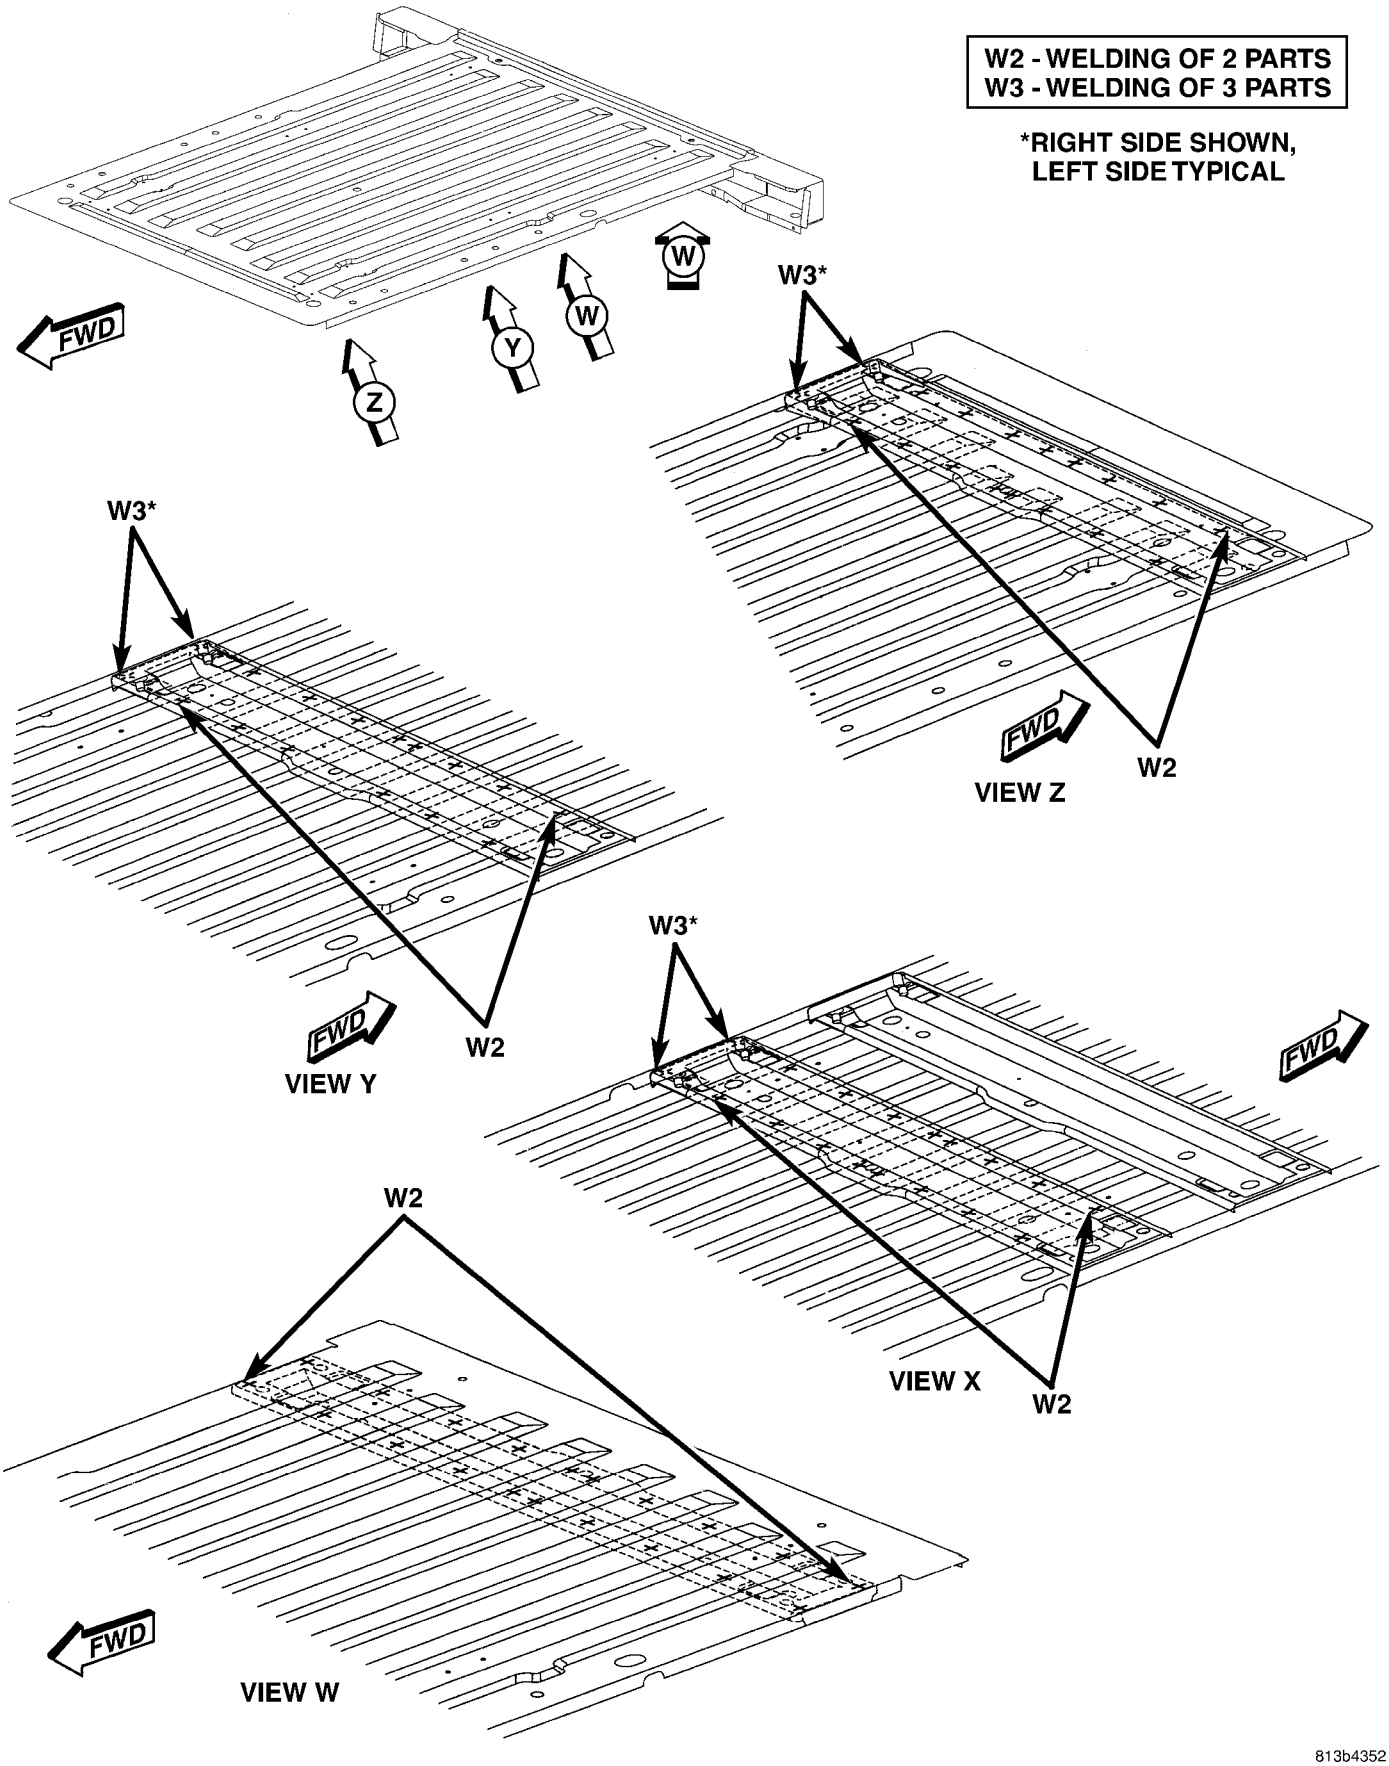


Fig. 79 REAR FLOOR LWB (2 OF 3)