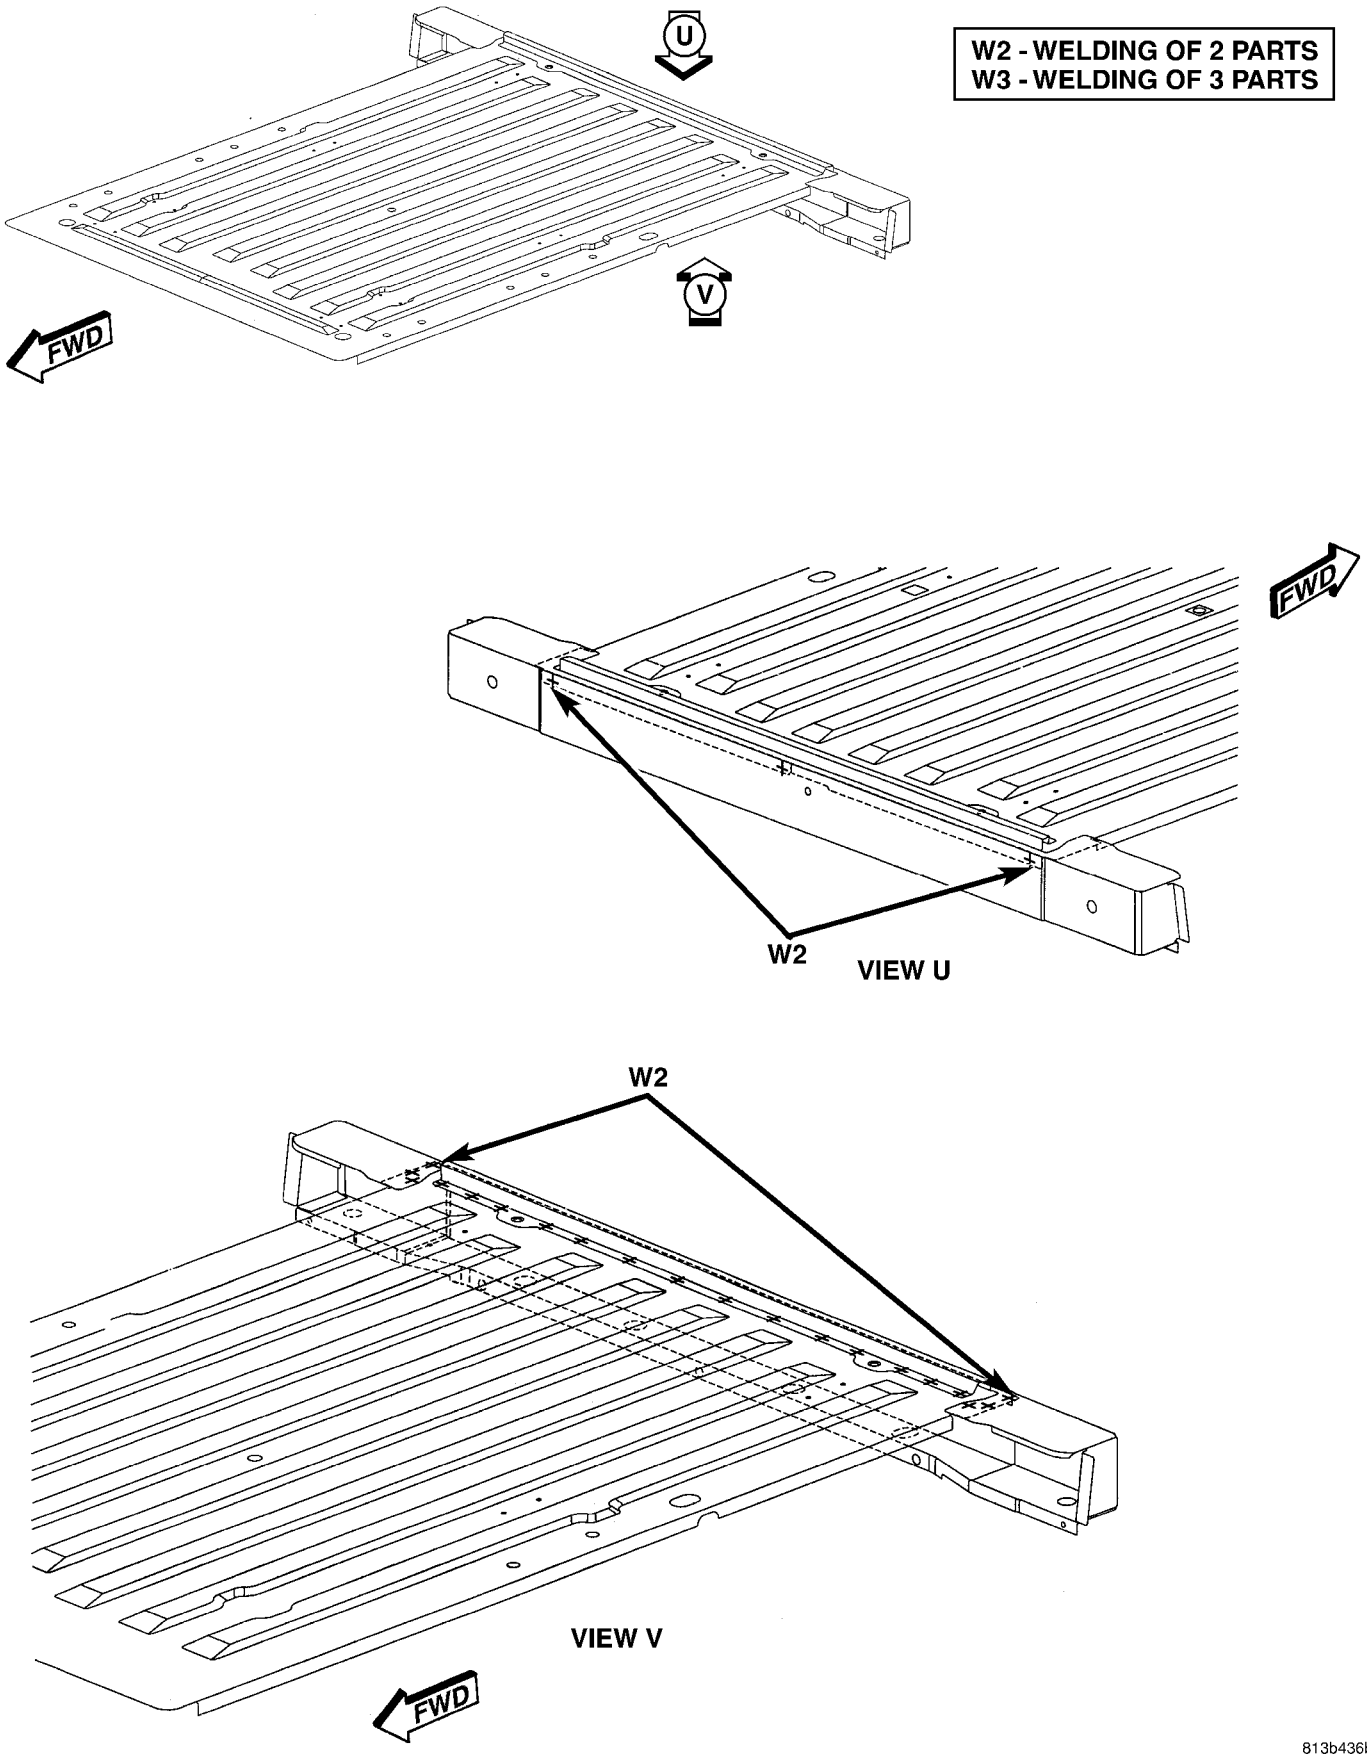


Fig. 80 REAR FLOOR LWB (3 OF 3)