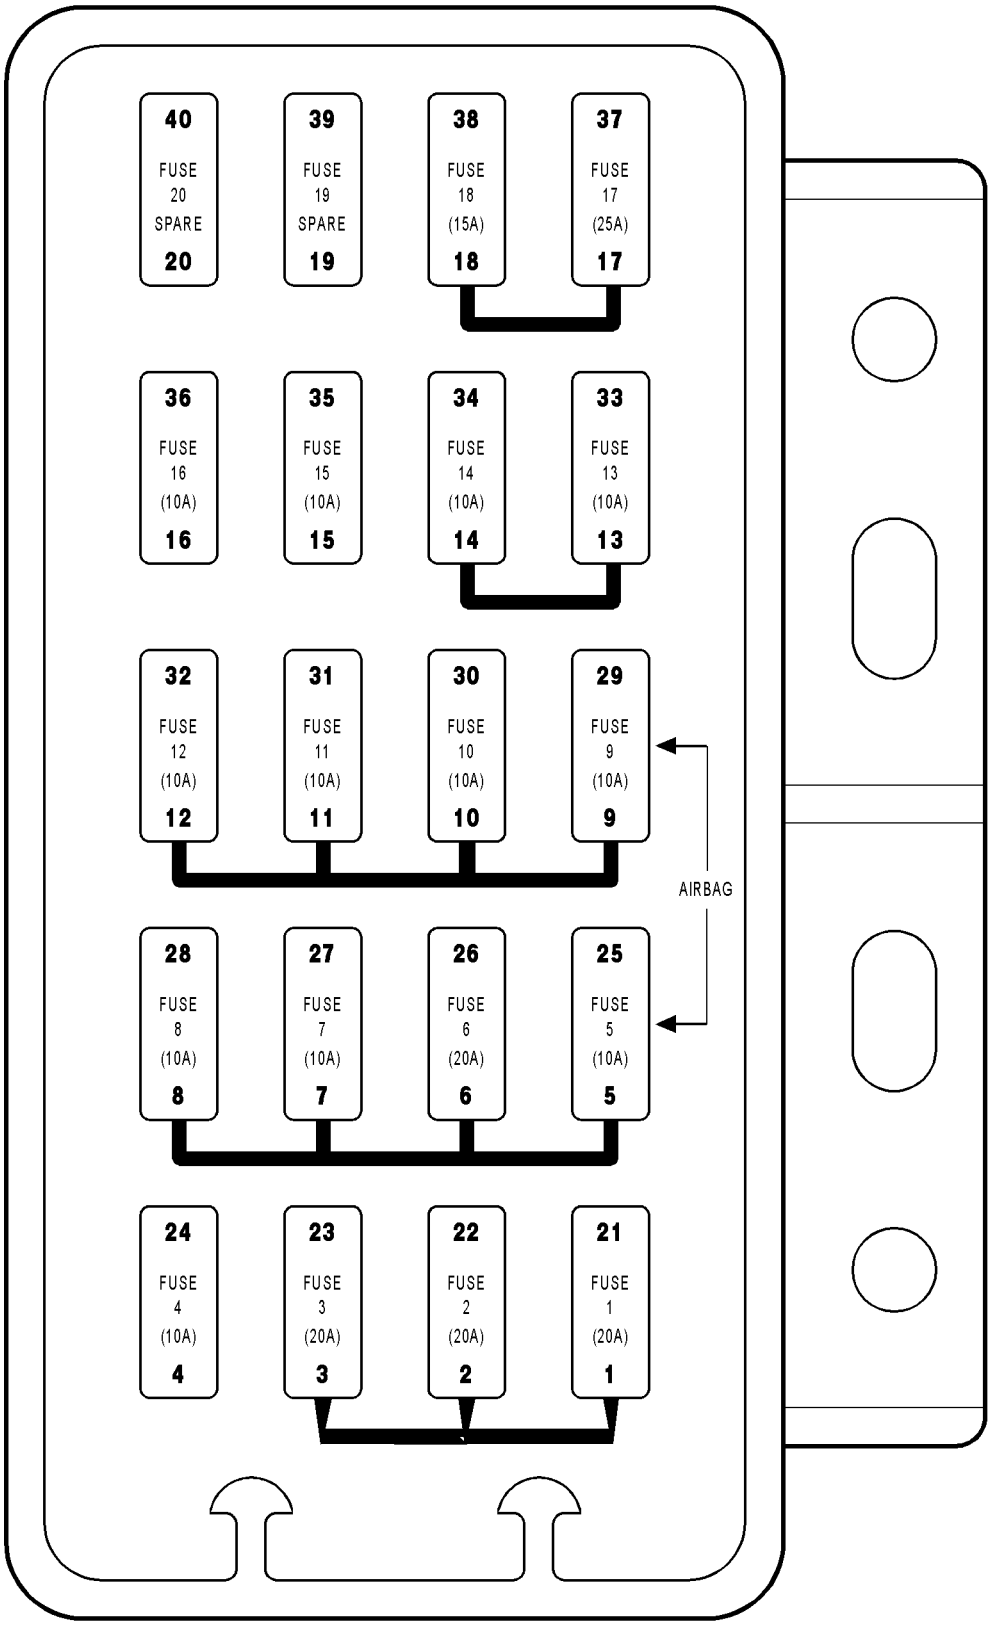FRONT OF FUSE BLOCK