CONNECTOR/GROUND/SPLICE LOCATION (Continued)

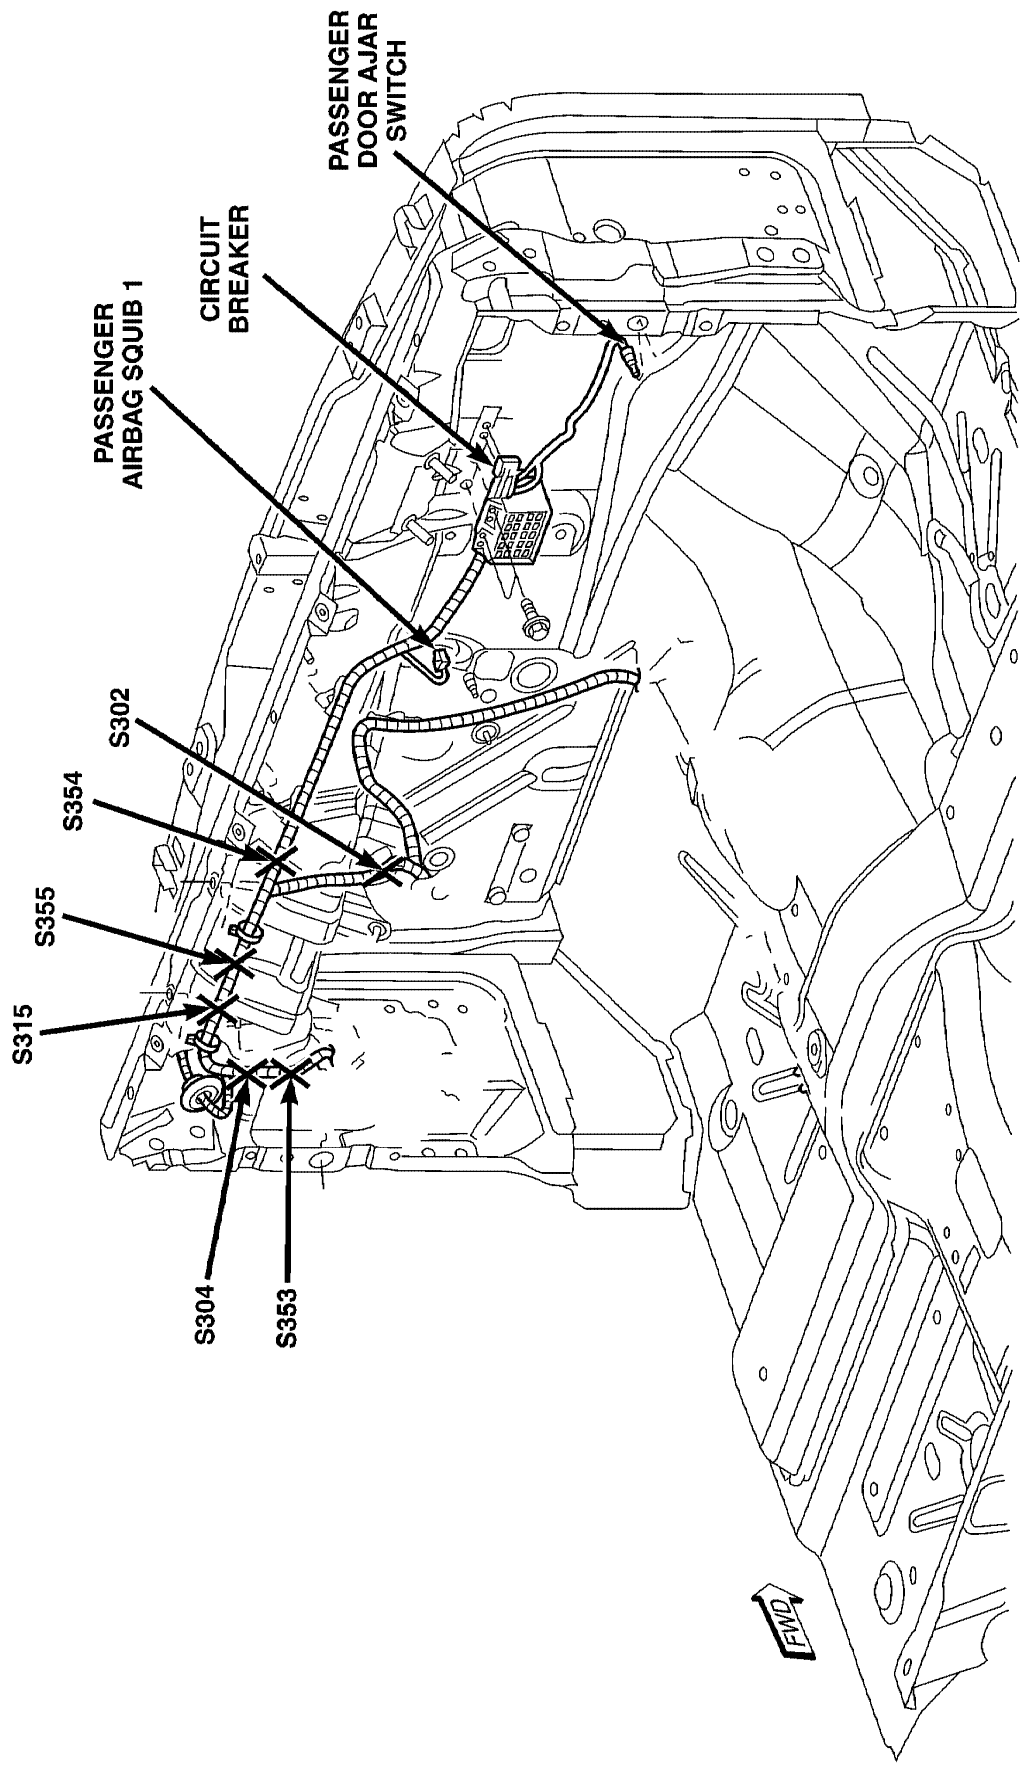


Fig. 19 -DASH PANEL (LHD)