CONNECTOR/GROUND/SPLICE LOCATION (Continued)

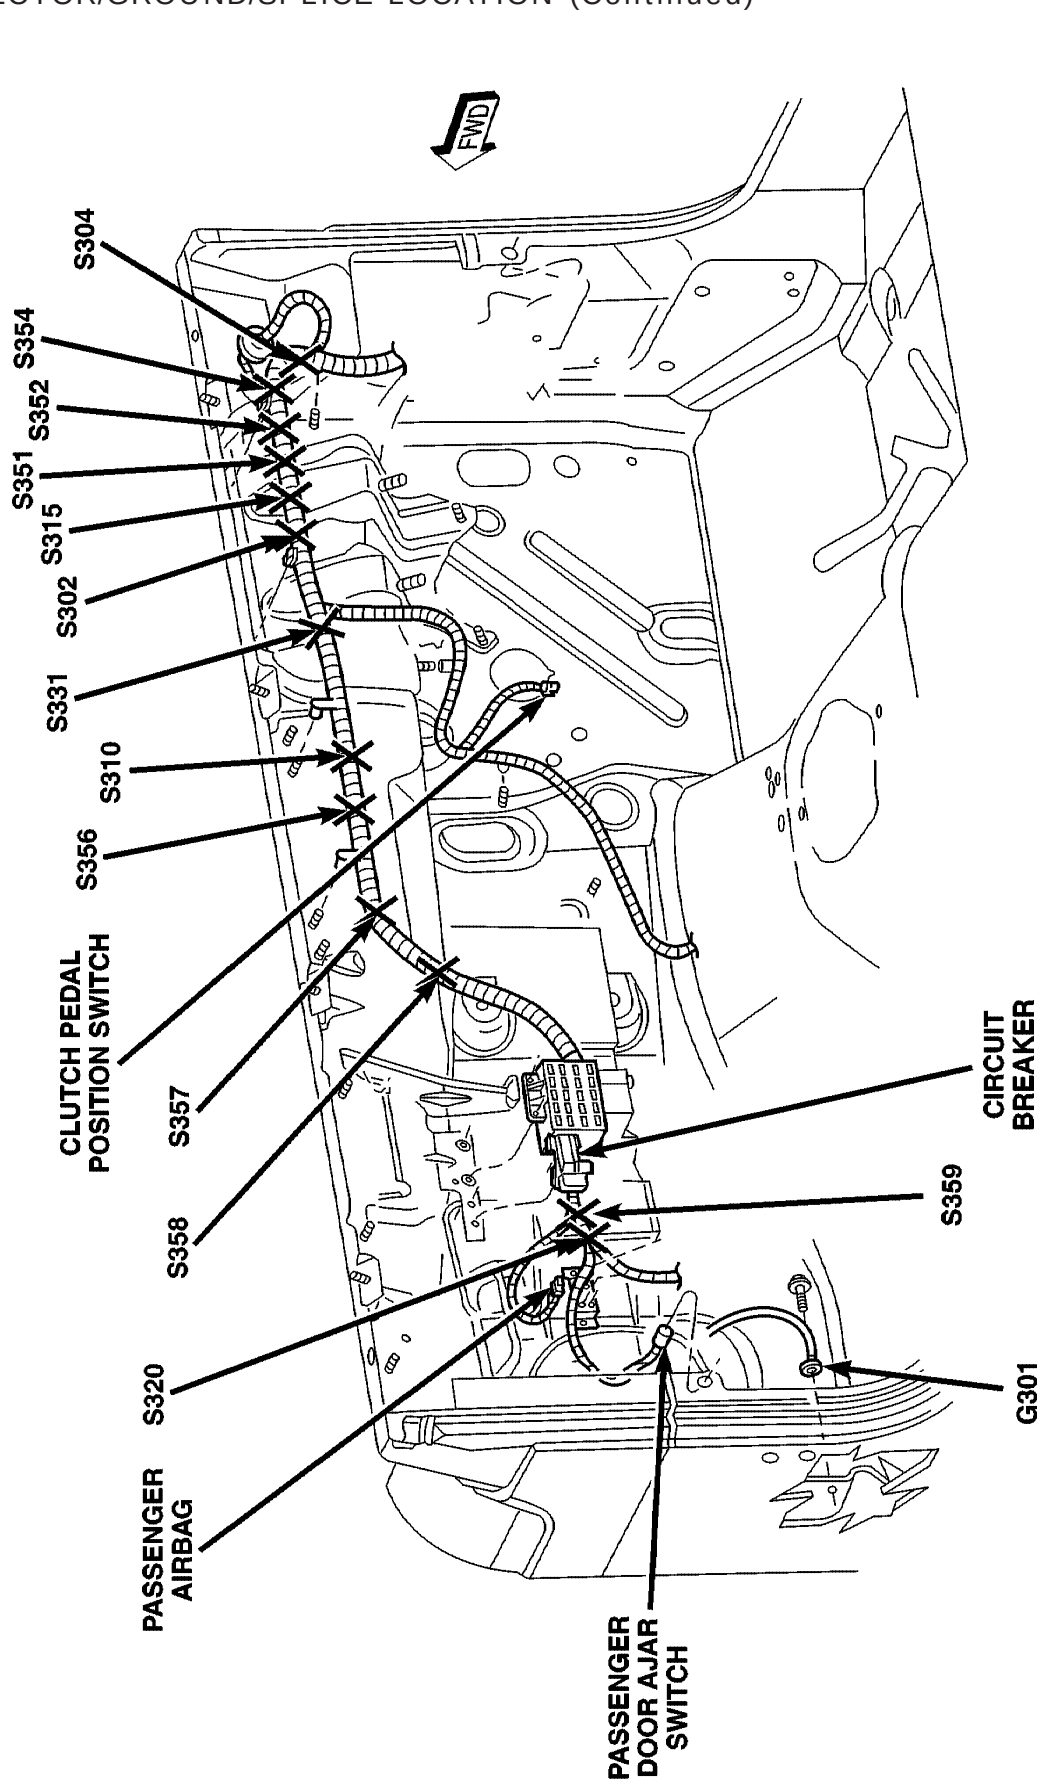


Fig. 21 -DASH PANEL (RHD)