CONNECTOR/GROUND/SPLICE LOCATION (Continued)

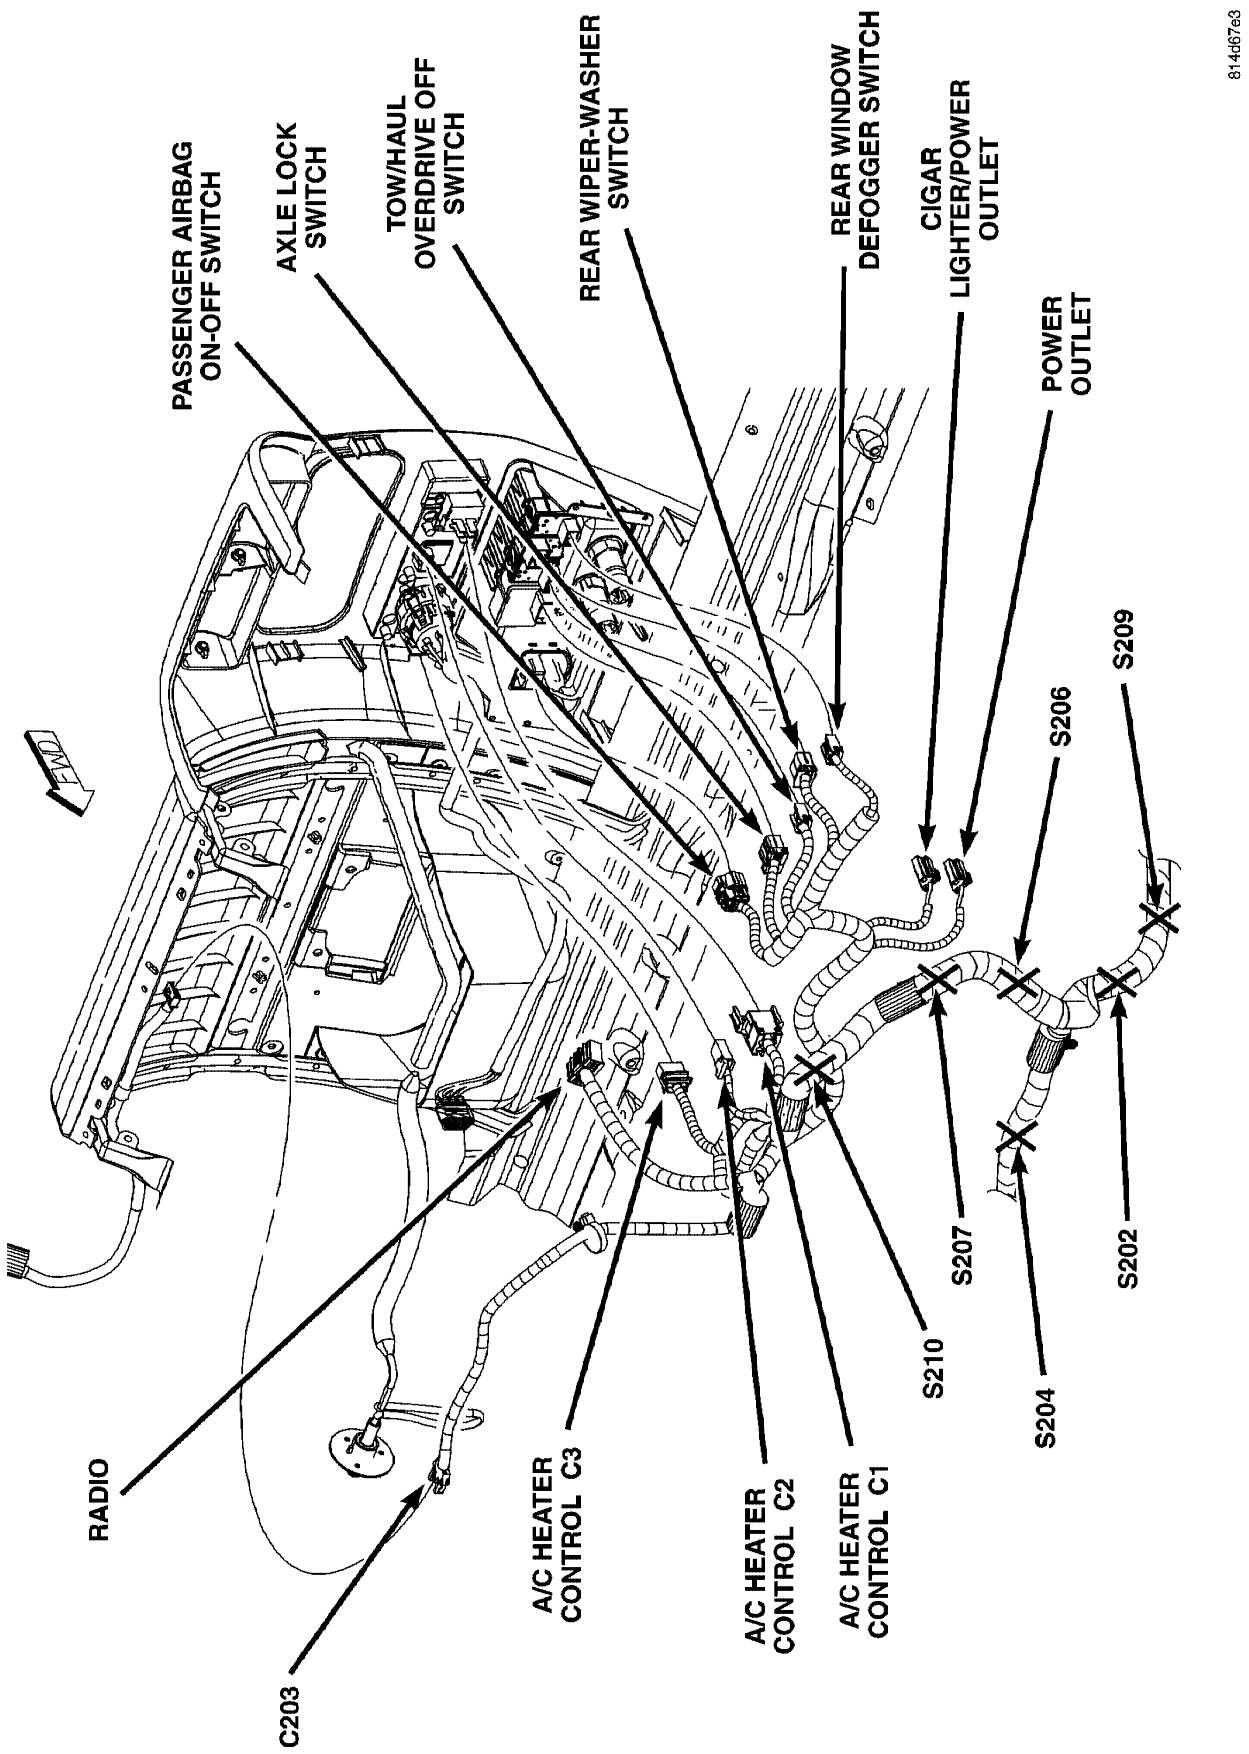


Fig. 26 -CENTER INSTRUMENT PANEL (LHD)