CONNECTOR/GROUND/SPLICE LOCATION (Continued)

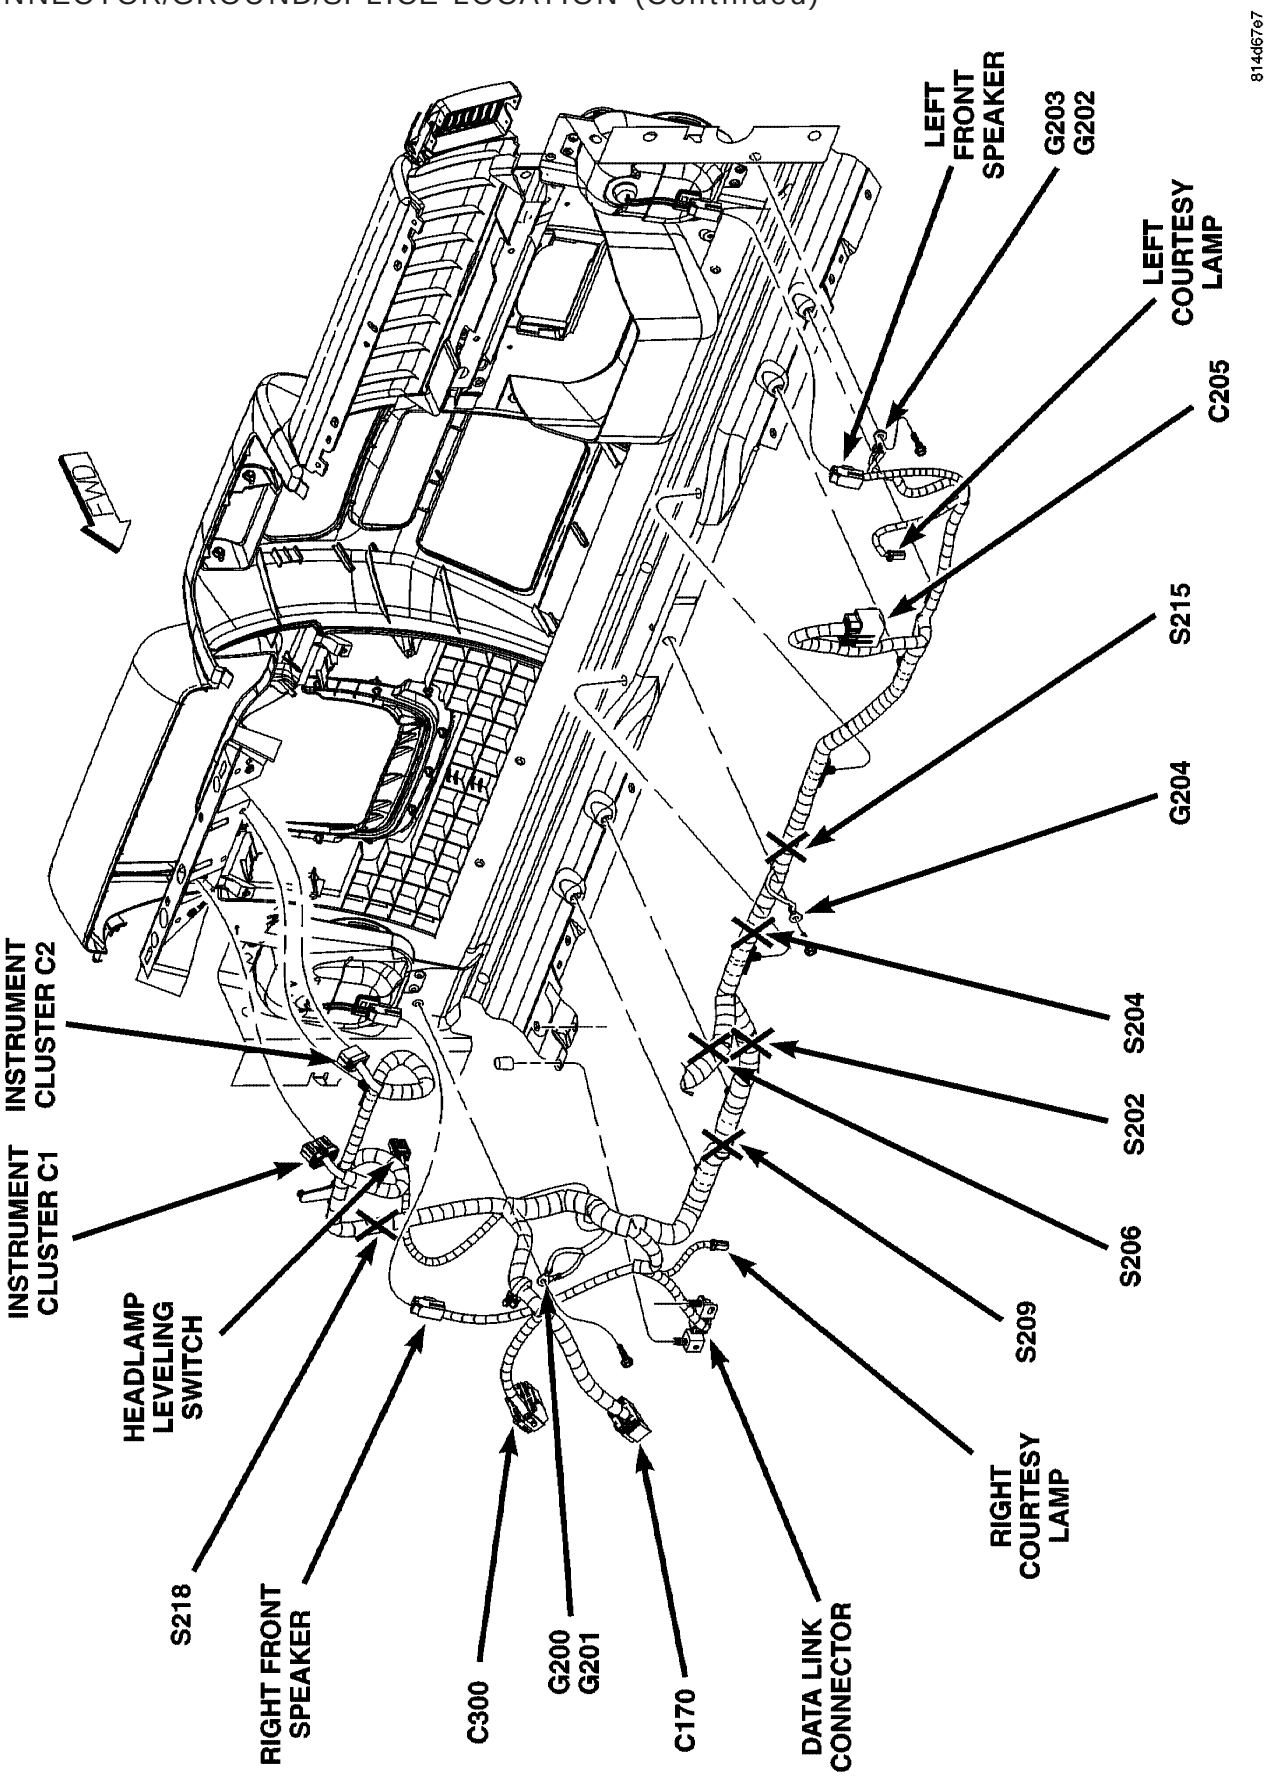


Fig. 27 -INSTRUMENT PANEL (RHD)