CONNECTOR/GROUND/SPLICE LOCATION (Continued)

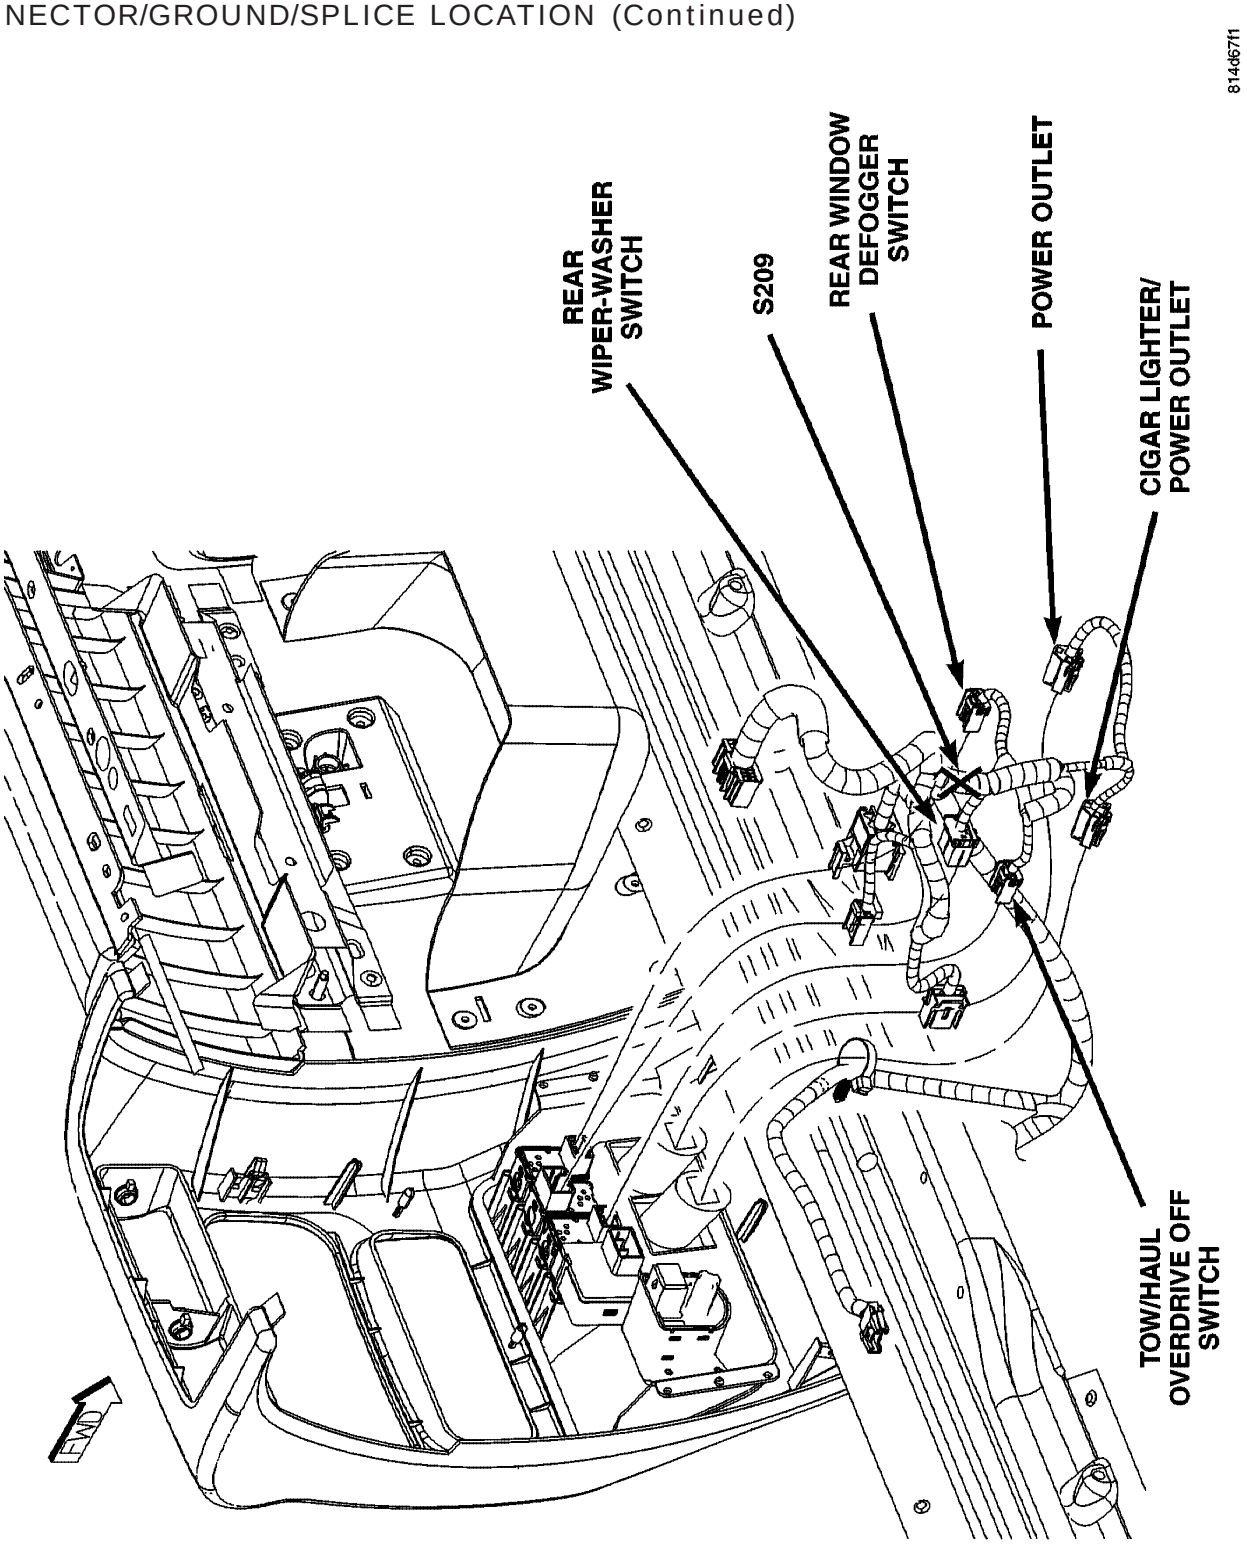


Fig. 28 -CENTER INSTRUMENT PANEL (RHD)