CONNECTOR/GROUND/SPLICE LOCATION (Continued)

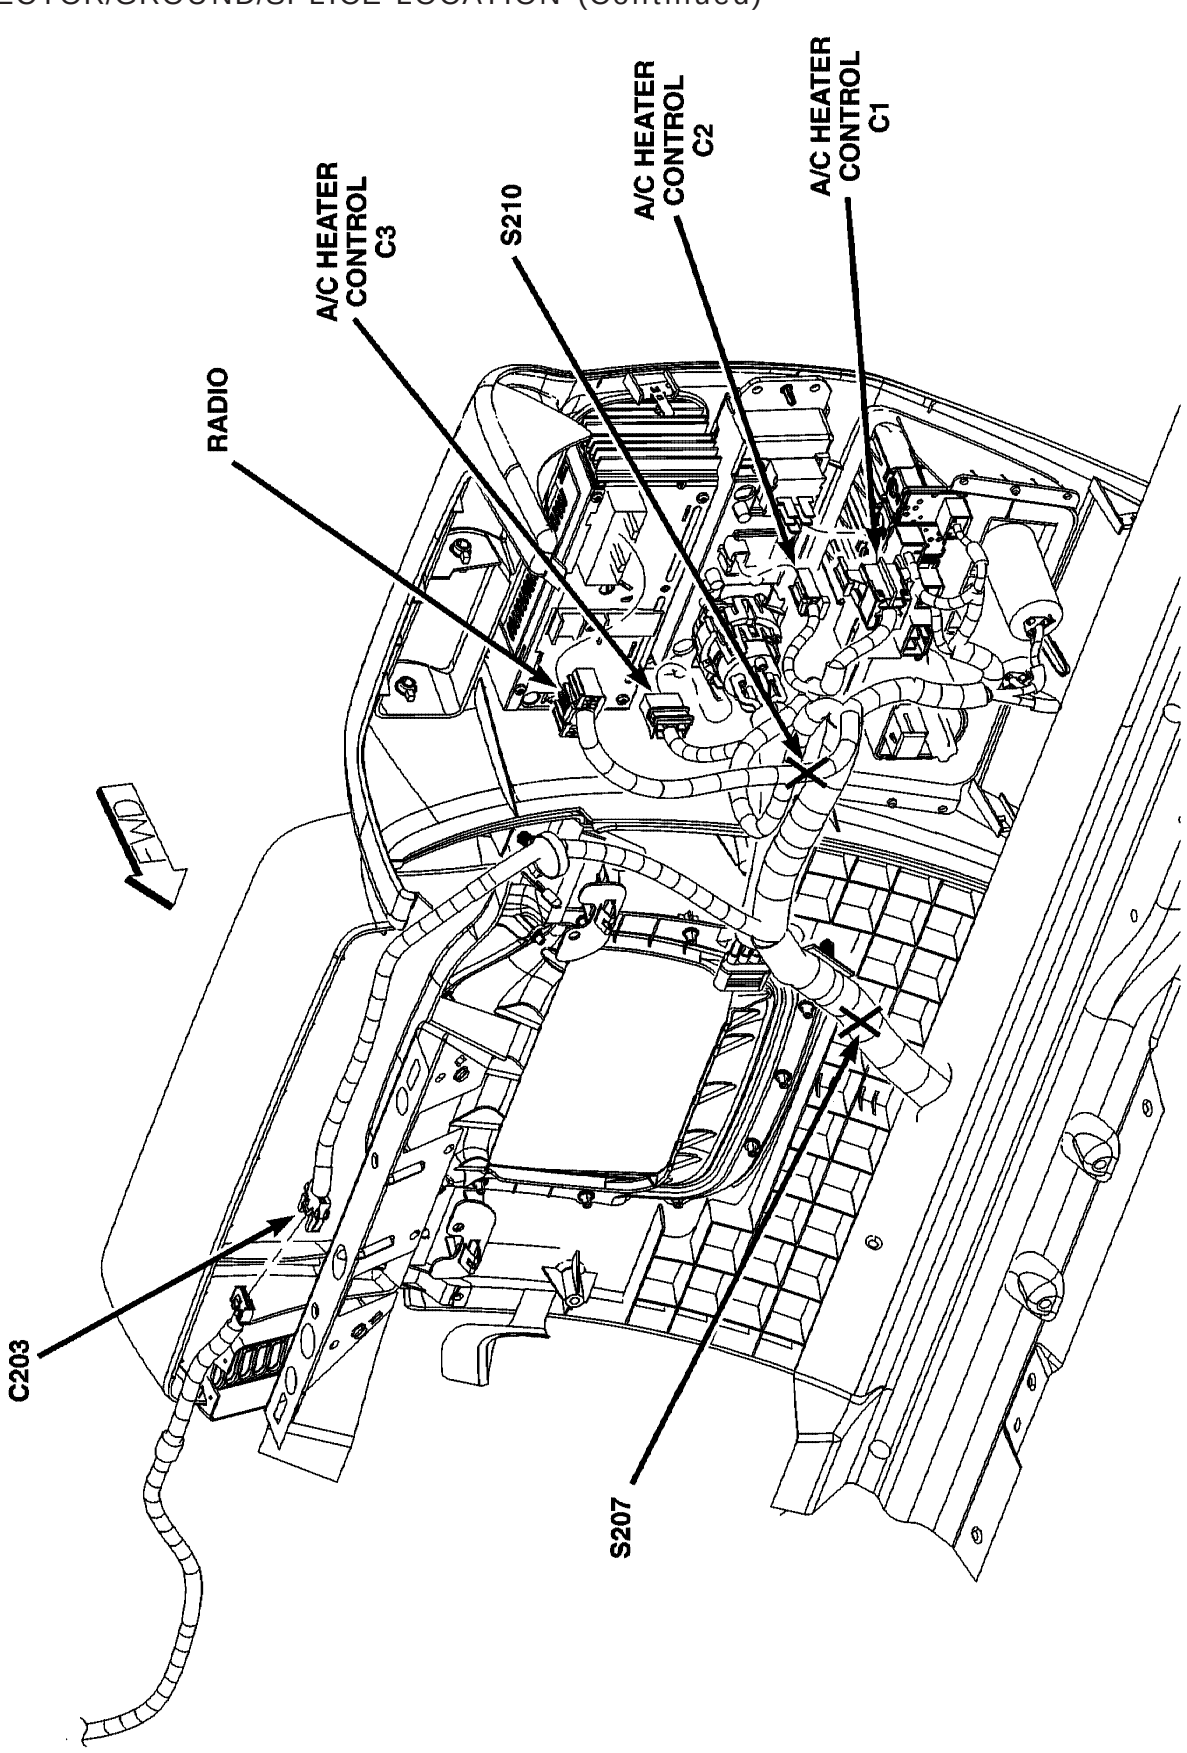


Fig. 29 -RIGHT AND CENTER INSTRUMENT PANEL (RHD)