CONNECTOR/GROUND/SPLICE LOCATION (Continued)

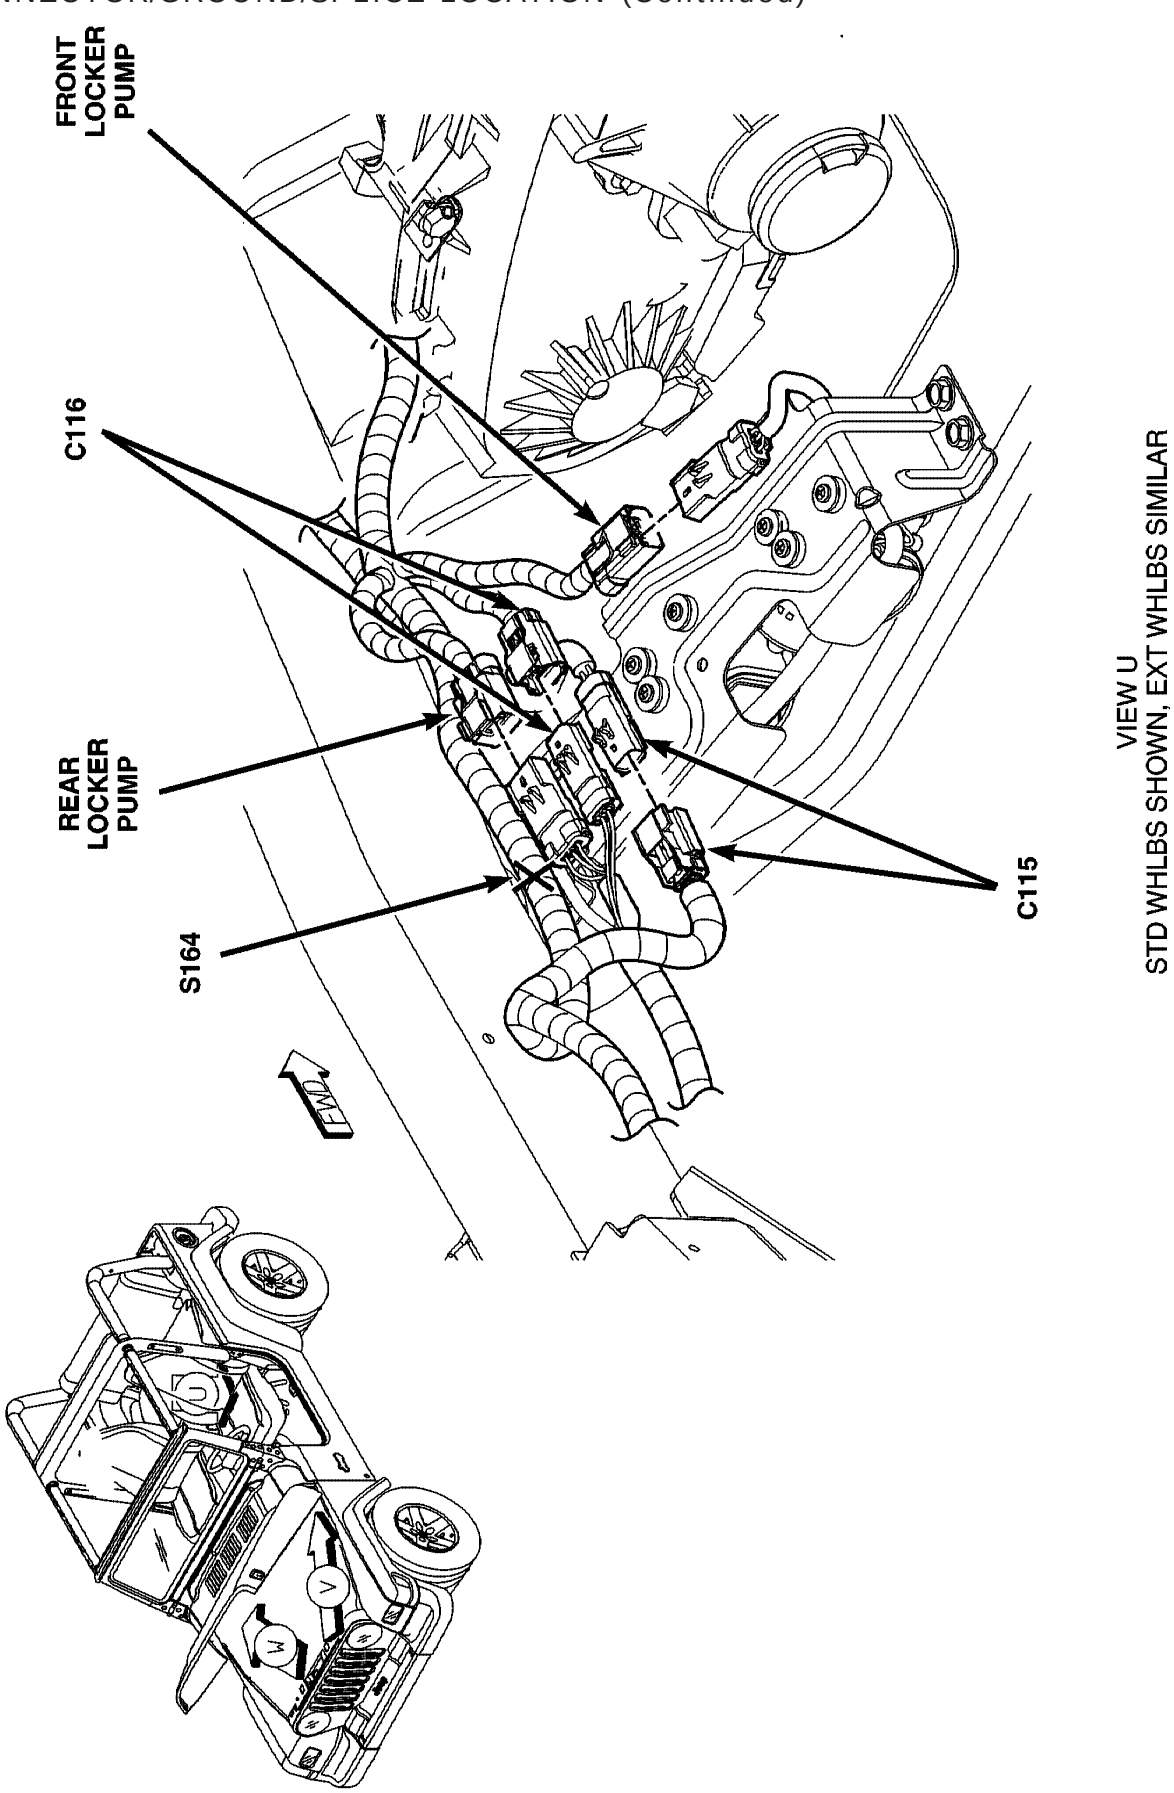


Fig. 32 -TRANSFER CASE