CONNECTOR/GROUND/SPLICE LOCATION (Continued)

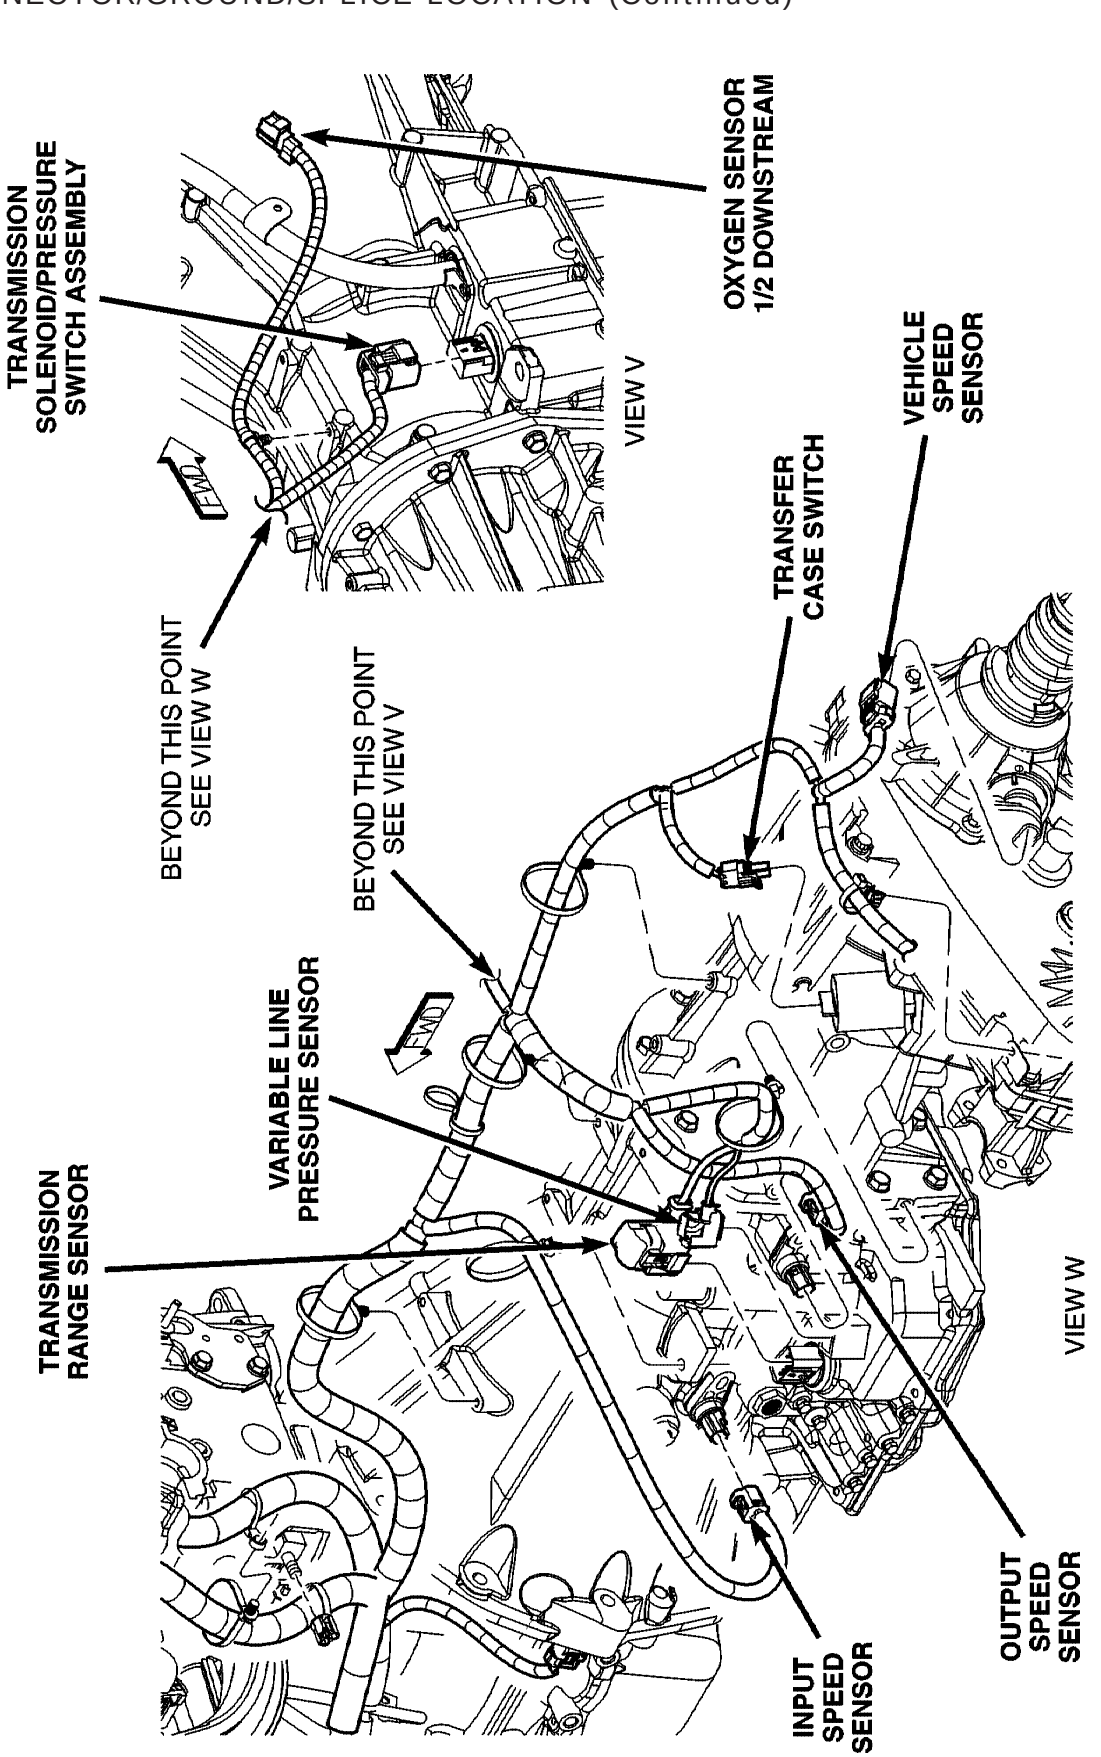



*Fig. 36 -2.4 L AUTOMATIC TRANSMISSION*