FRAME (Continued)

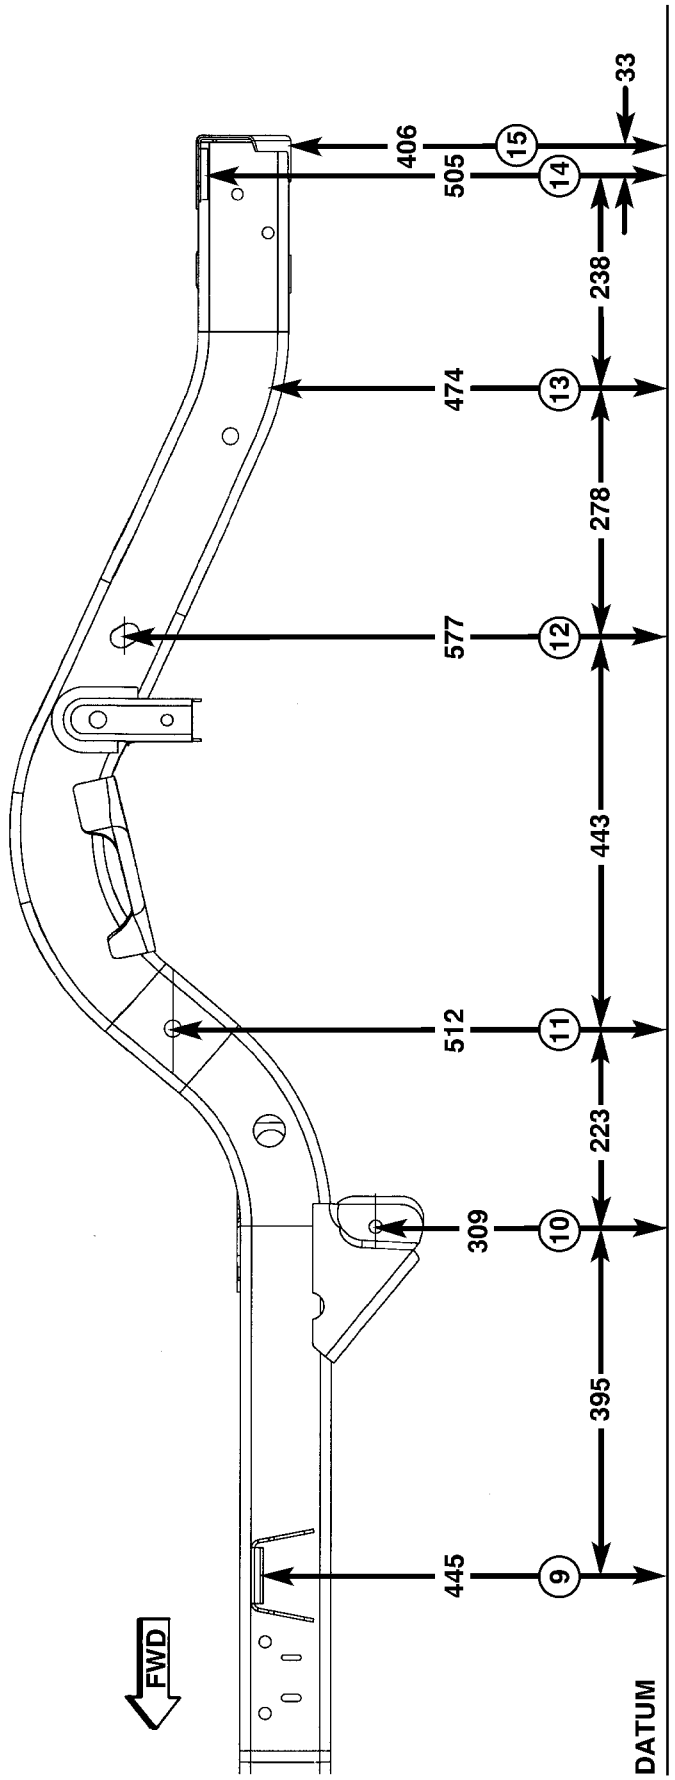

Fig. 8 FRAME SIDE VIEW LWB