FRAME (Continued)

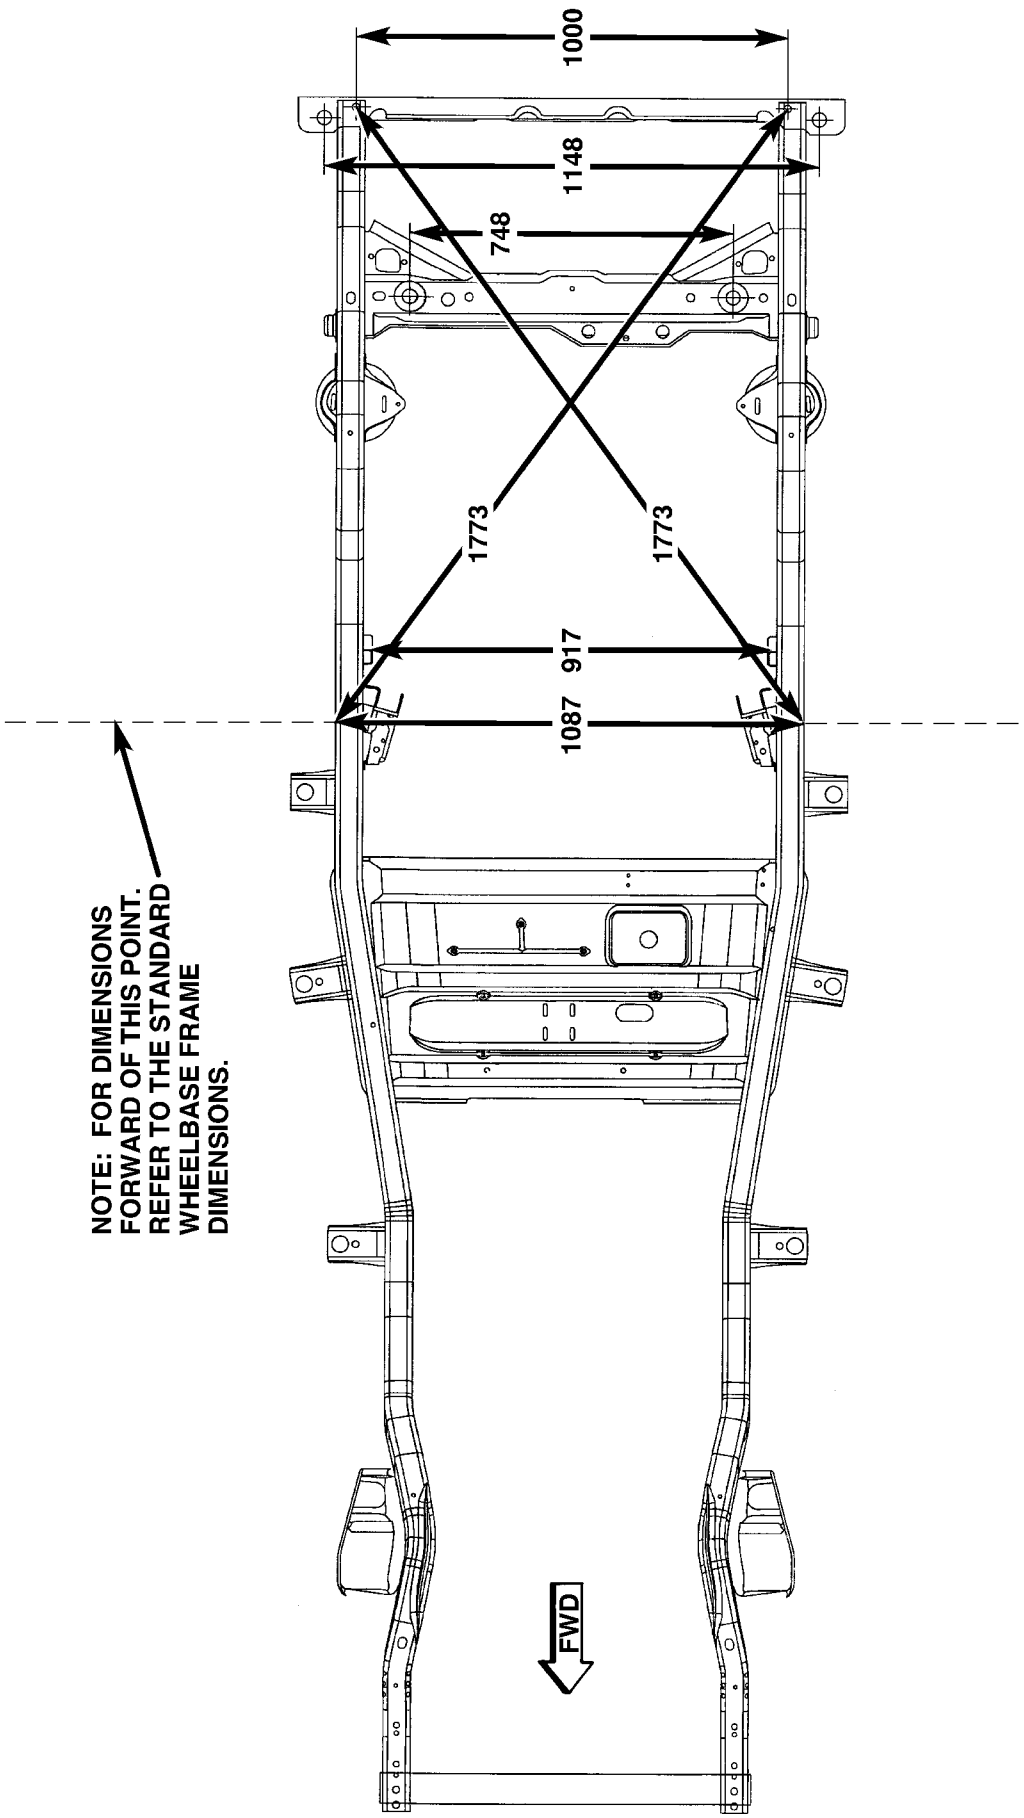

Fig. 9 FRAME TOP VIEW LWB