STRUCTURAL ADHESIVE LOCATIONS (Continued)

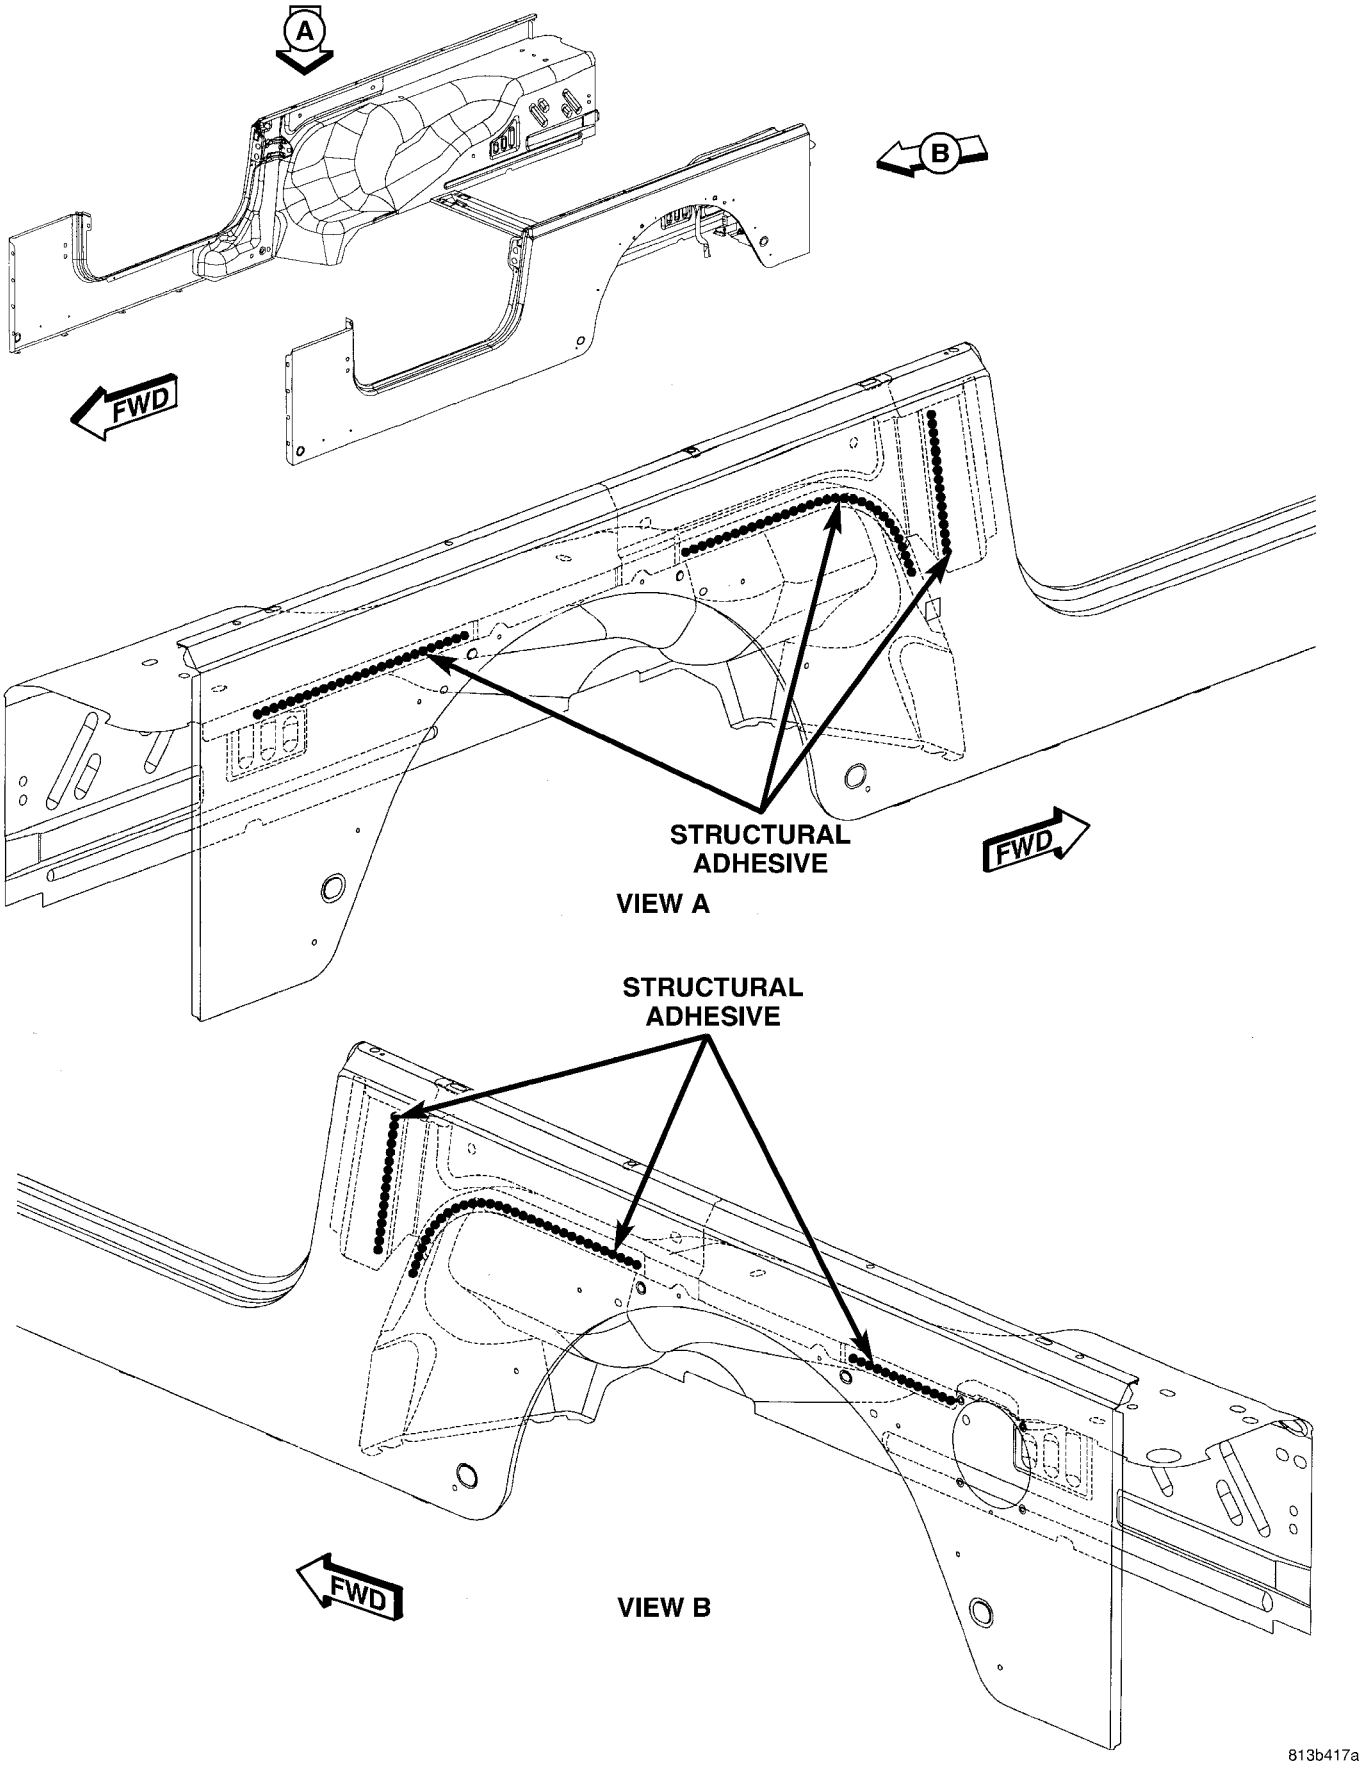

Fig. 34 BODY SIDE/WHEELHOUSE LONG WHEEL BASE (LWB)