STRUCTURAL ADHESIVE LOCATIONS (Continued)

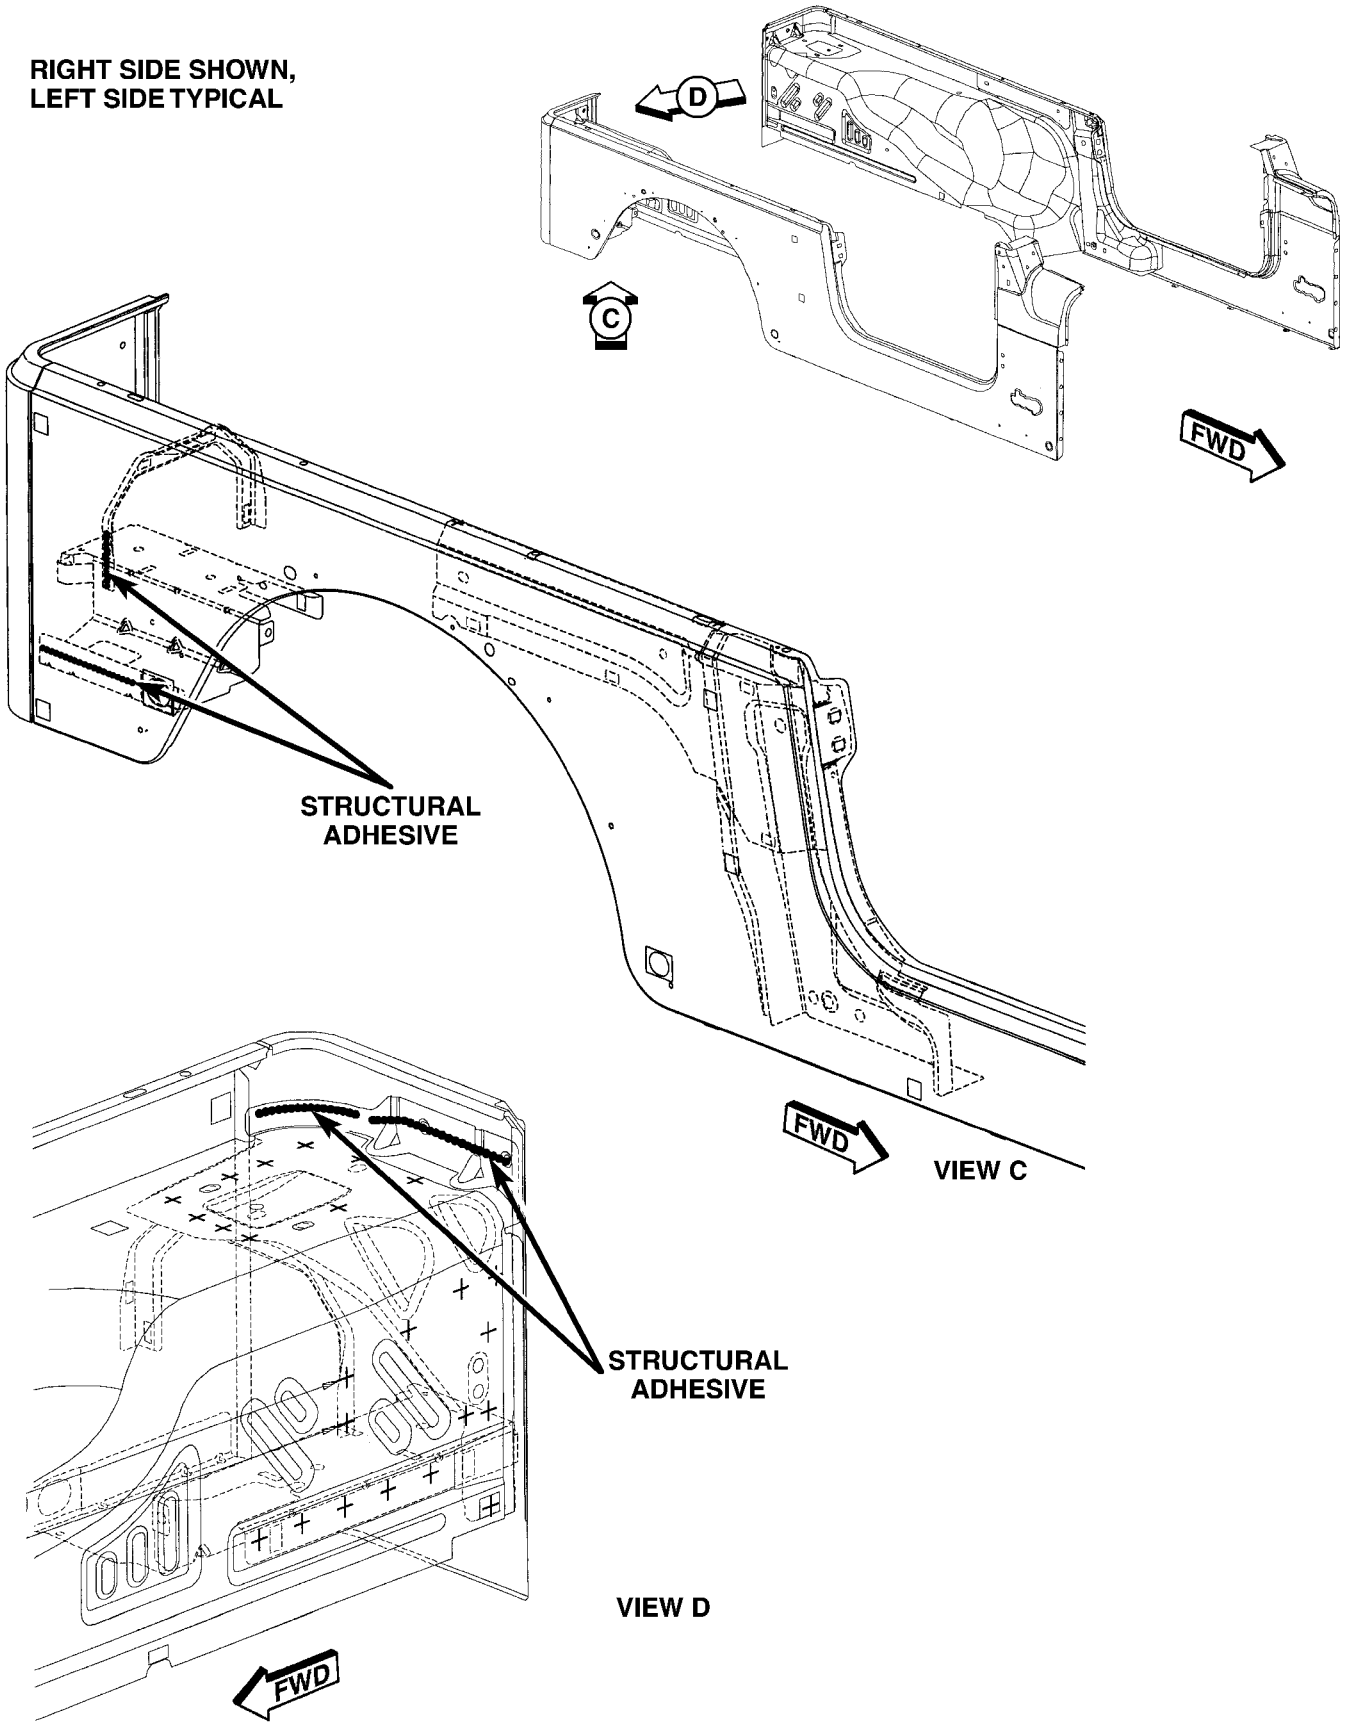

Fig. 37 BODY SIDE COMPLETE LWB