WELD LOCATIONS (Continued)

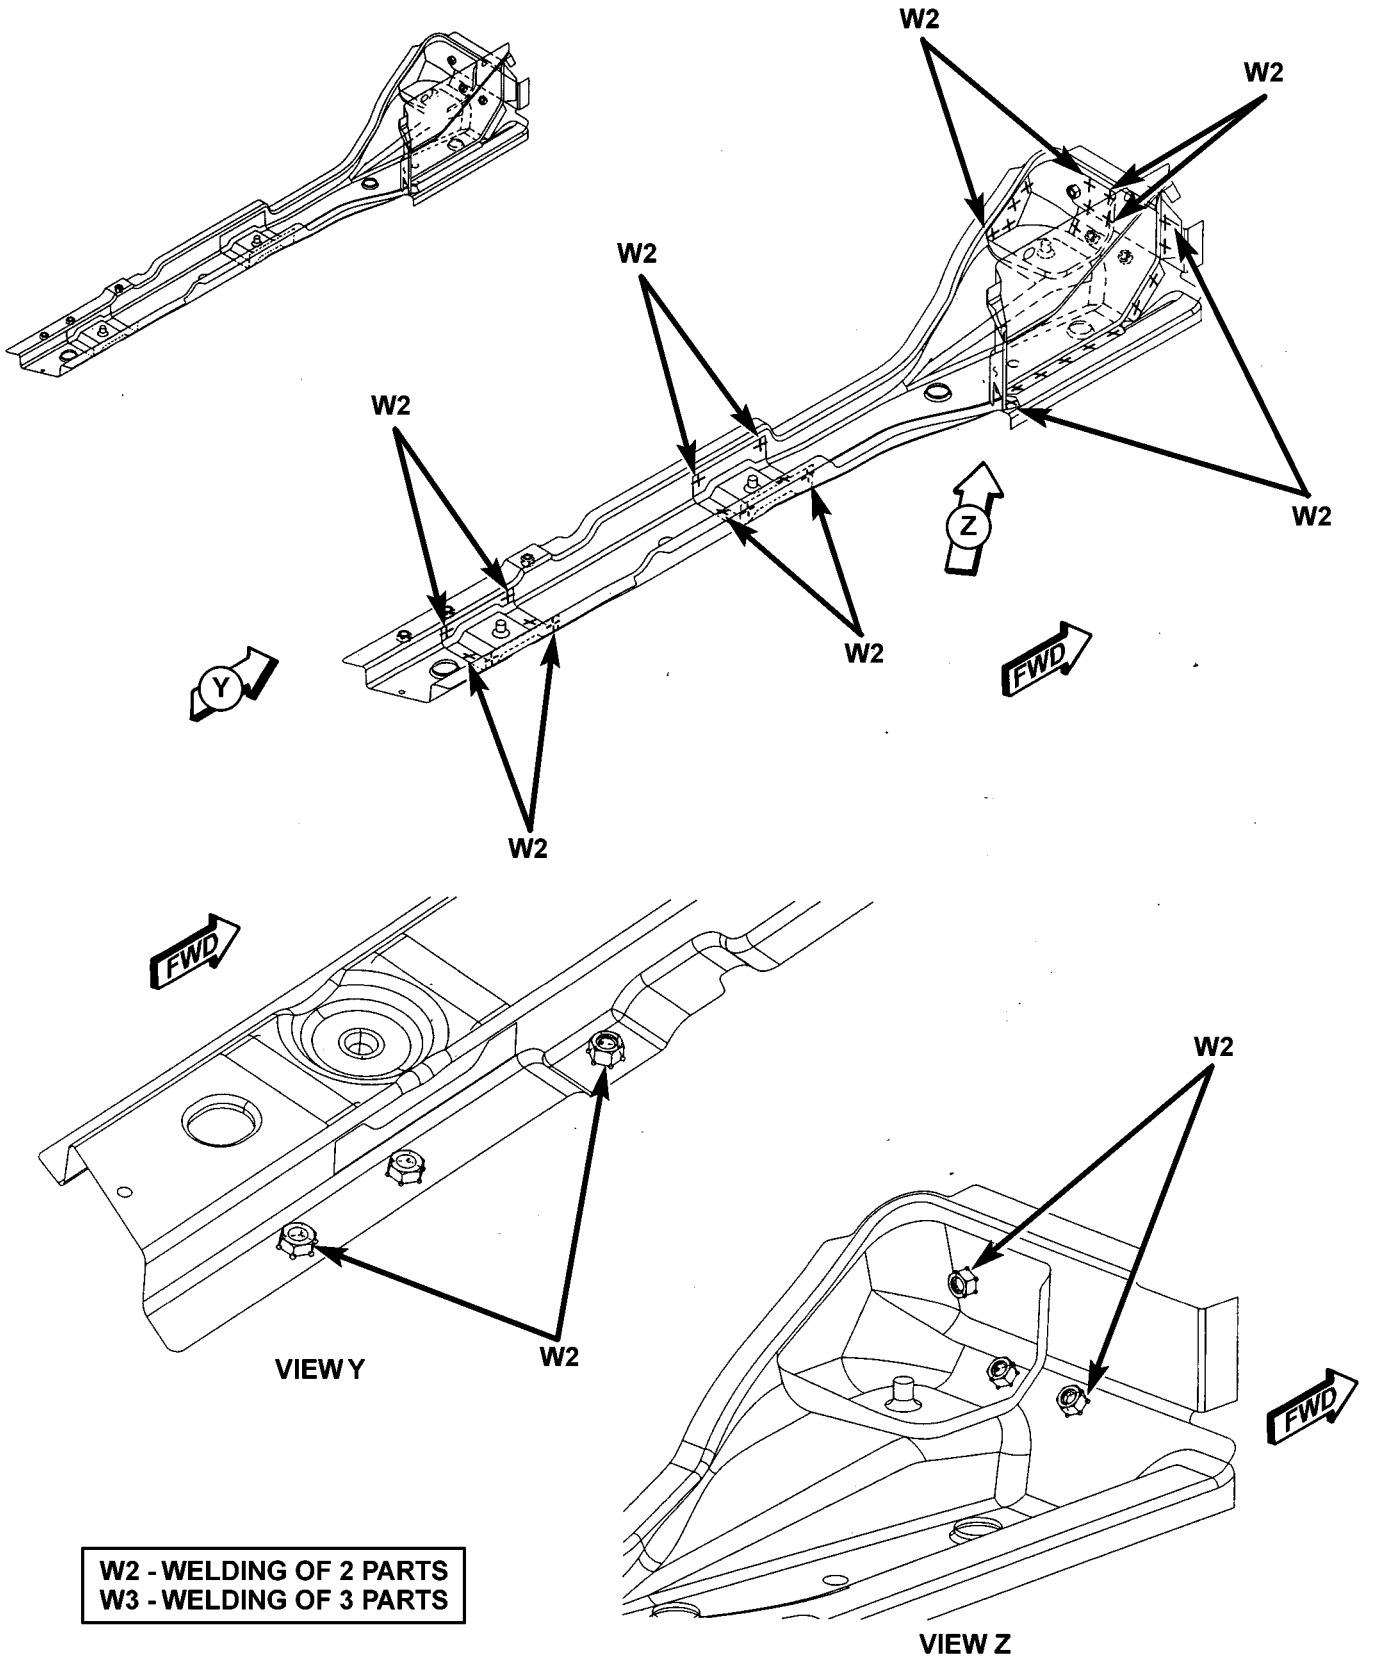

BOTH SIDES TYPICAL

80f8586e

Fig. 39 CROSSMEMBERS/STRAINERS