WELD LOCATIONS (Continued)

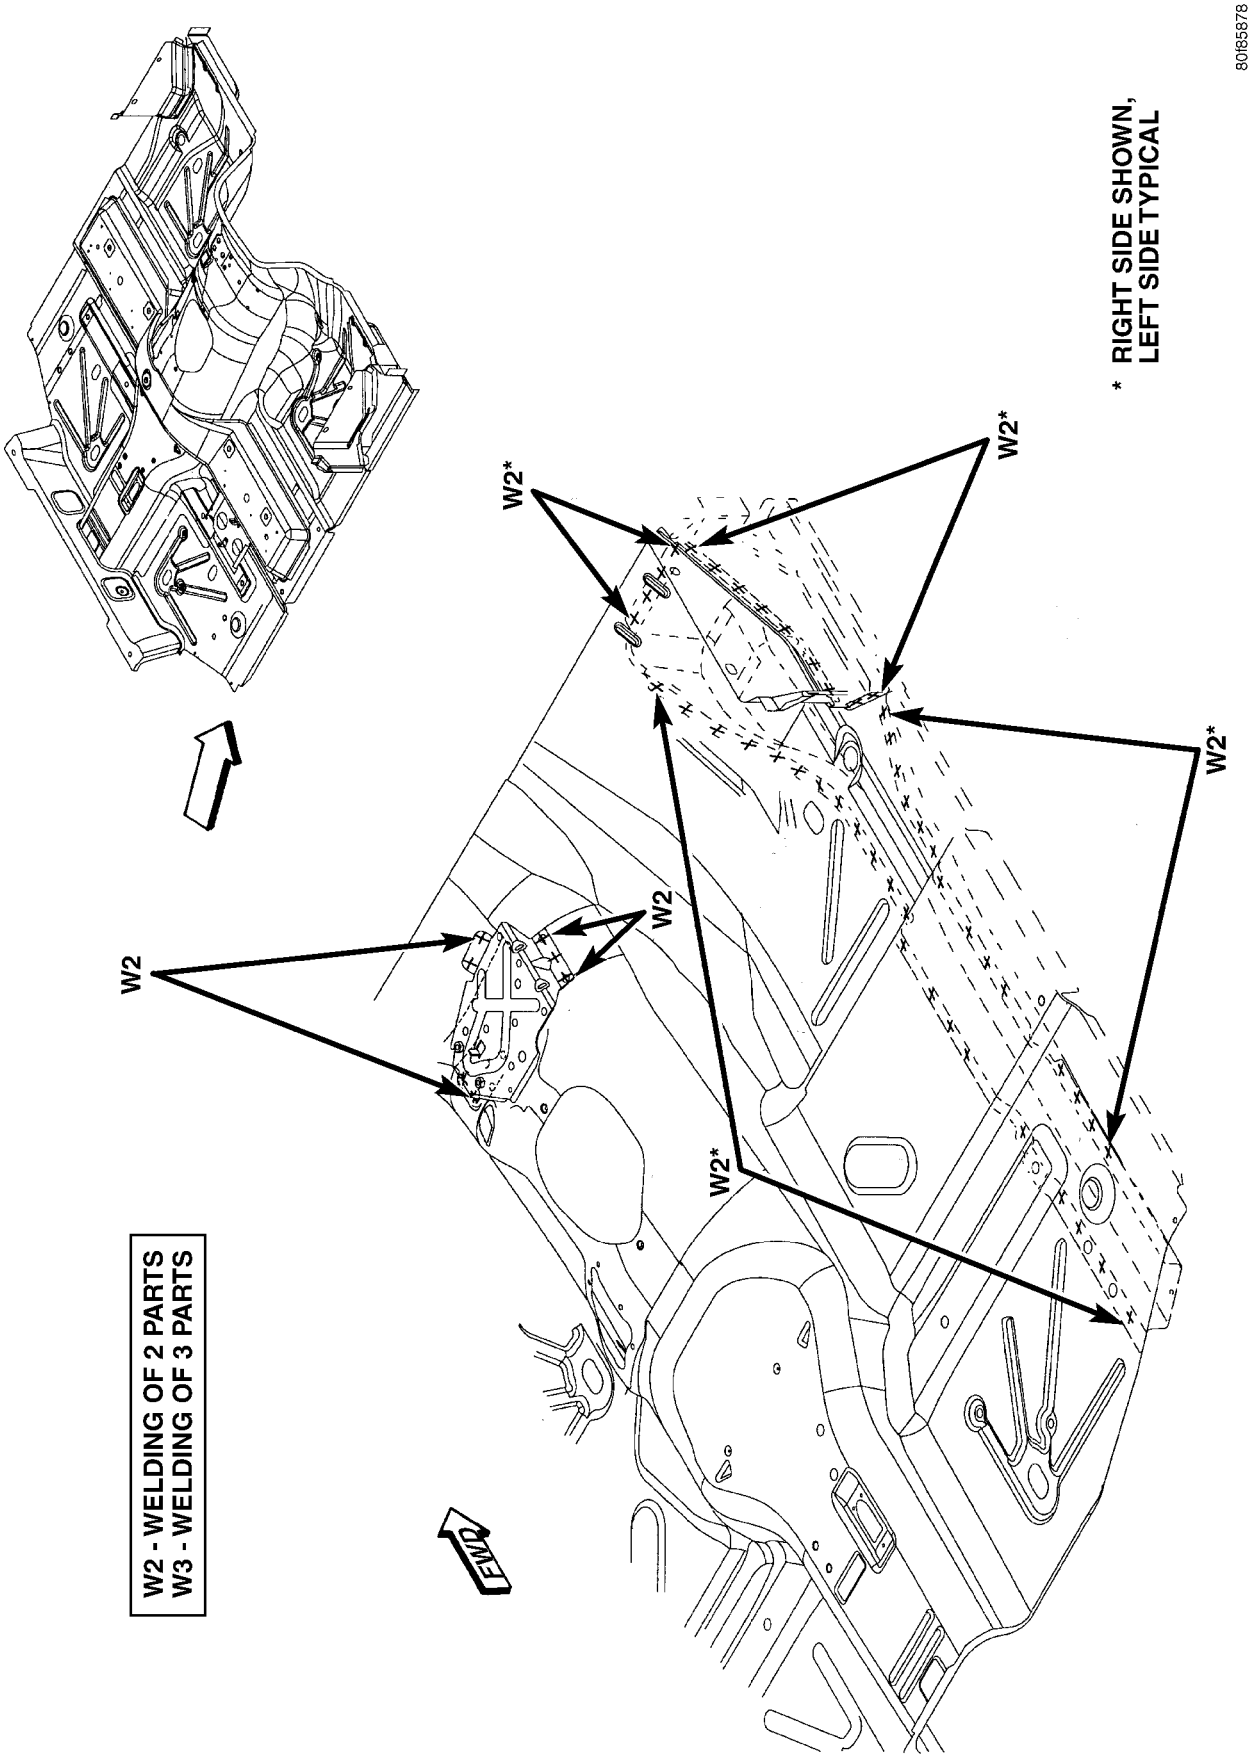

Fig. 40 FRONT FLOOR PAN (1 OF 3)