WELD LOCATIONS (Continued)

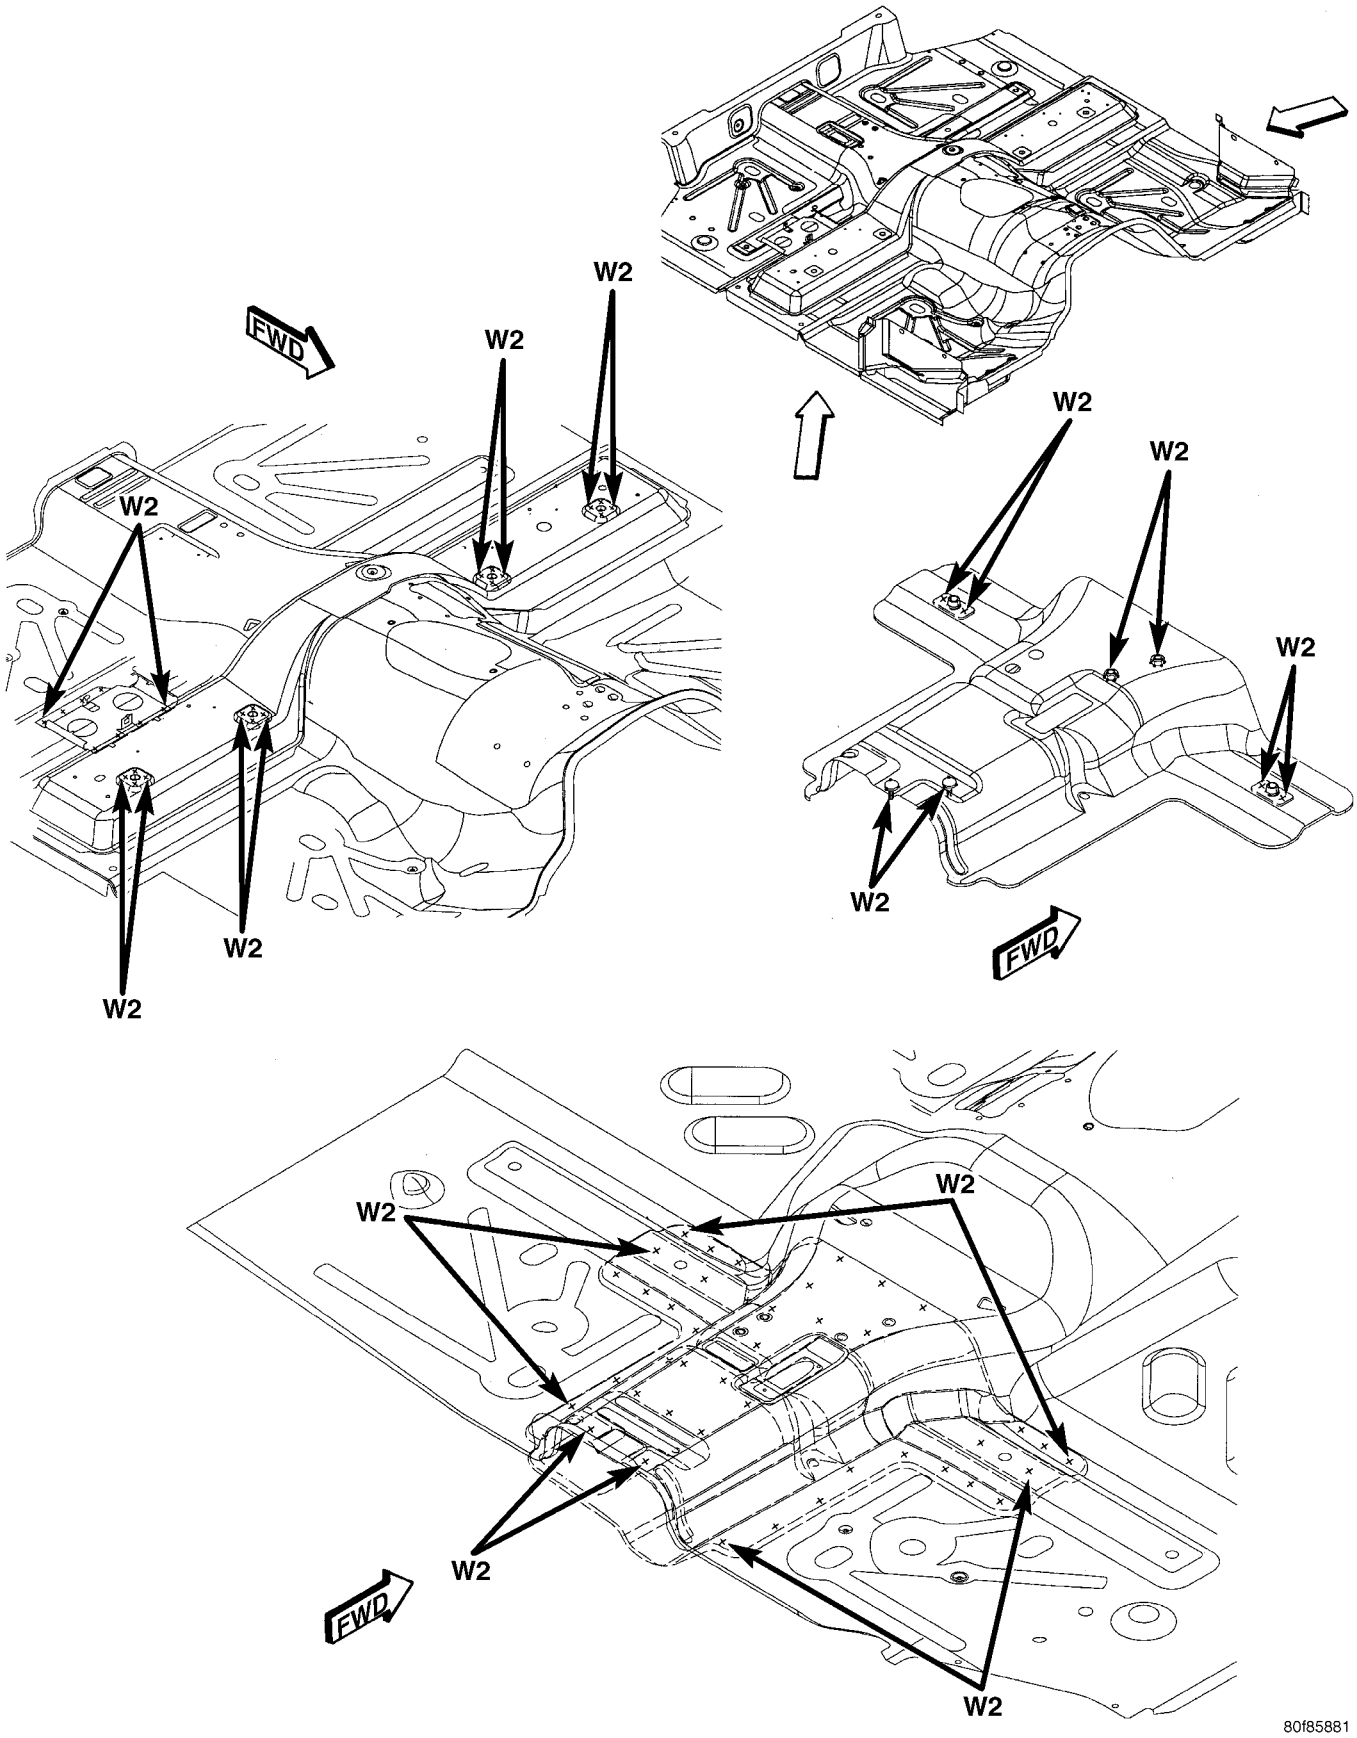


Fig. 42 FRONT FLOOR PAN (3 OF 3)