WELD LOCATIONS (Continued)

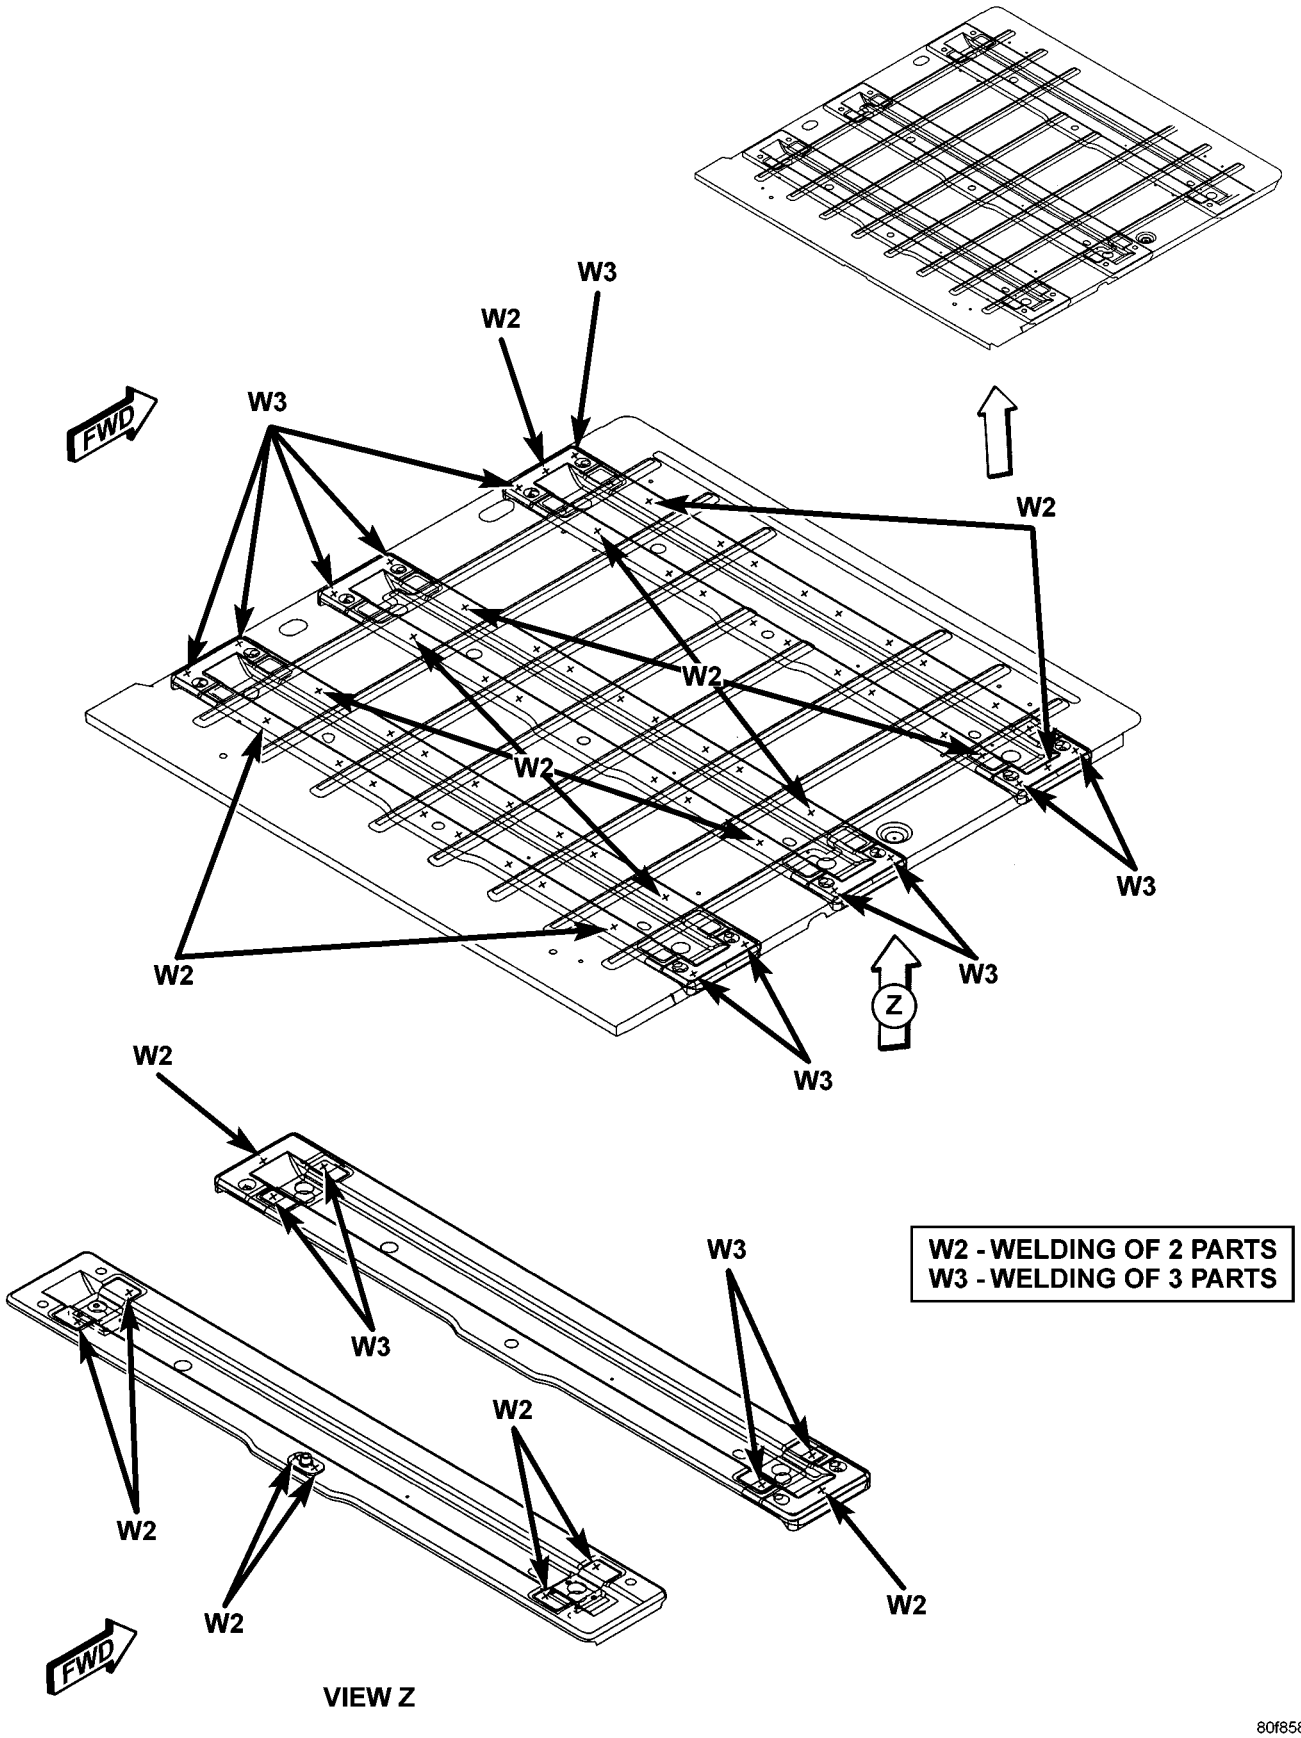


Fig. 43 REAR FLOOR PAN (1 OF 2)