WELD LOCATIONS (Continued)

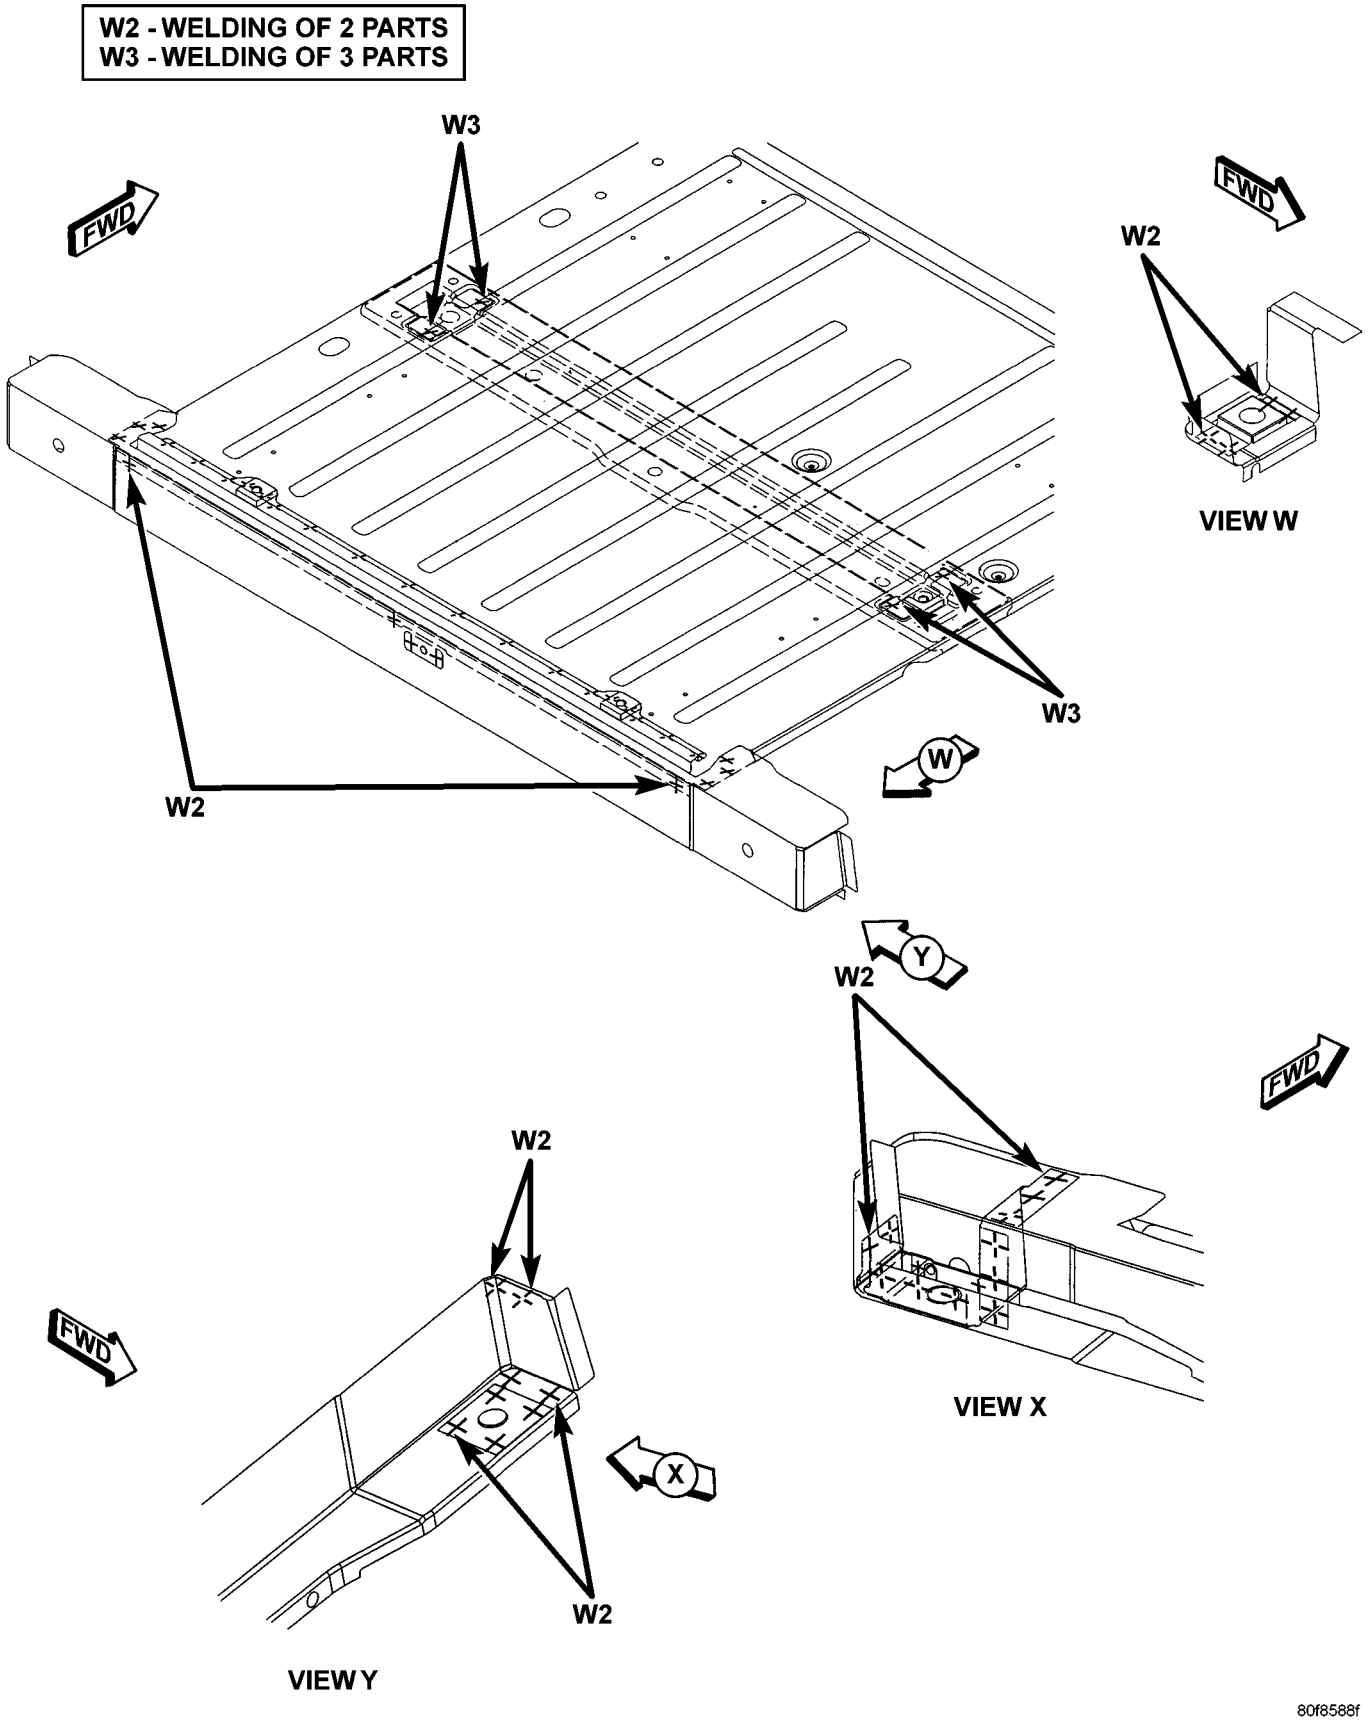

Fig. 44 REAR FLOOR PAN (2 OF 2)