WELD LOCATIONS (Continued)

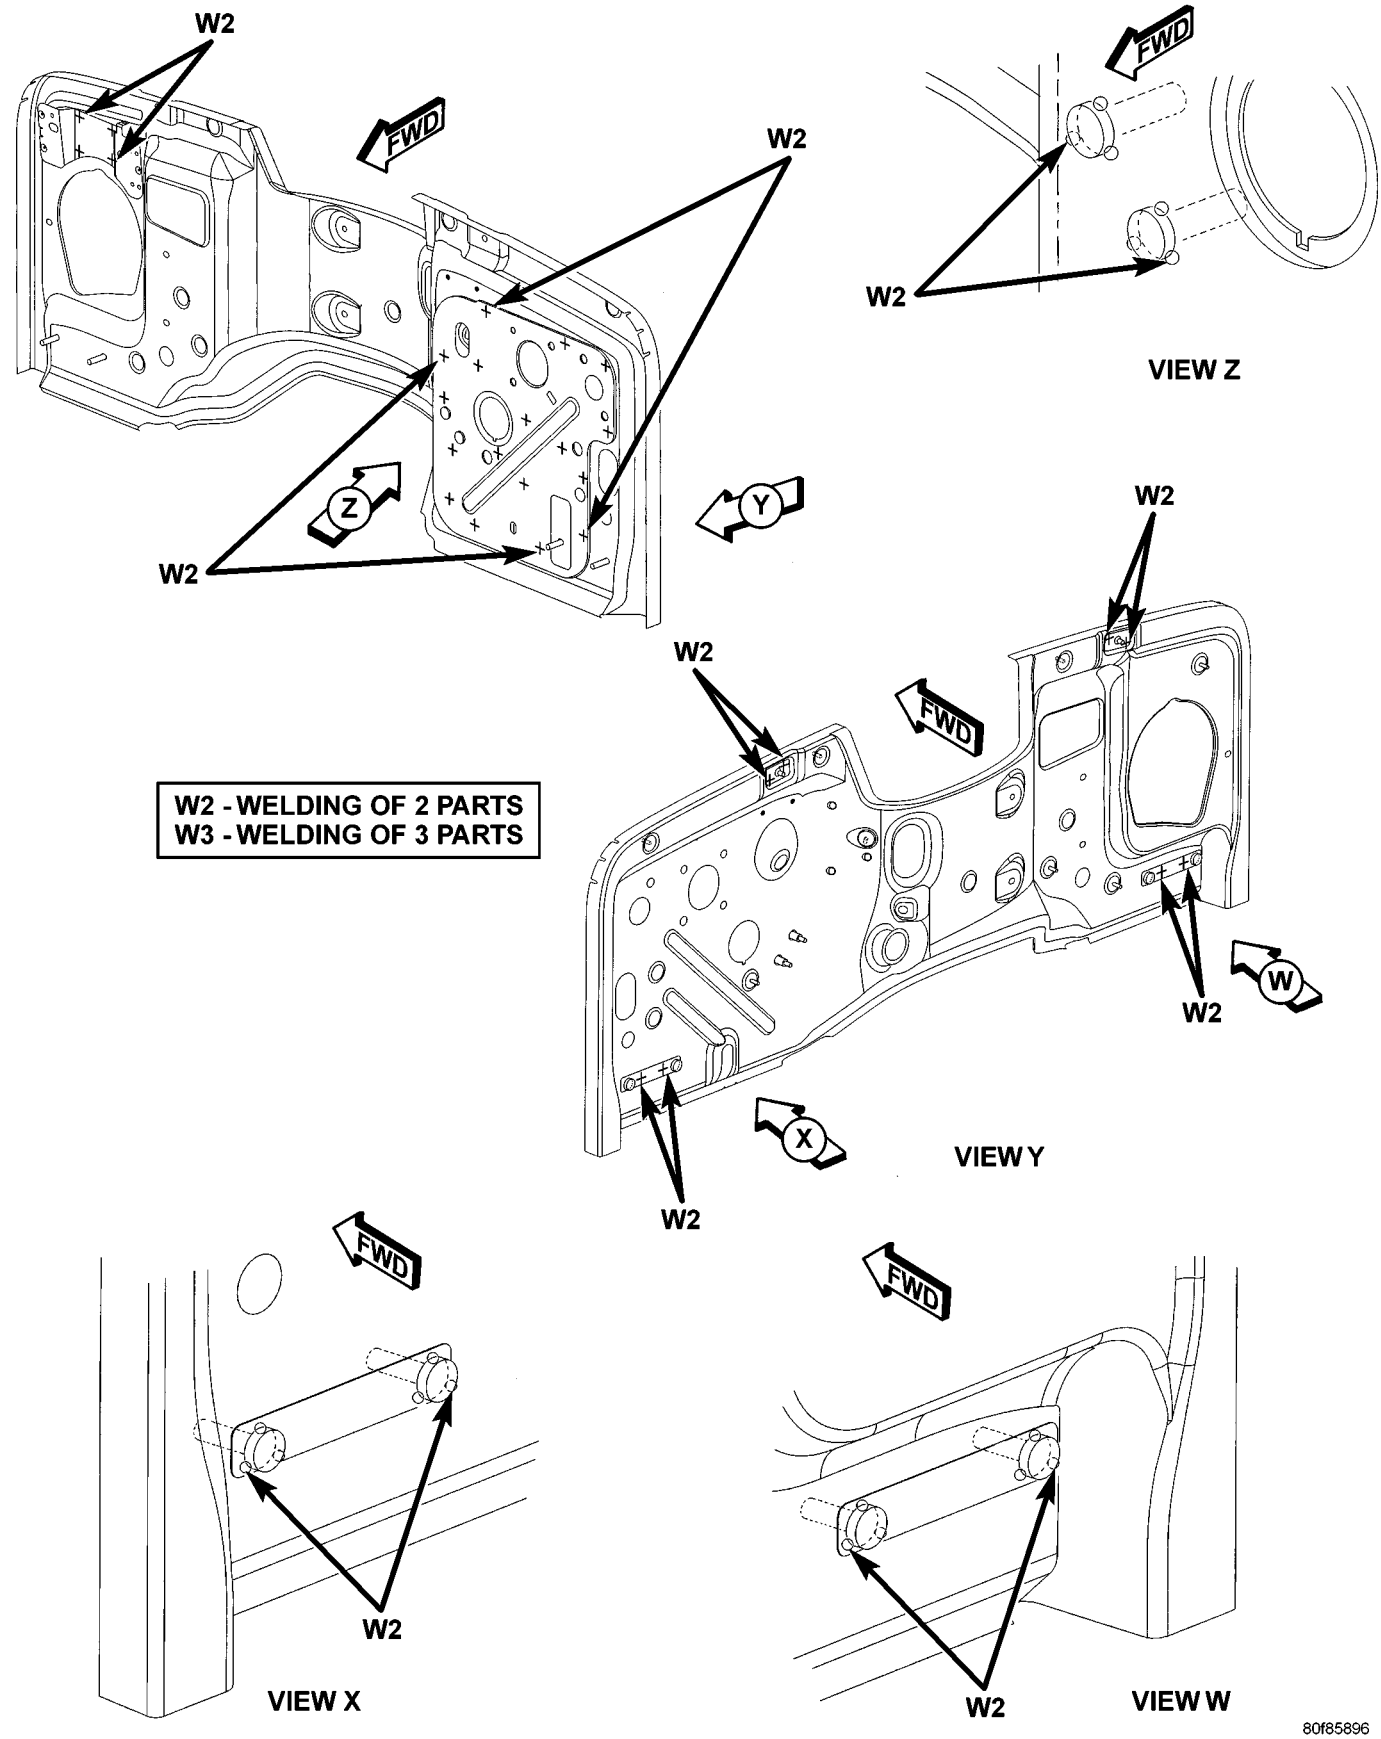

Fig. 45 DASH PANEL - LEFT HAND DRIVE