WELD LOCATIONS (Continued)

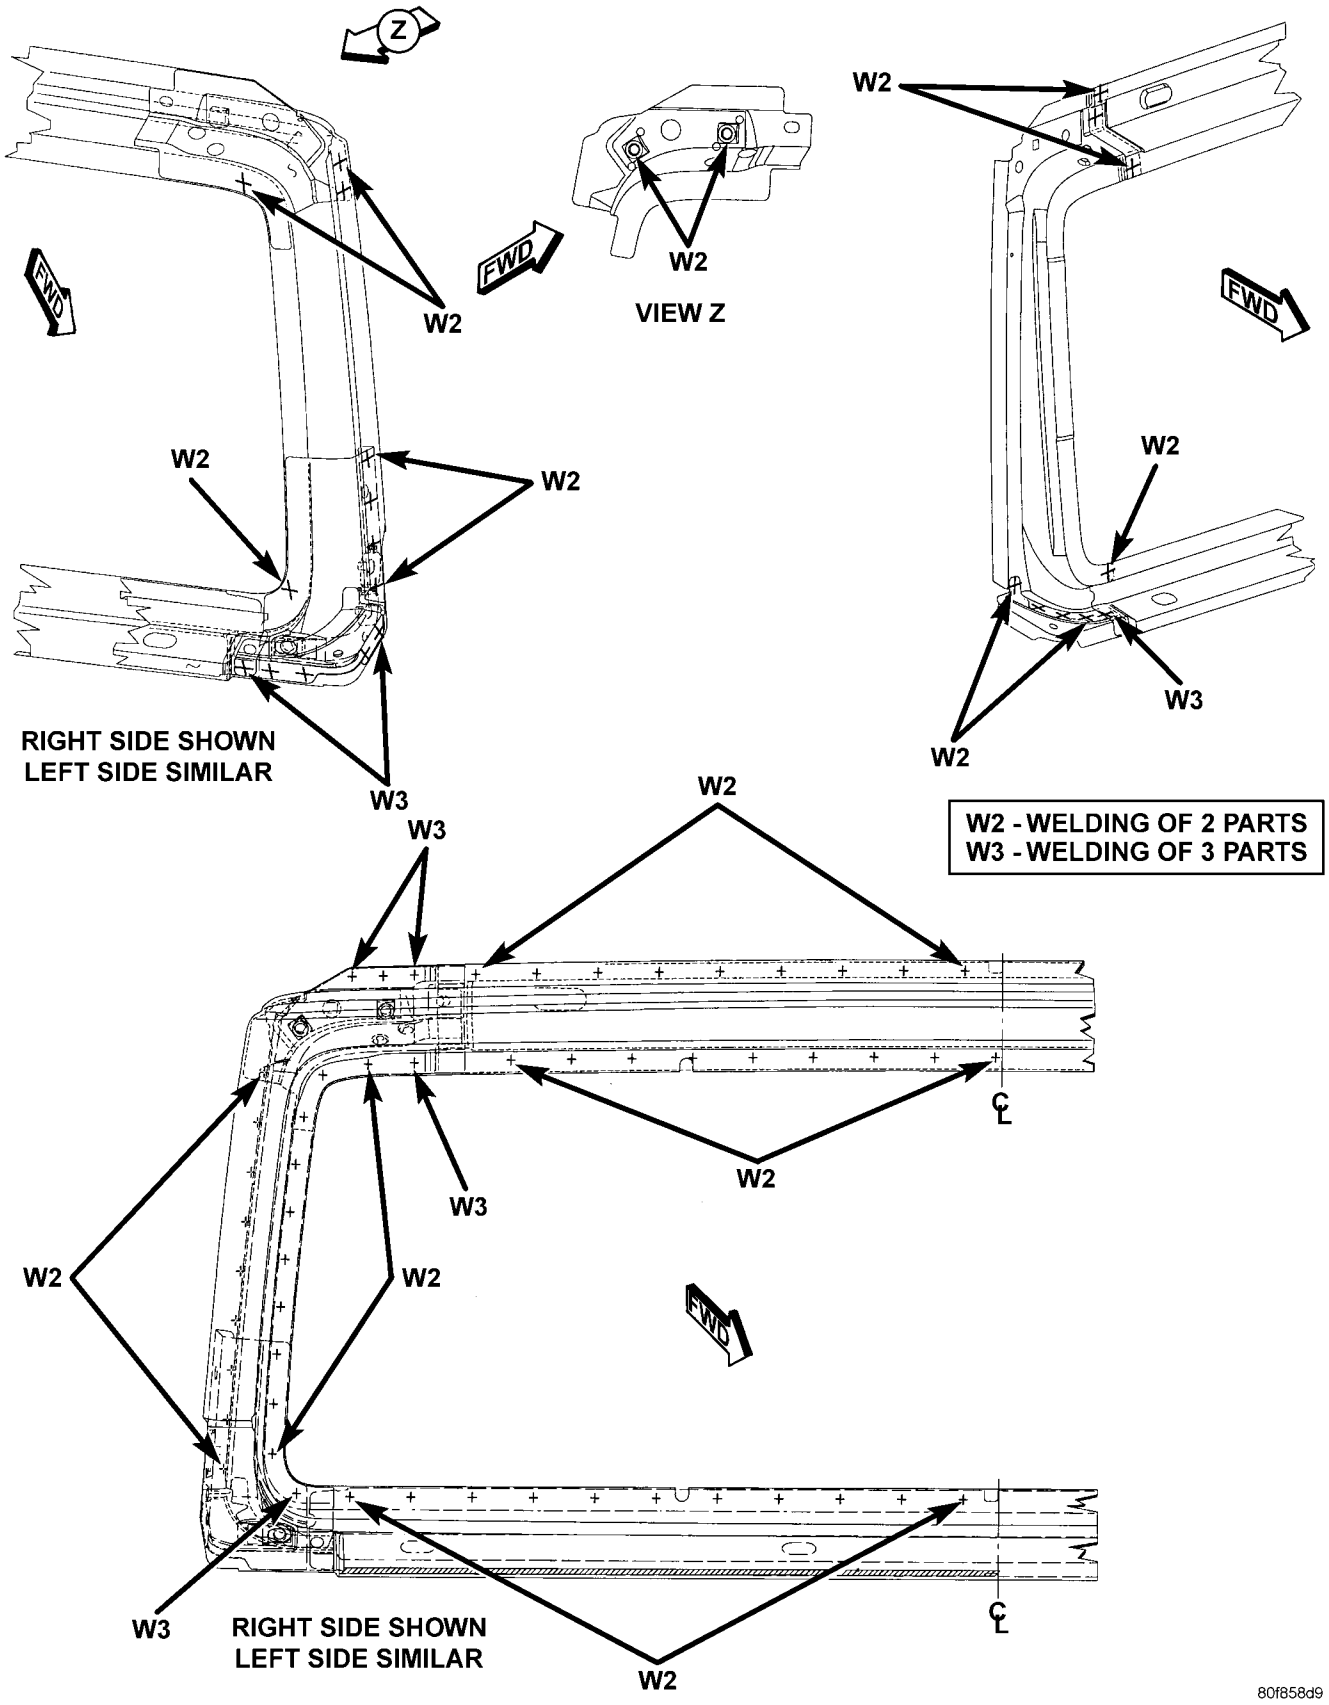

Fig. 50 WINDSHIELD FRAME