WELD LOCATIONS (Continued)

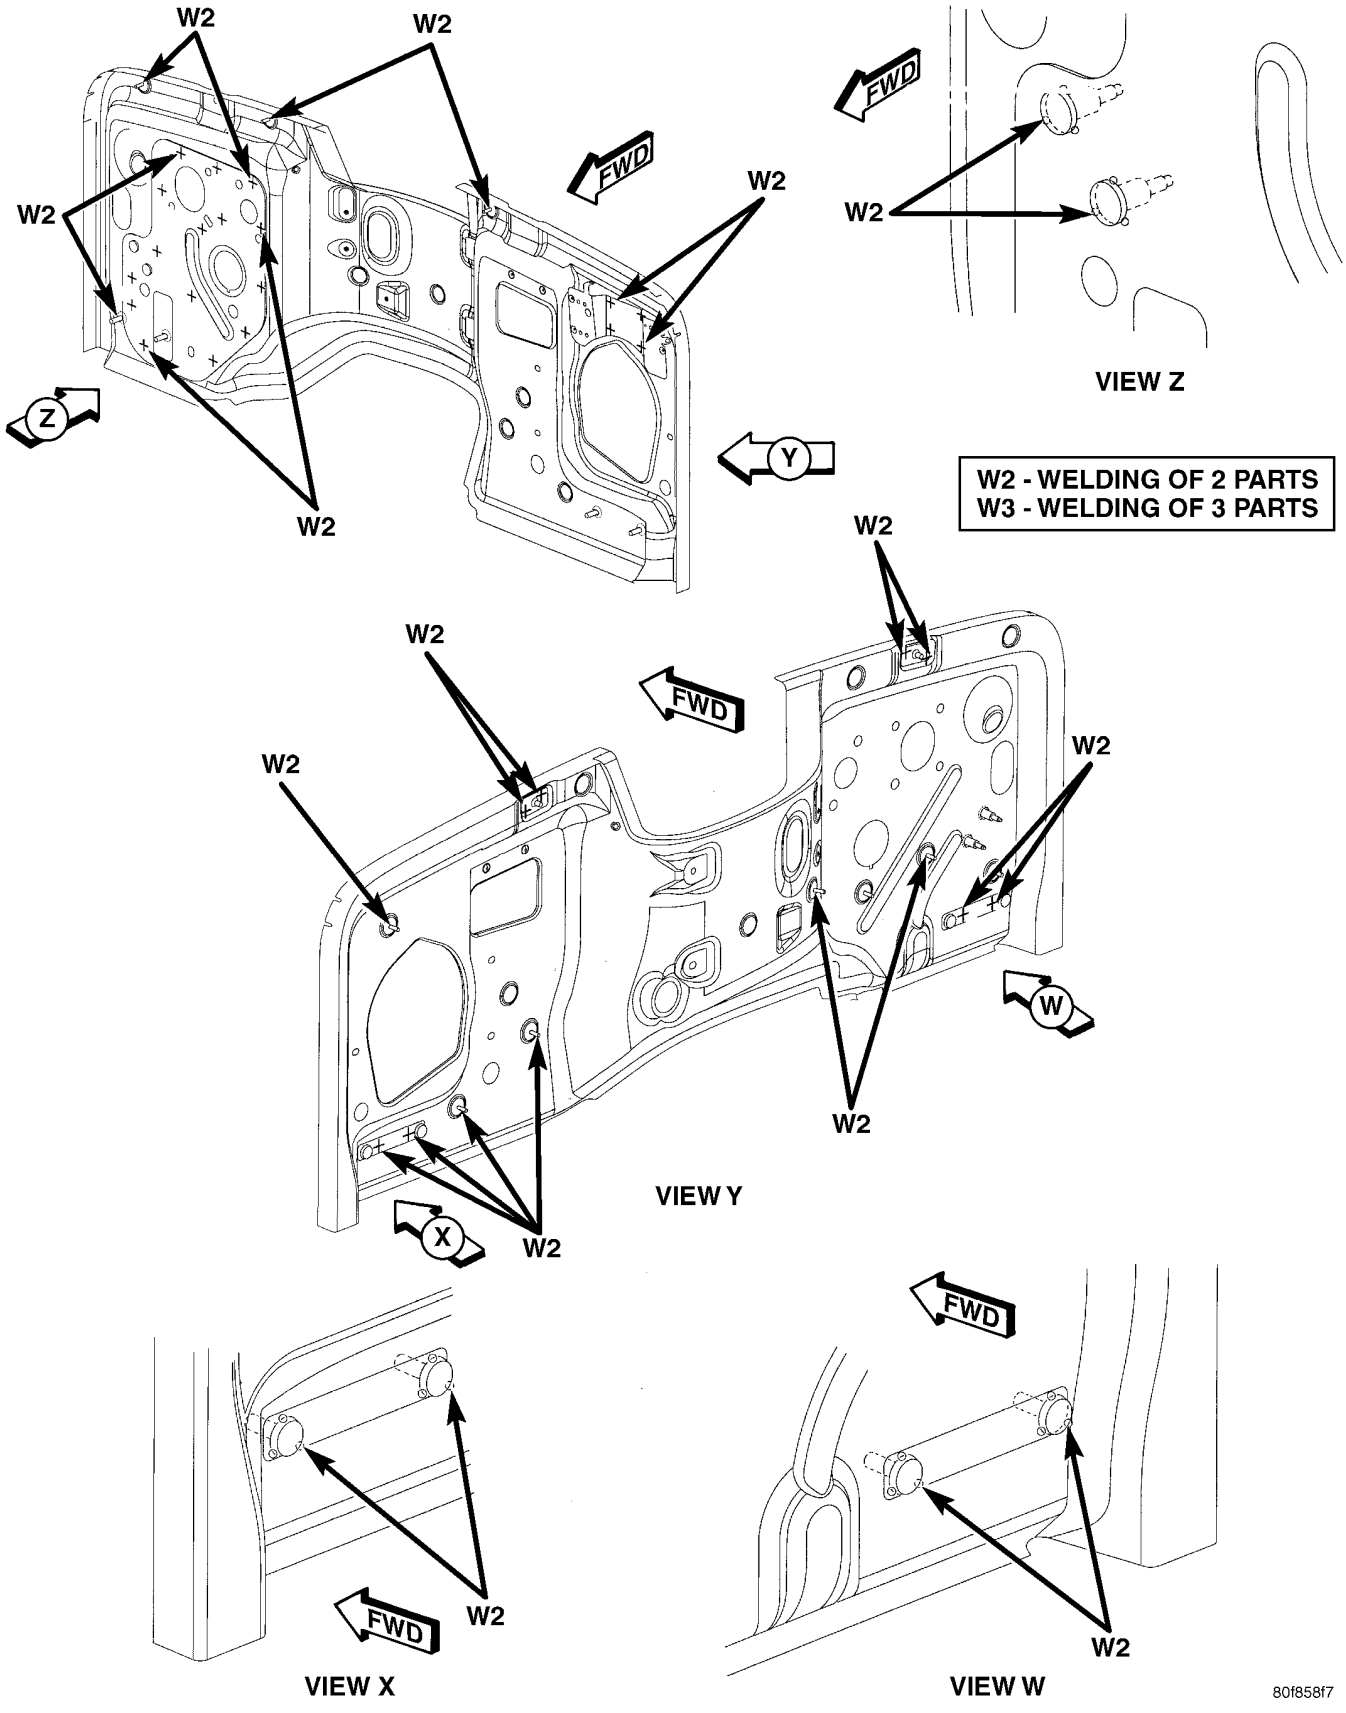

Fig. 51 DASH PANEL - RIGHT HAND DRIVE