WELD LOCATIONS (Continued)

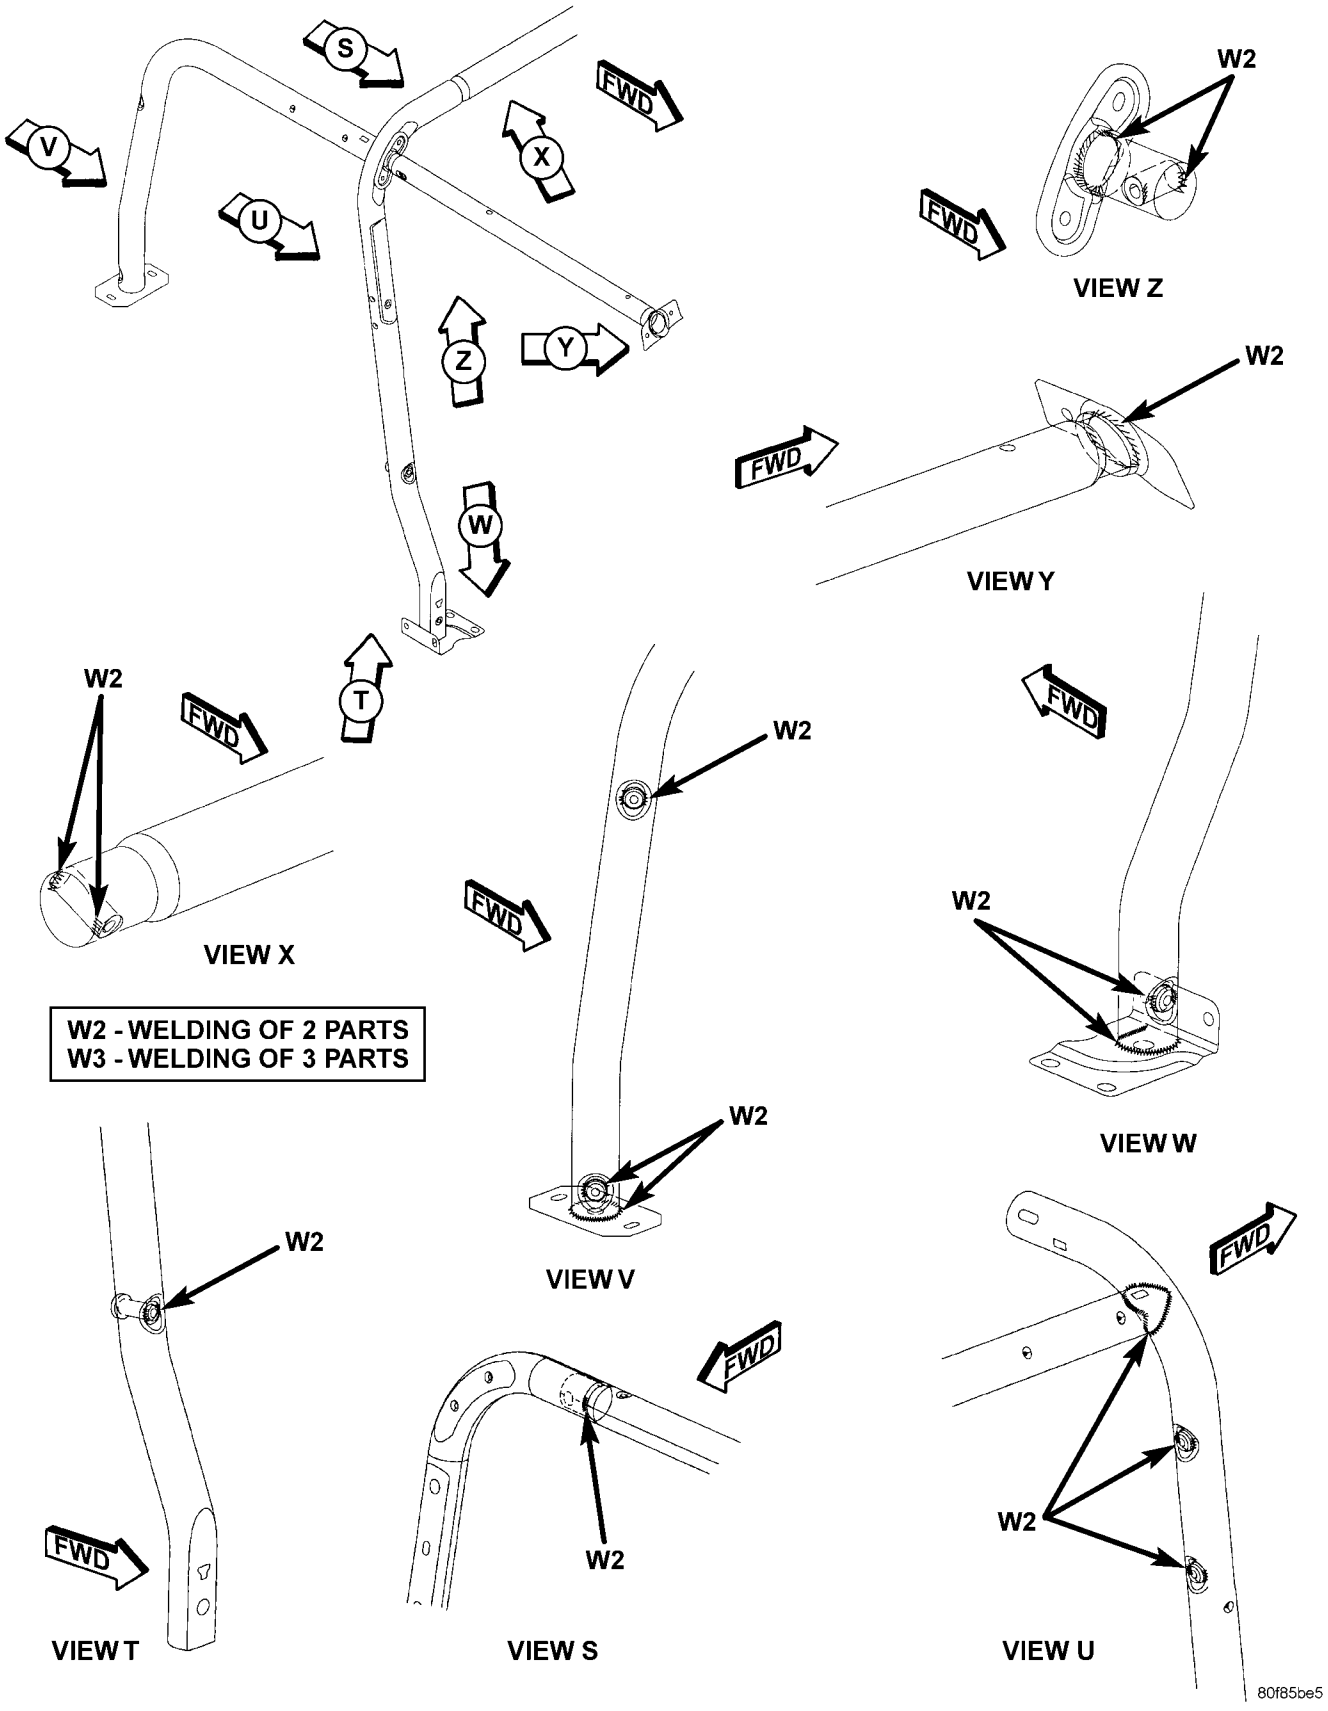

Fig. 58 SPORT BAR ASSEMBLY