WELD LOCATIONS (Continued)

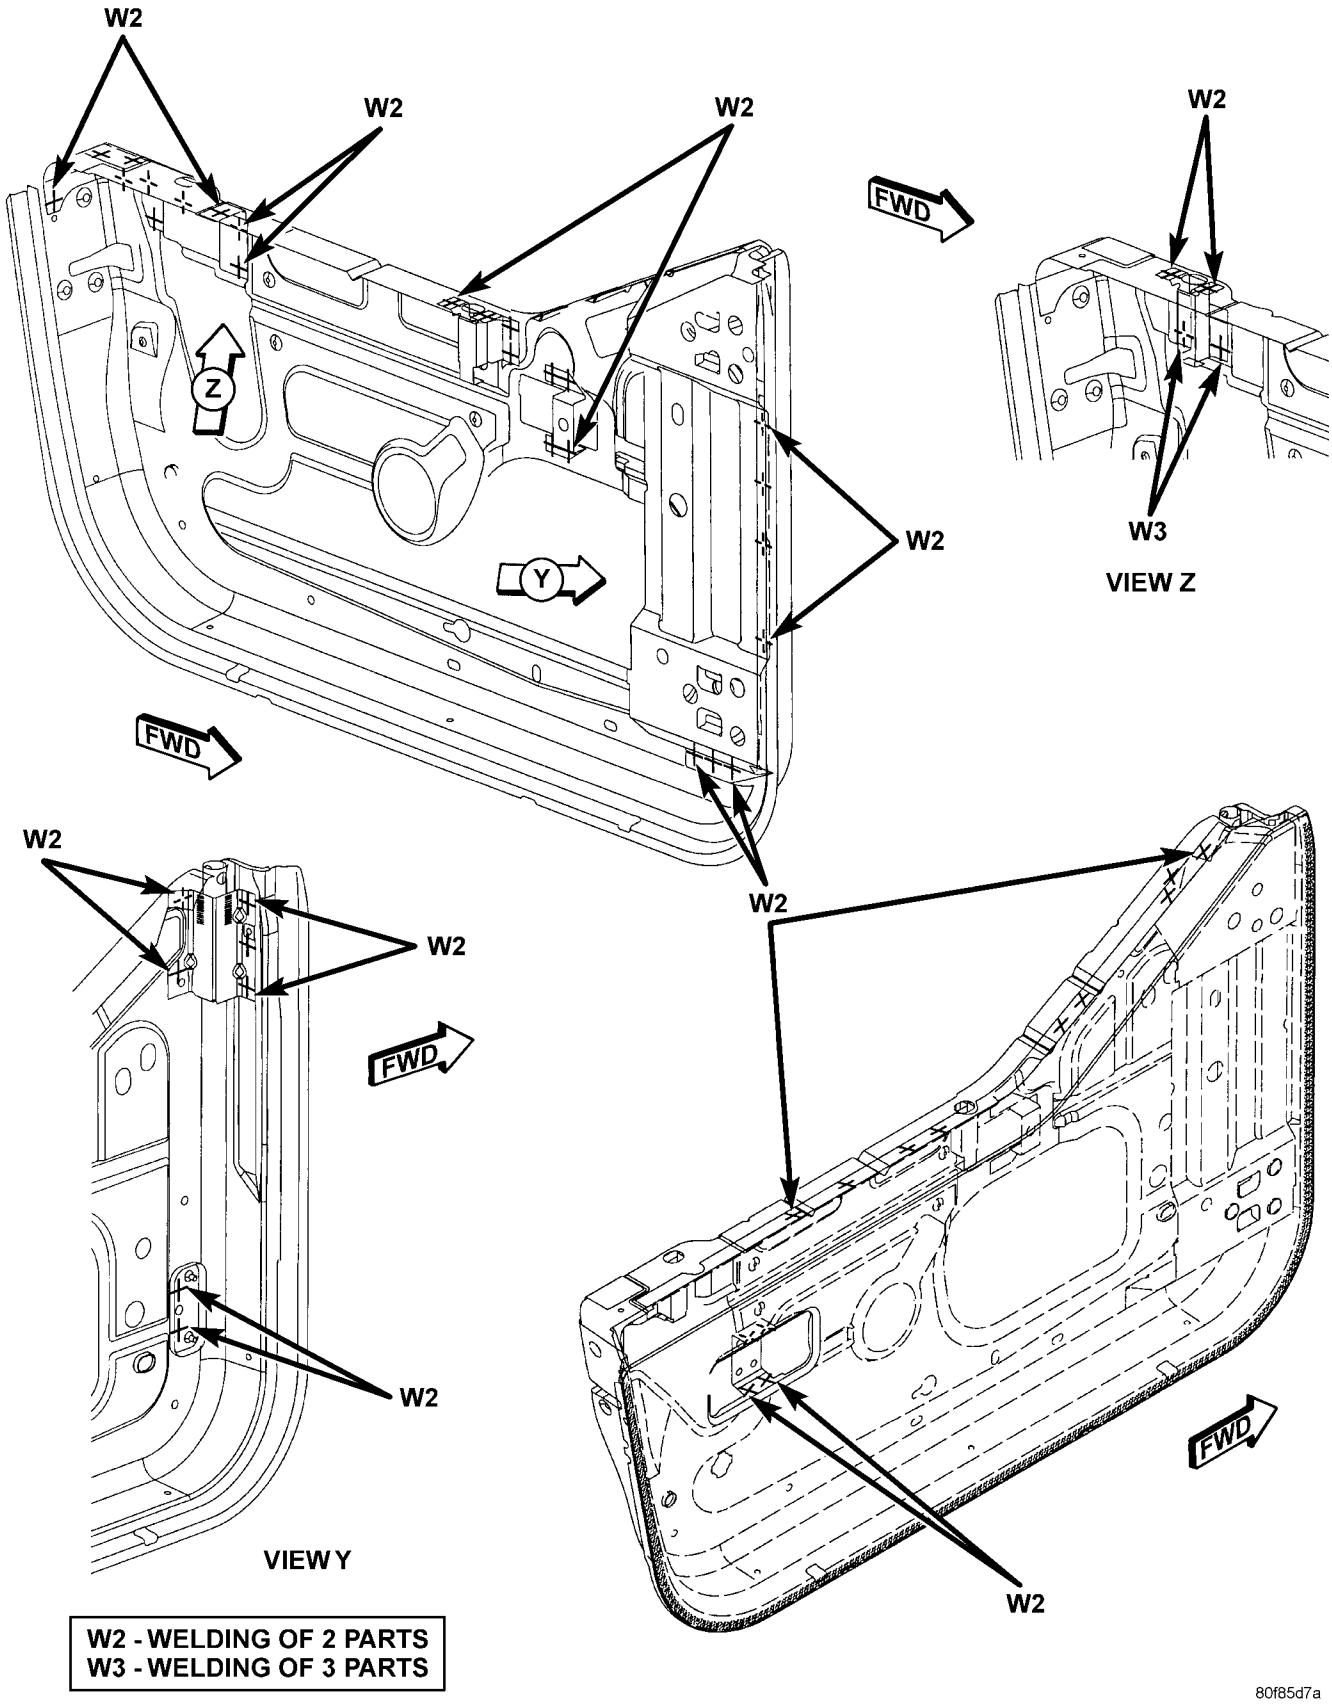


Fig. 59 HALF DOOR ASSEMBLY