WELD LOCATIONS (Continued)

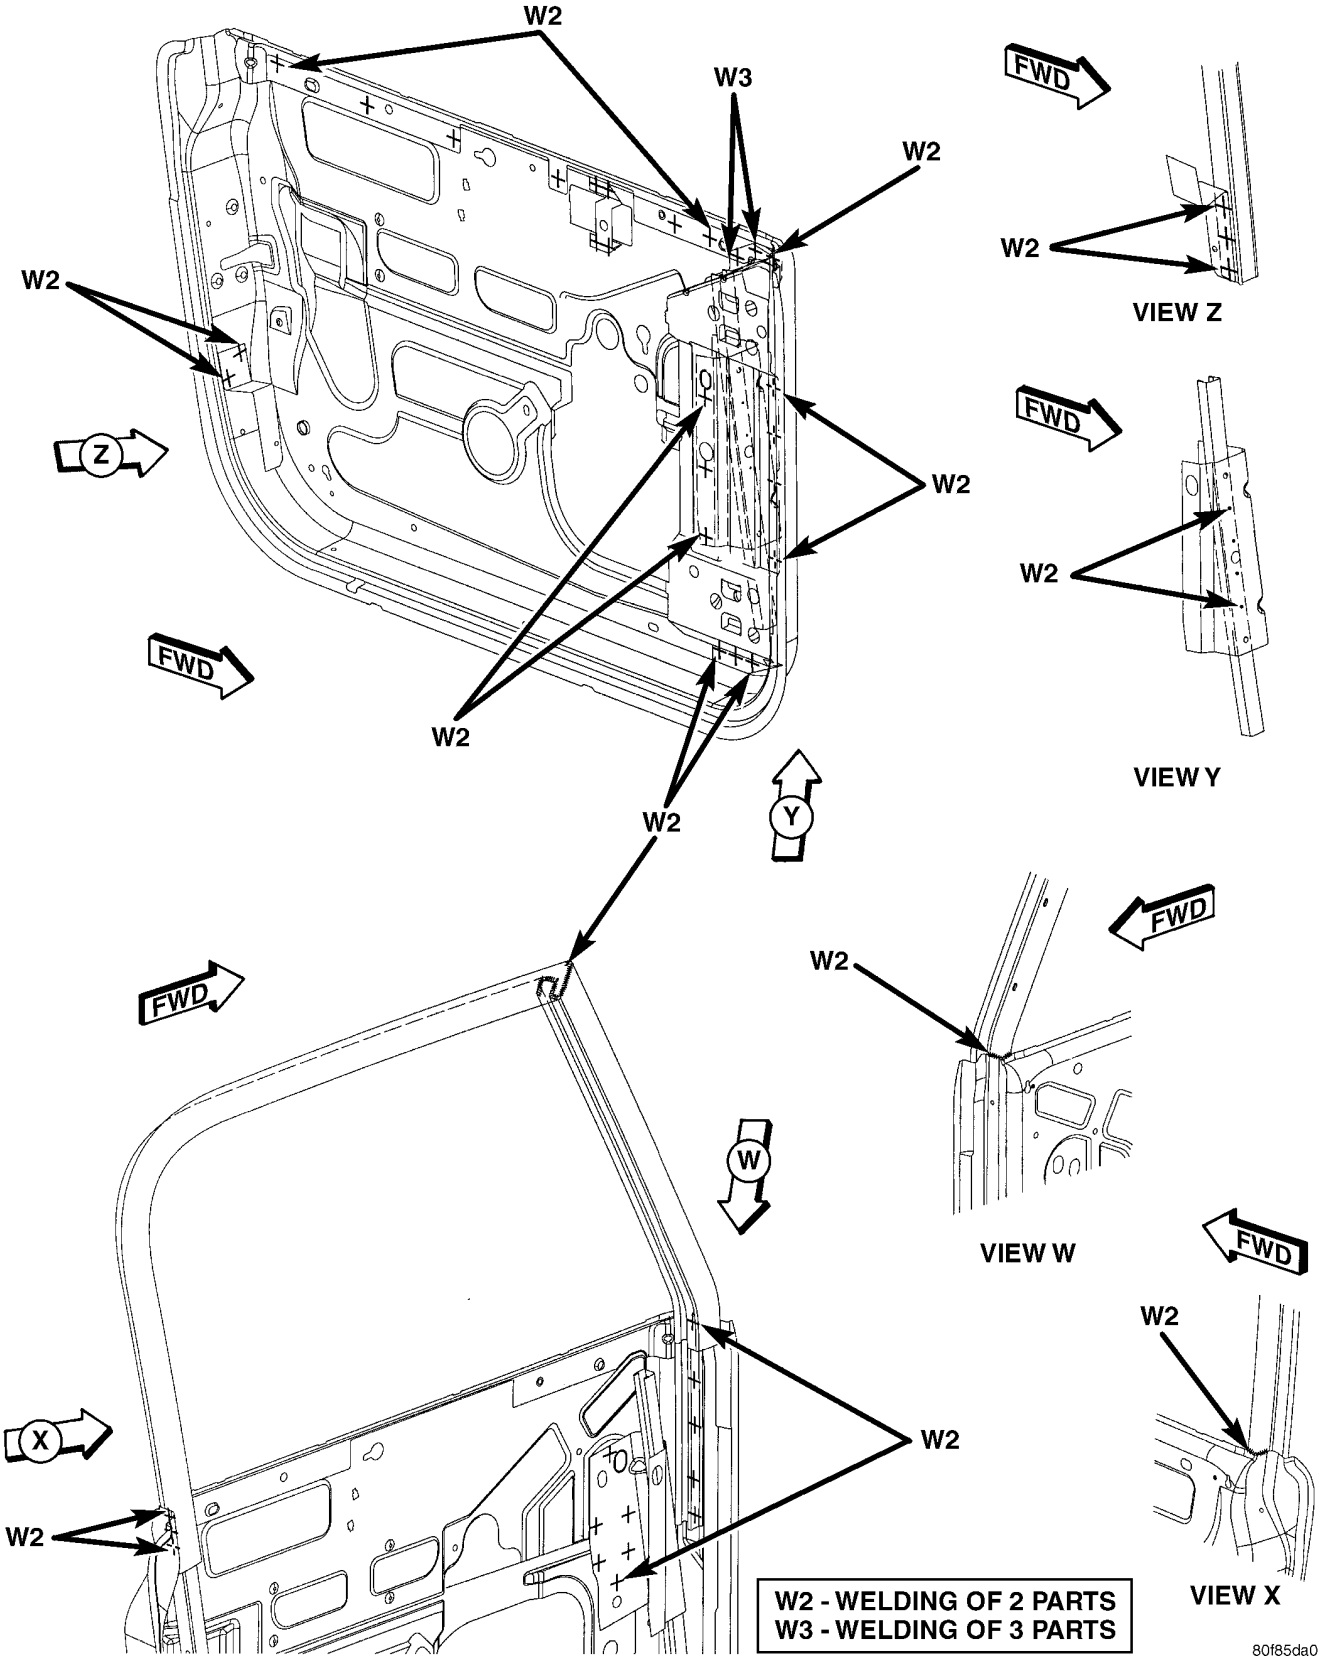

Fig. 60 FULL DOOR ASSEMBLY (1 OF 2)