WELD LOCATIONS (Continued)

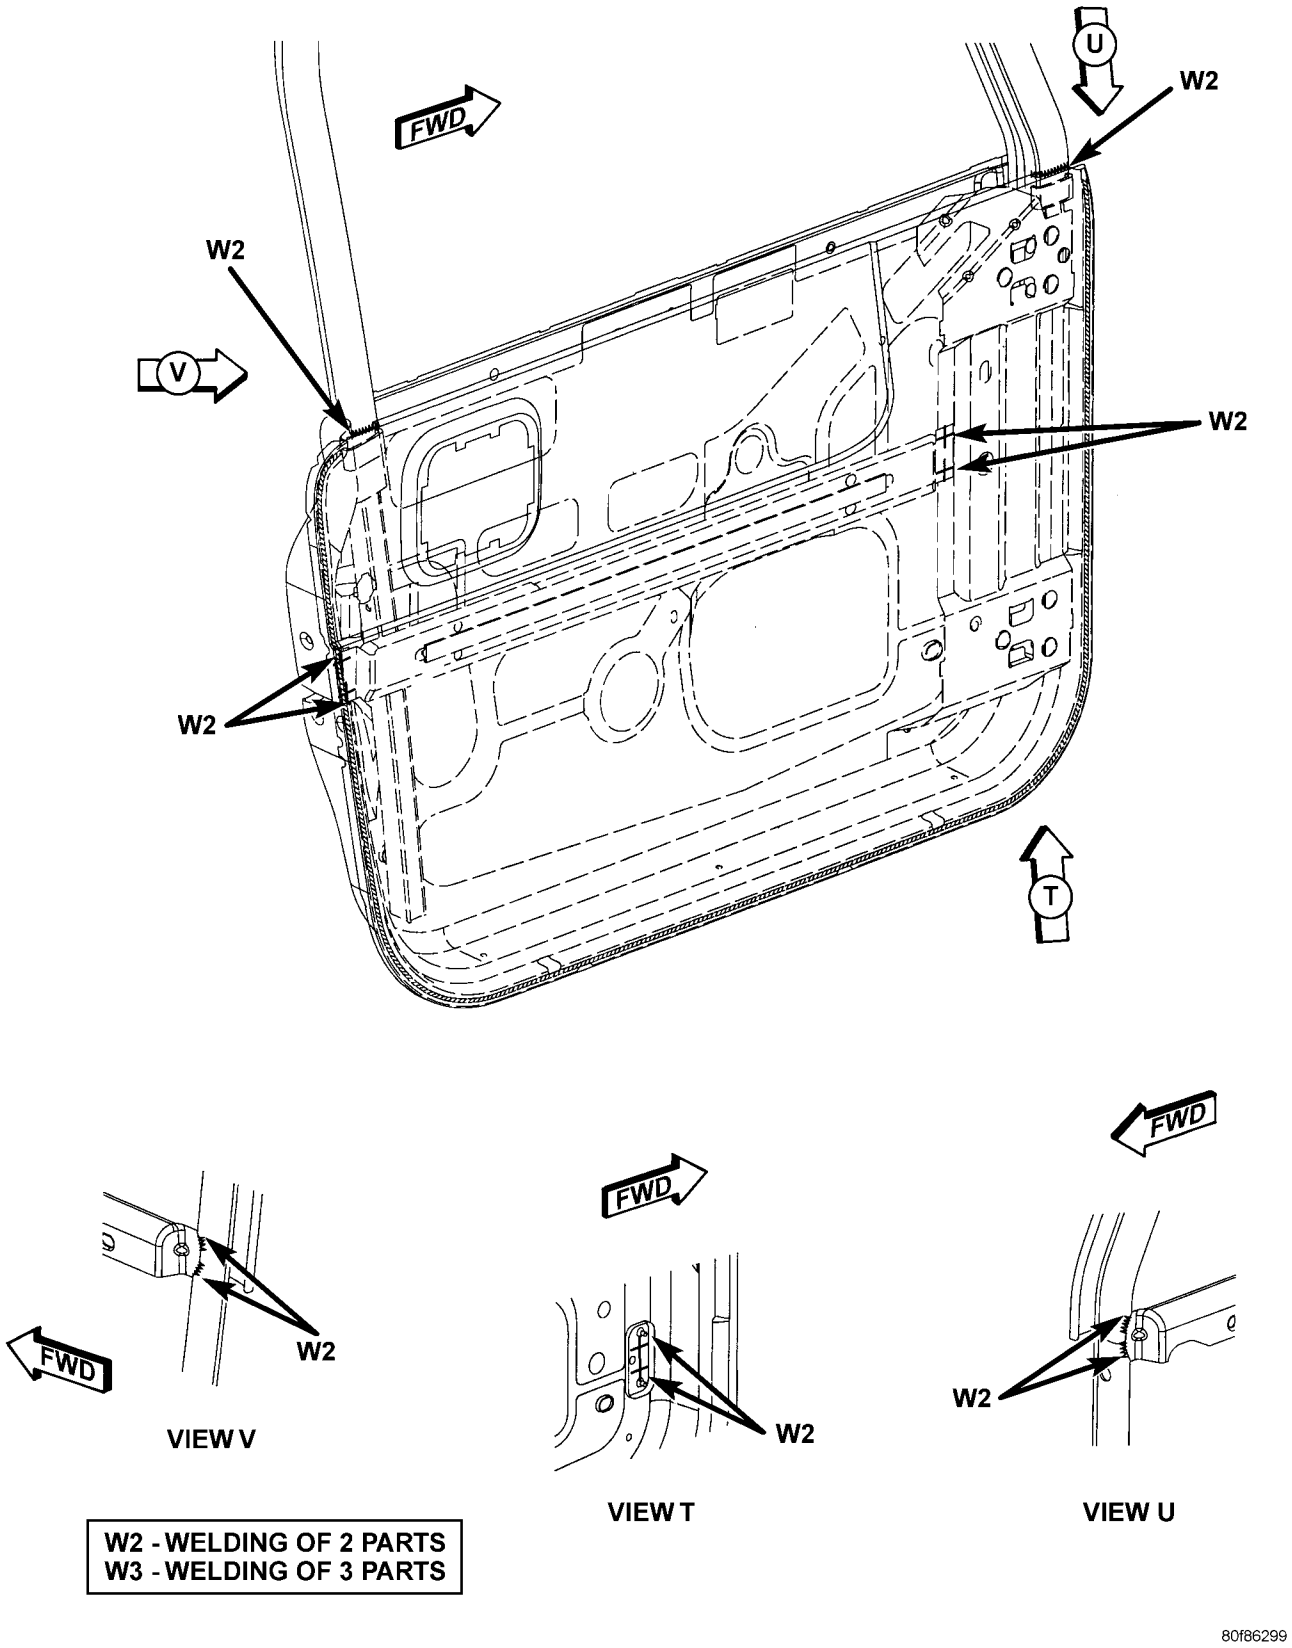

Fig. 61 FULL DOOR ASSEMBLY (2 OF 2)