WELD LOCATIONS (Continued)

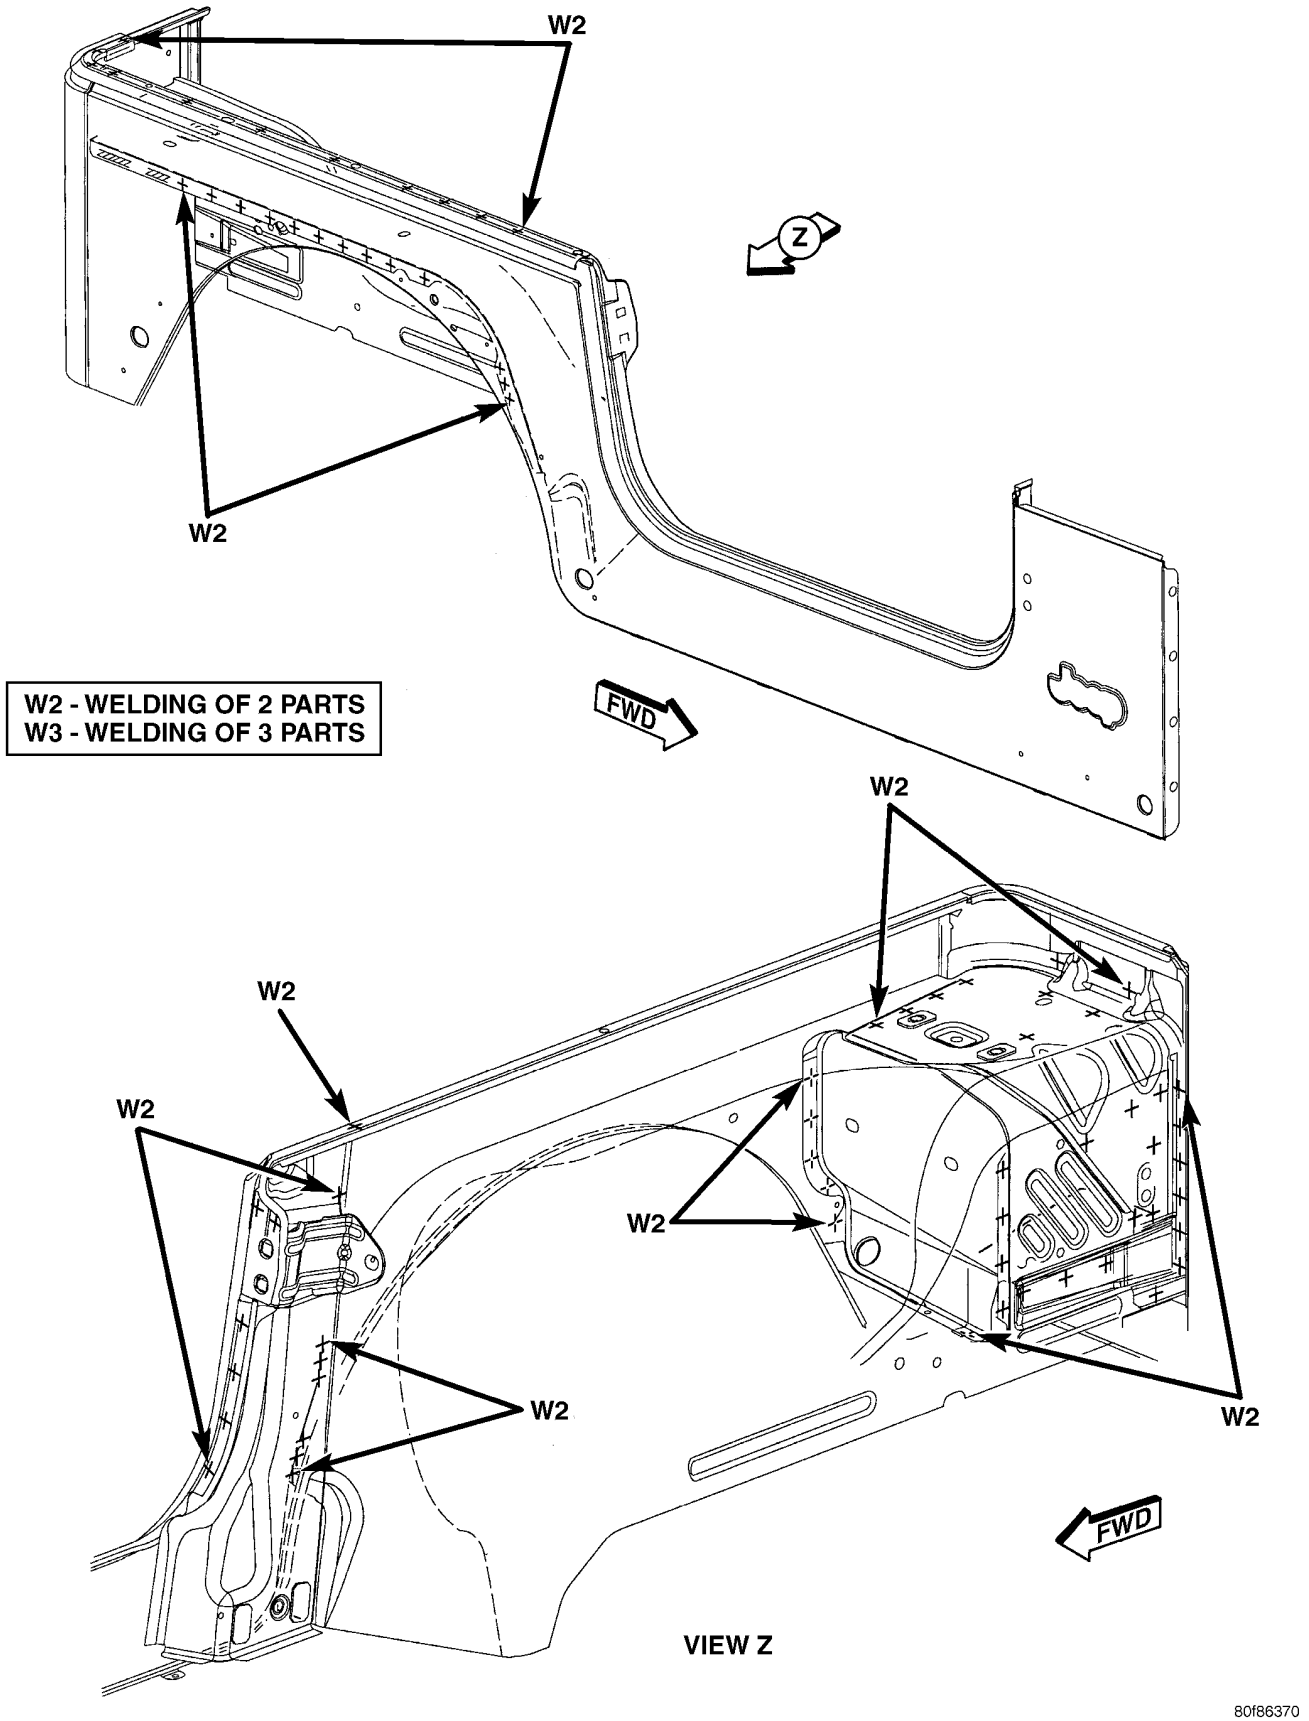


*Fig. 69 BODY SIDE (1 OF 2)*