WELD LOCATIONS (Continued)

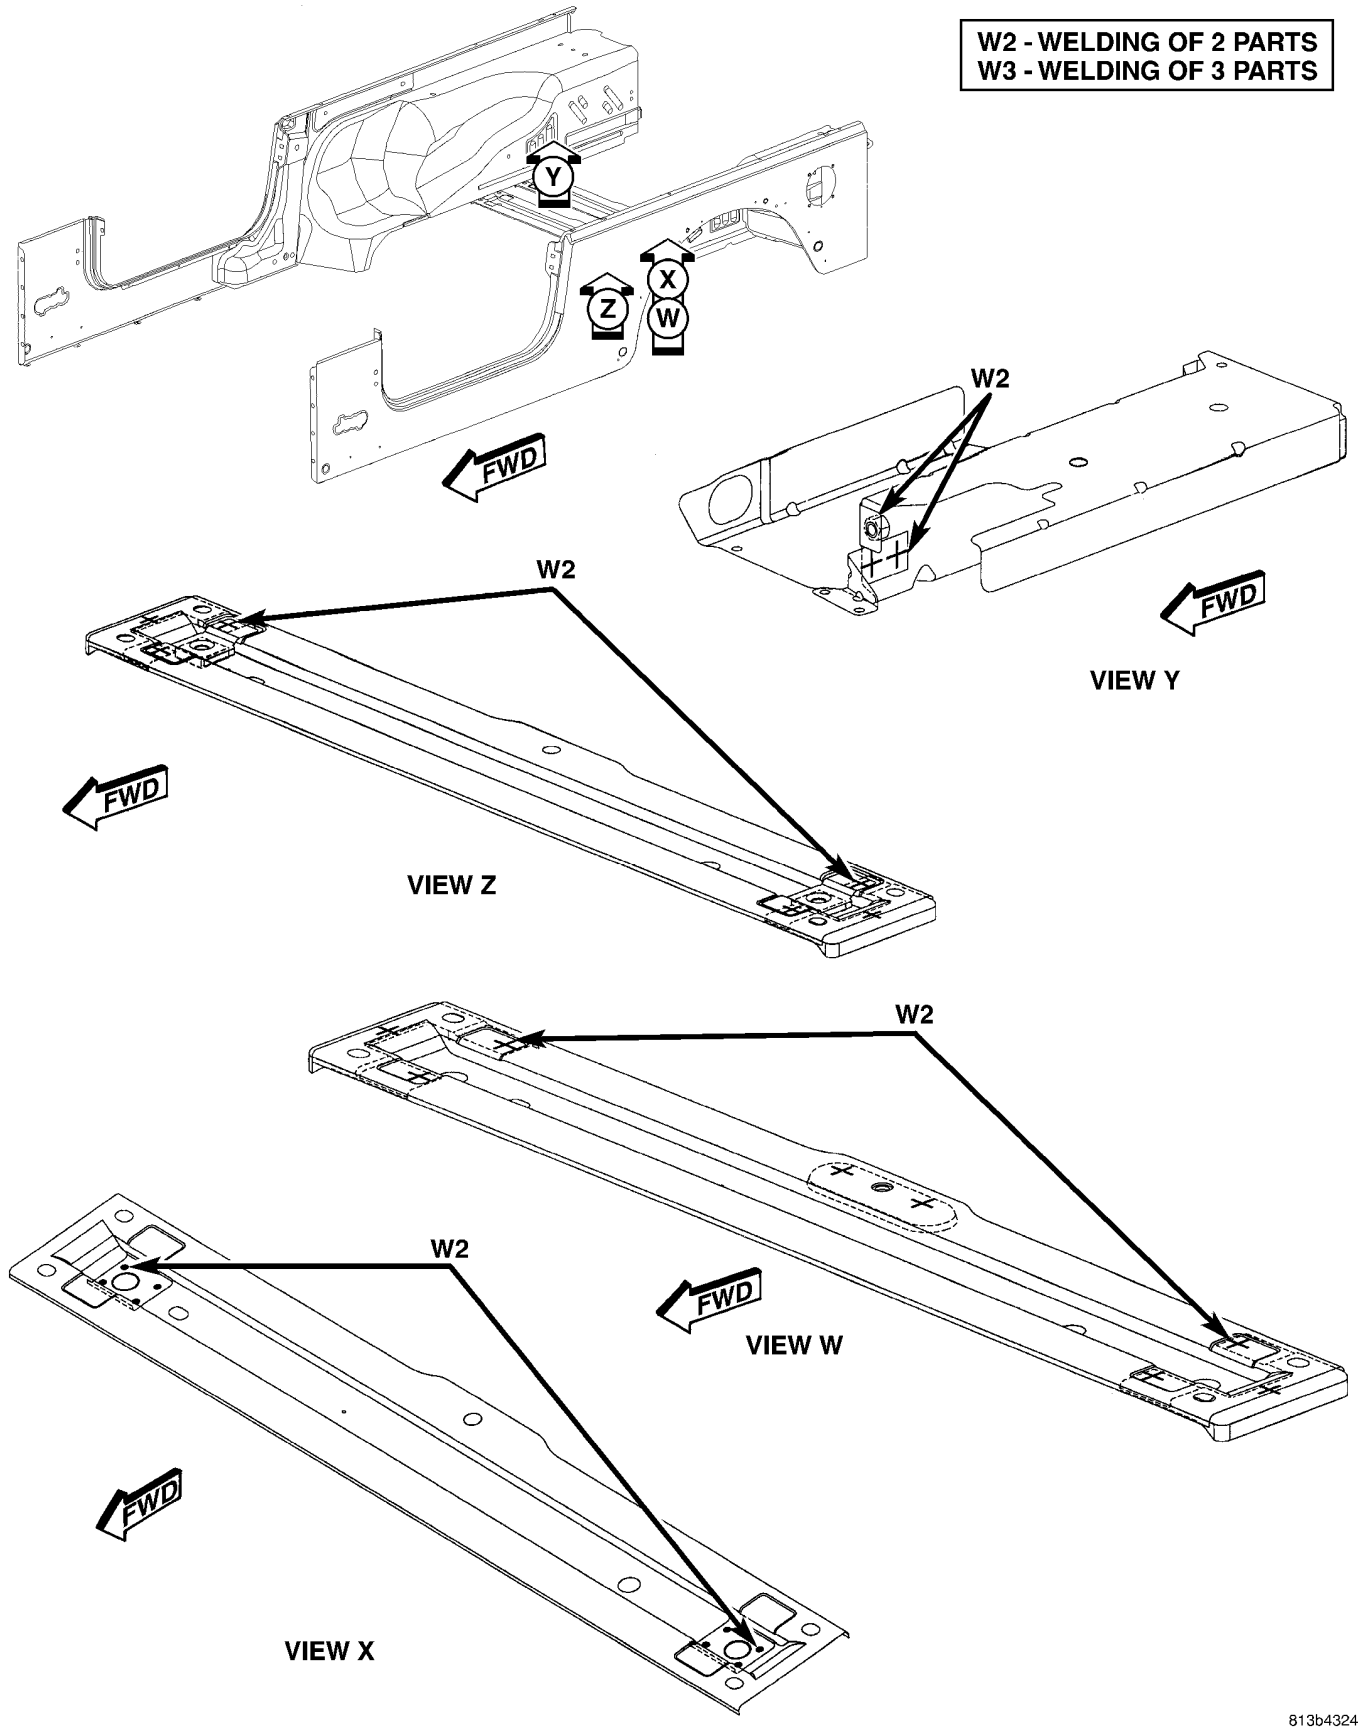

Fig. 75 BODY COMPLETE LONG WHEEL BASE (LWB) (1 OF 3)