WELD LOCATIONS (Continued)

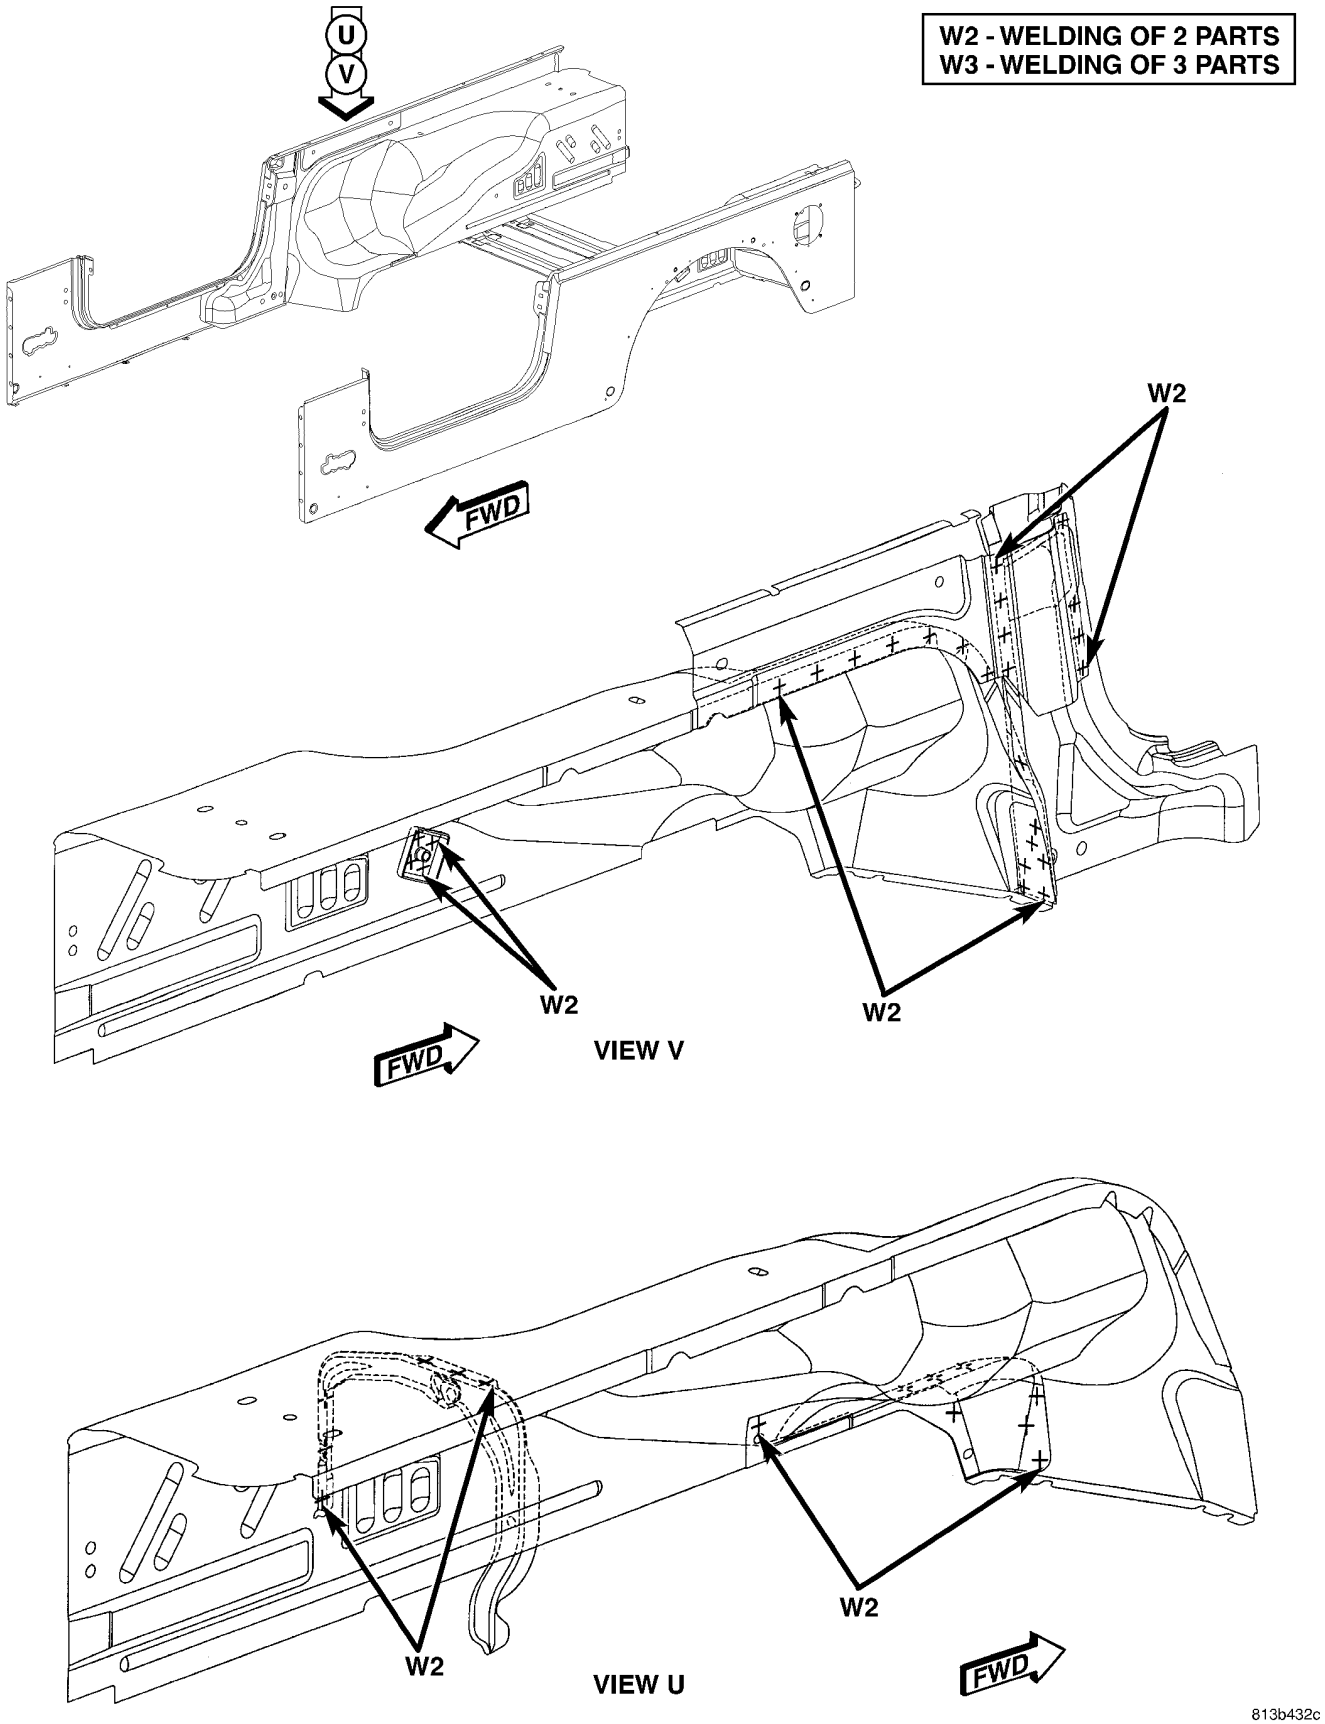


*Fig. 76 BODY COMPLETE LWB (2 OF 3)*