WELD LOCATIONS (Continued)

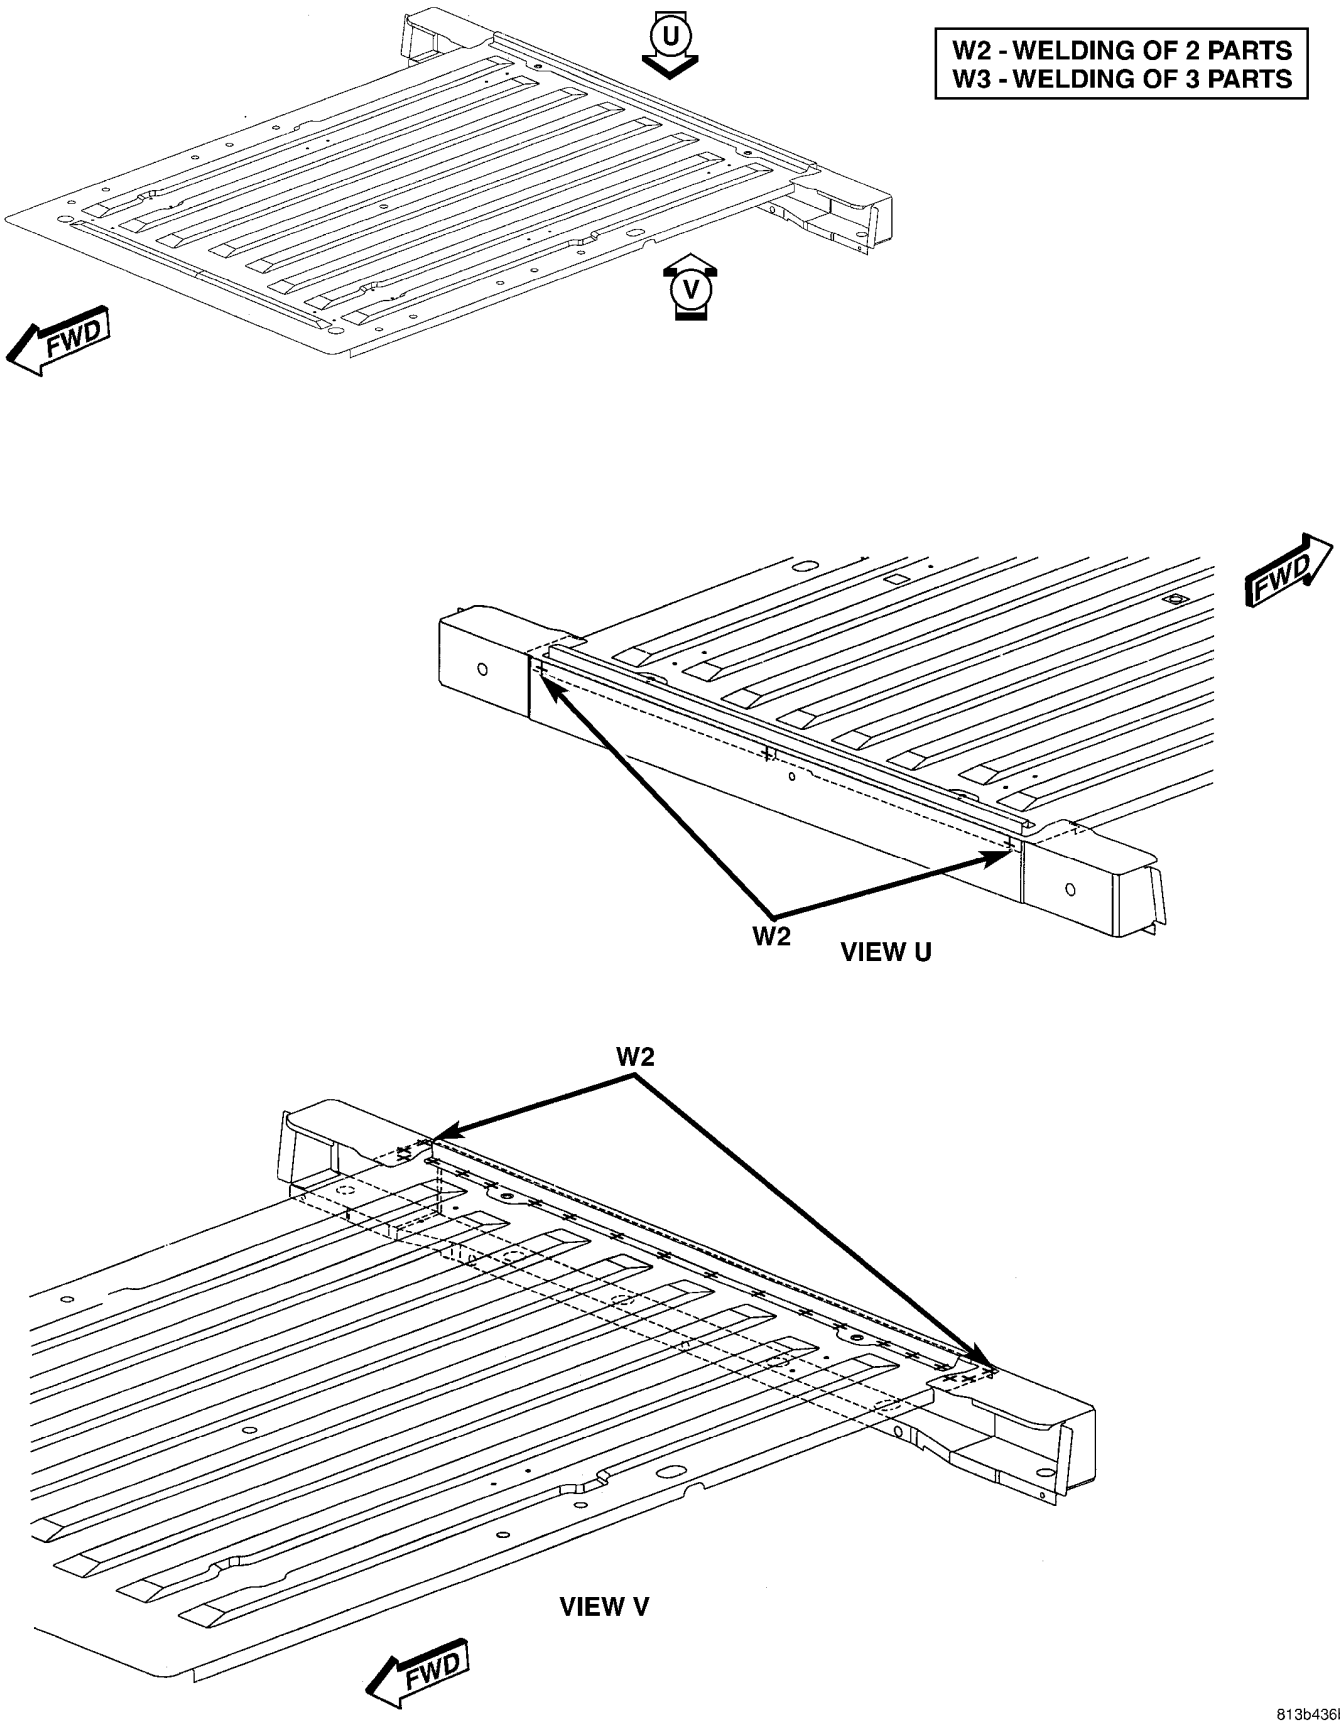


Fig. 80 REAR FLOOR LWB (3 OF 3)