WELD LOCATIONS (Continued)

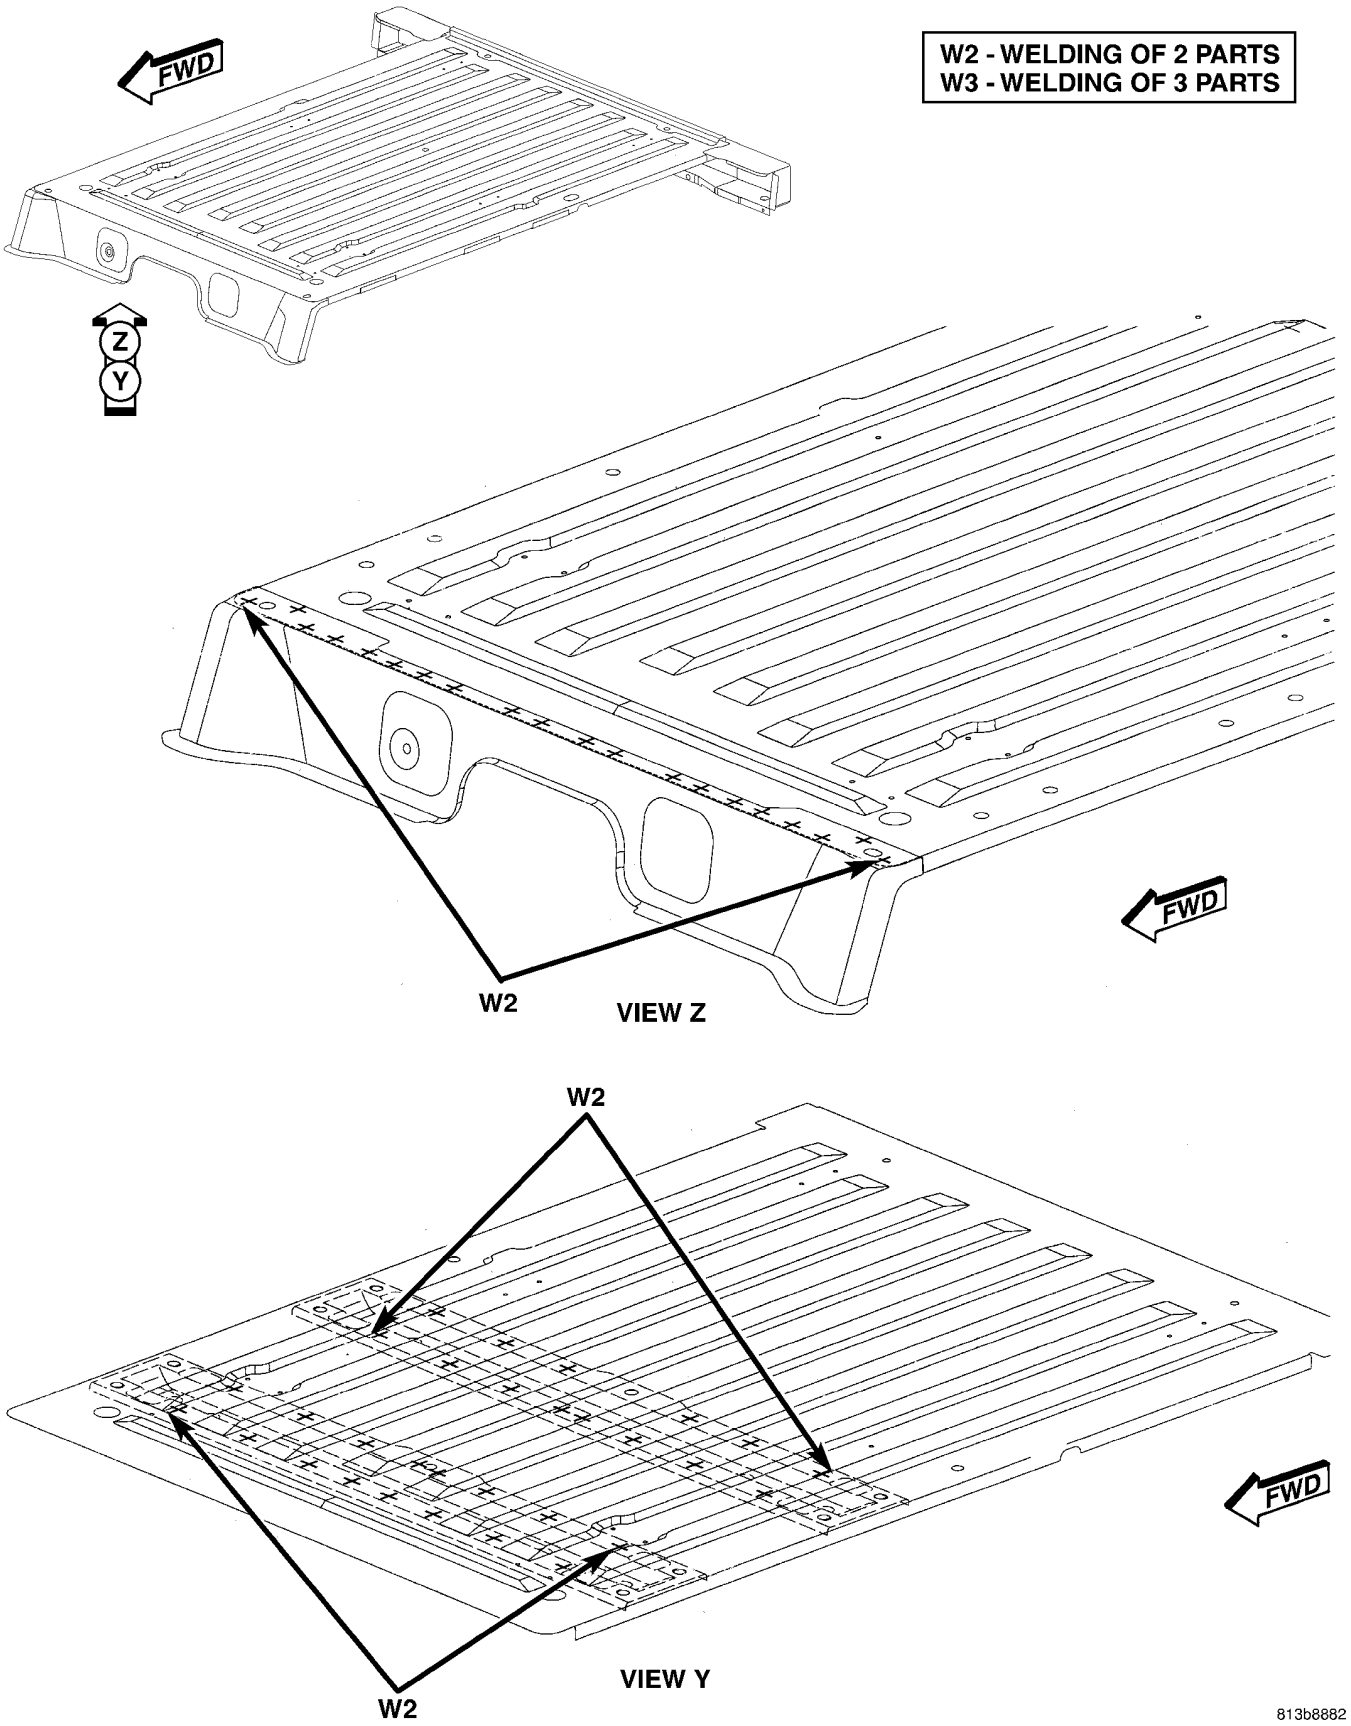



*Fig. 81 UNDERBODY COMPLETE LWB (1 OF 3)*