WELD LOCATIONS (Continued)

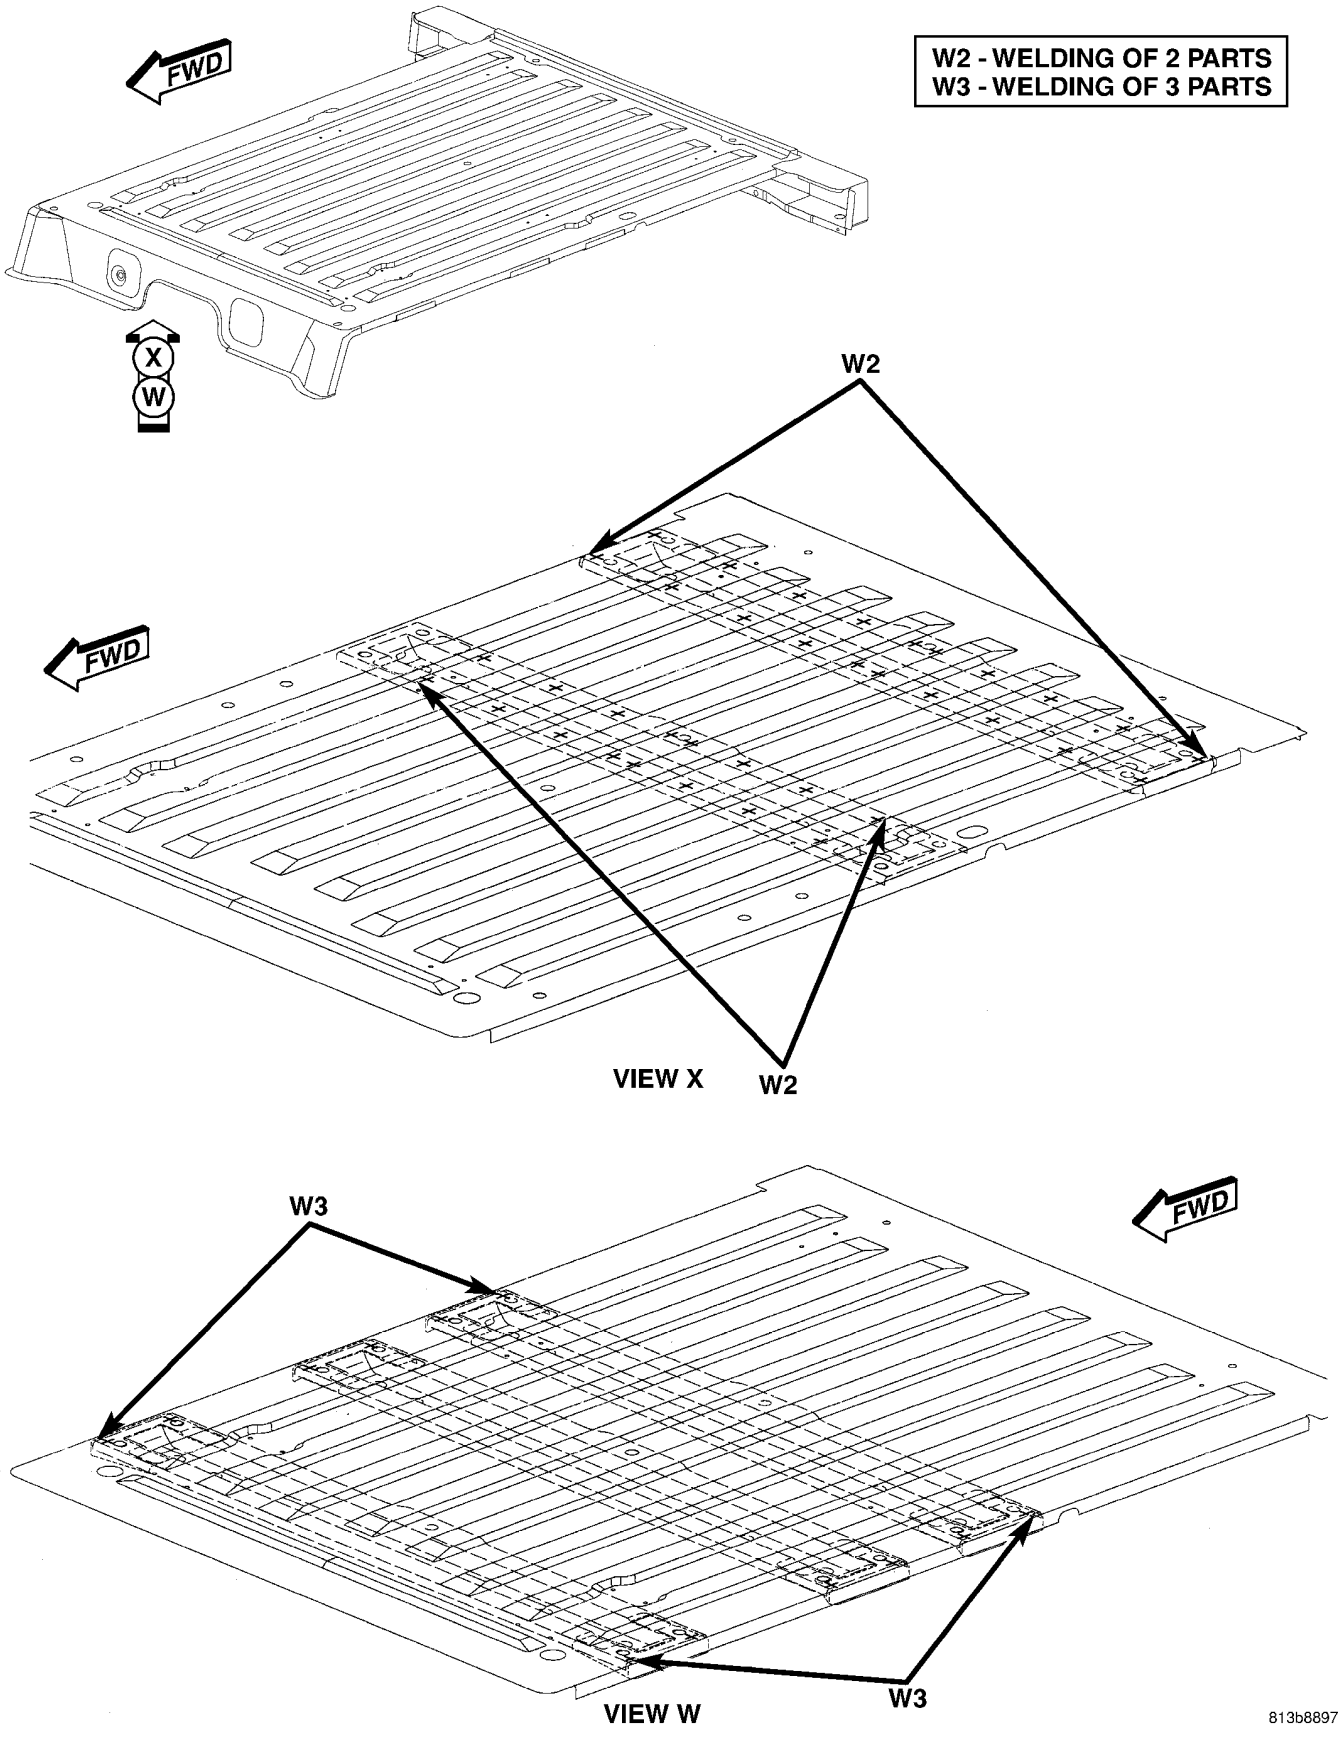


Fig. 82 UNDERBODY COMPLETE LWB (2 OF 3)