WELD LOCATIONS (Continued)

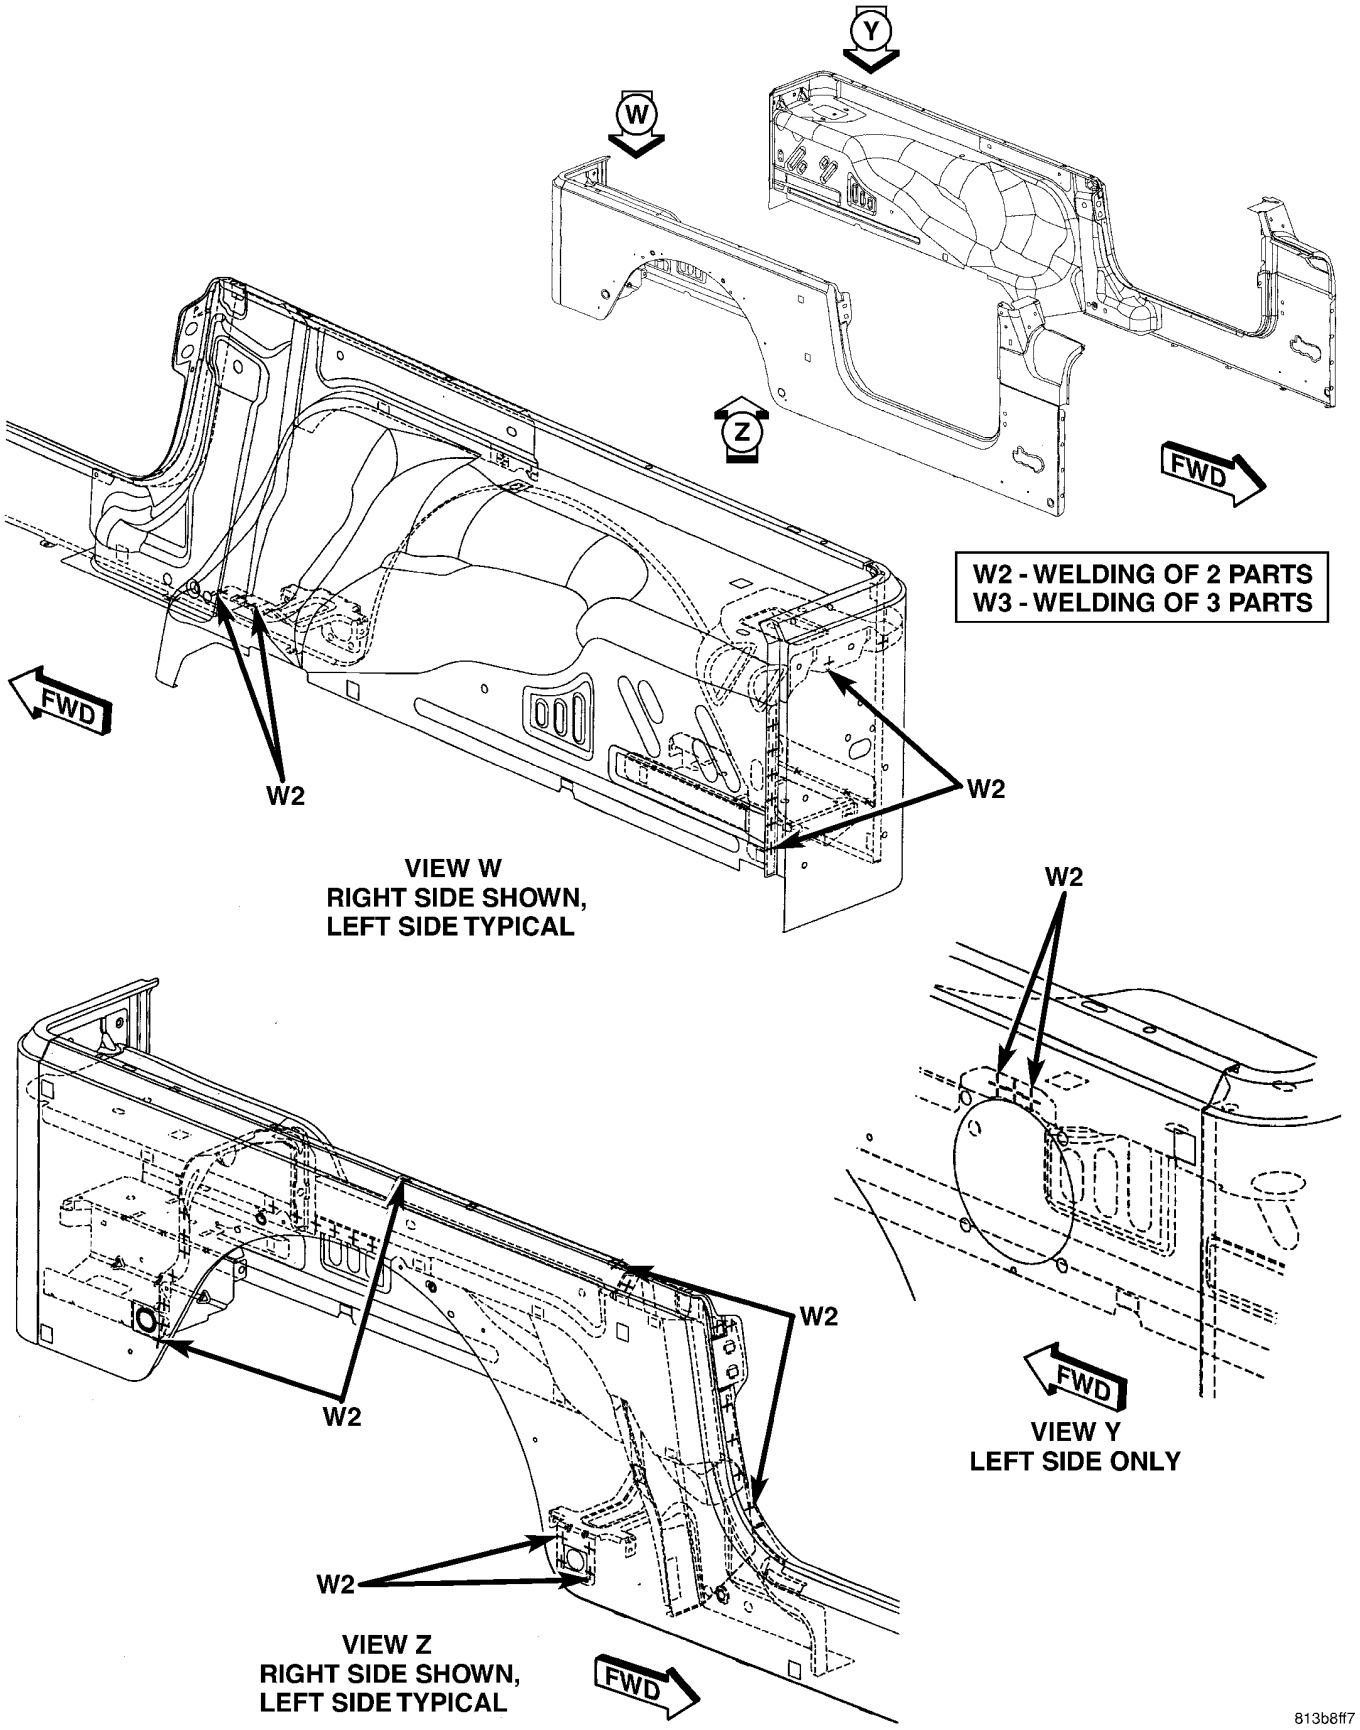


Fig. 84 BODY SIDE COMPLETE LWB (1 OF 2)