WELD LOCATIONS (Continued)

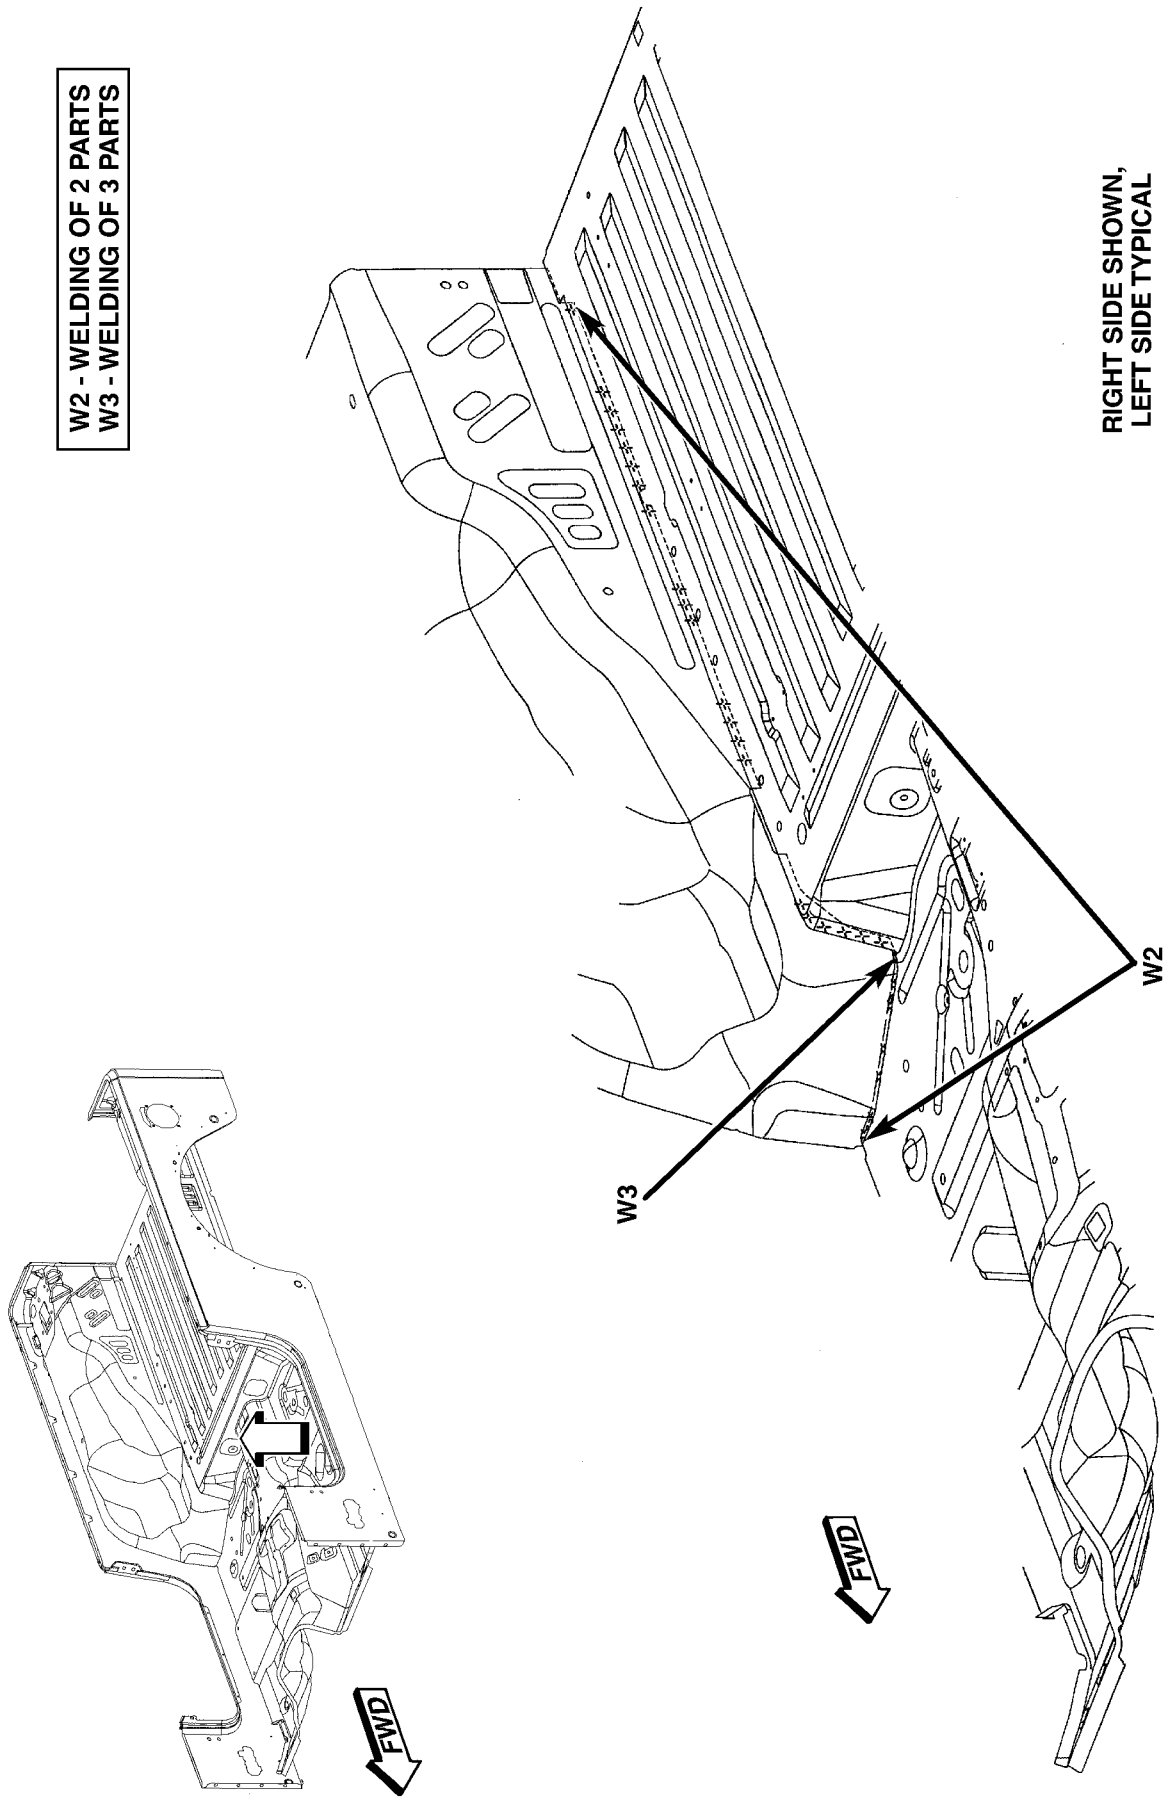

Fig. 86 BODY COMPLETE LWB (1 OF 4)