AUTOMATIC TRANSMISSION - 42RLE (Continued)

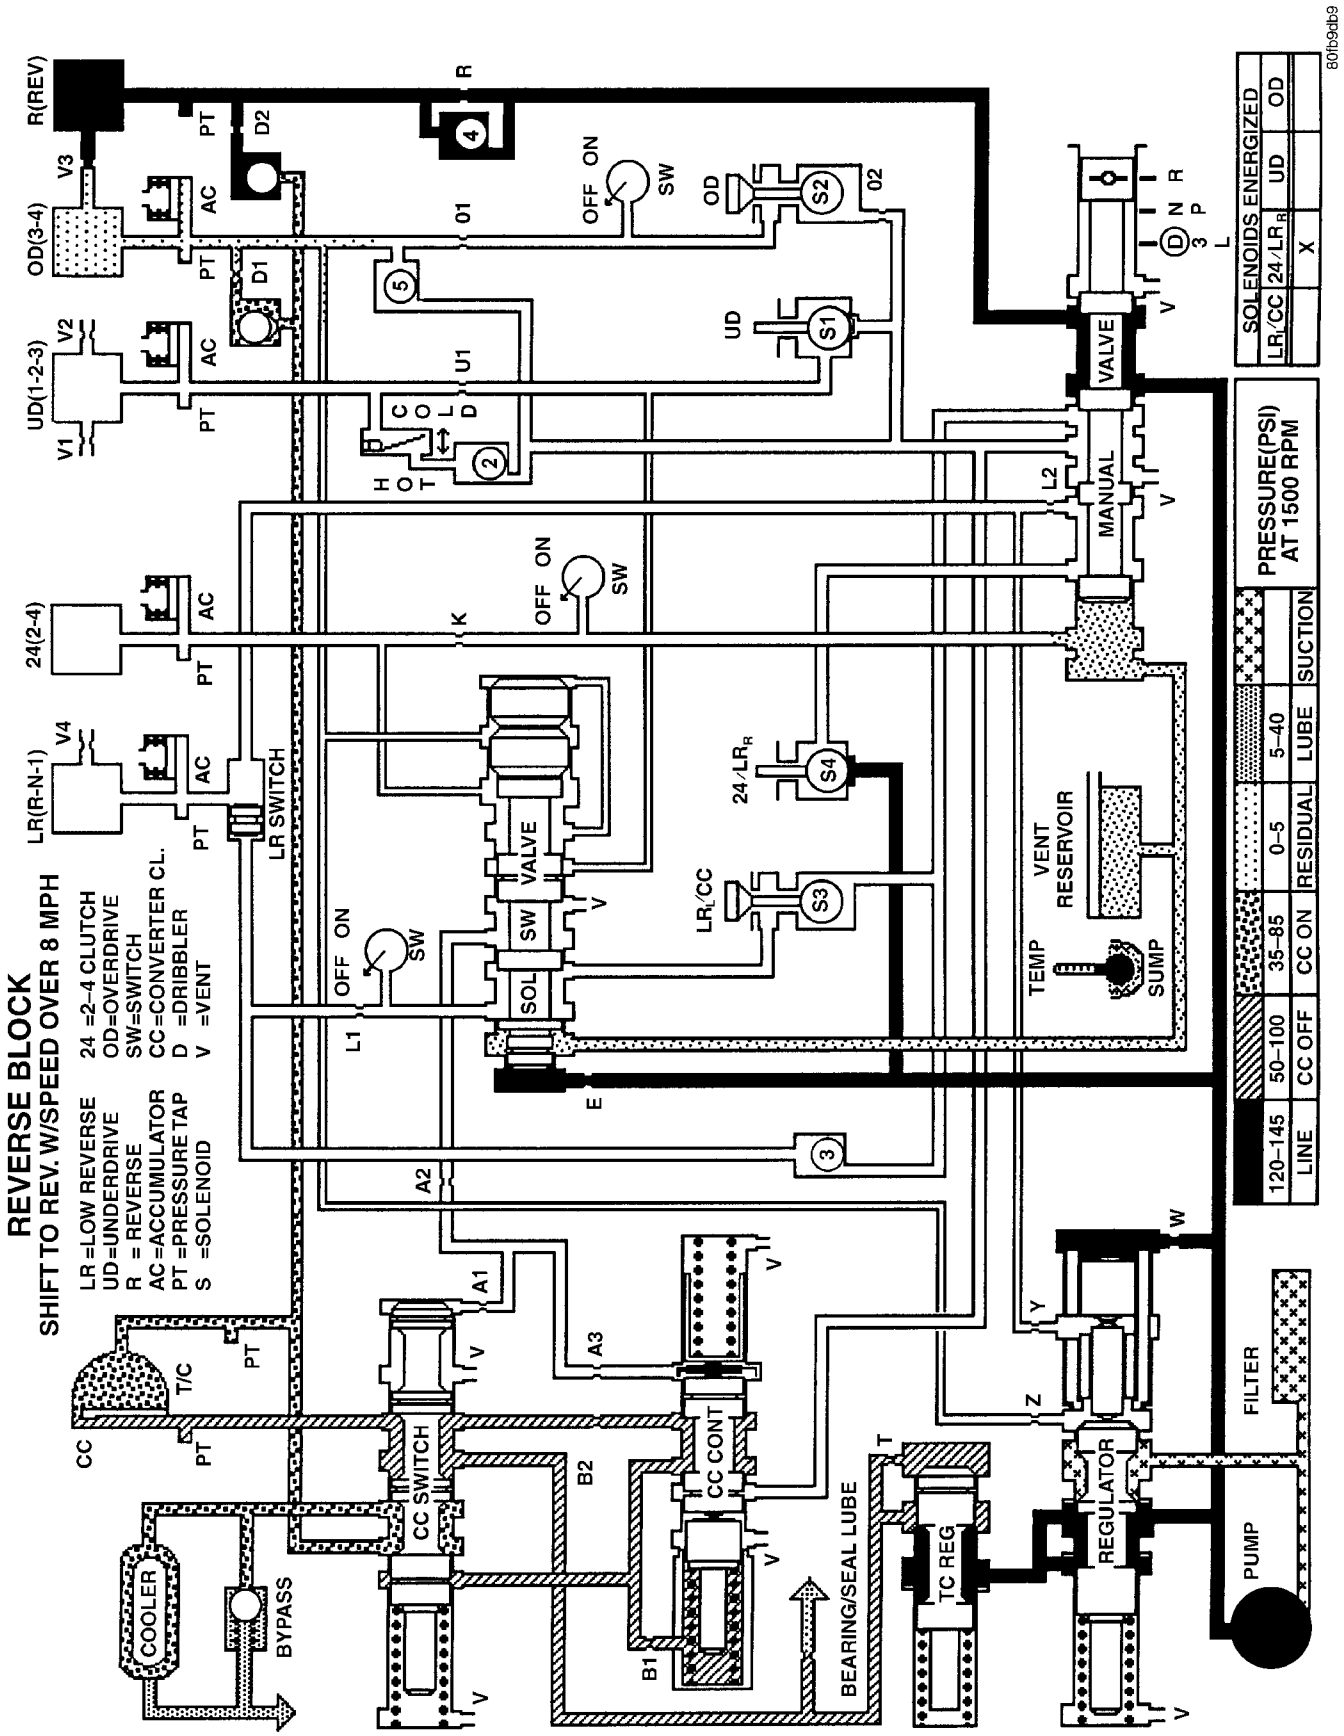

Reverse Block (Shift to Reverse w/Speed Over 8 mph)