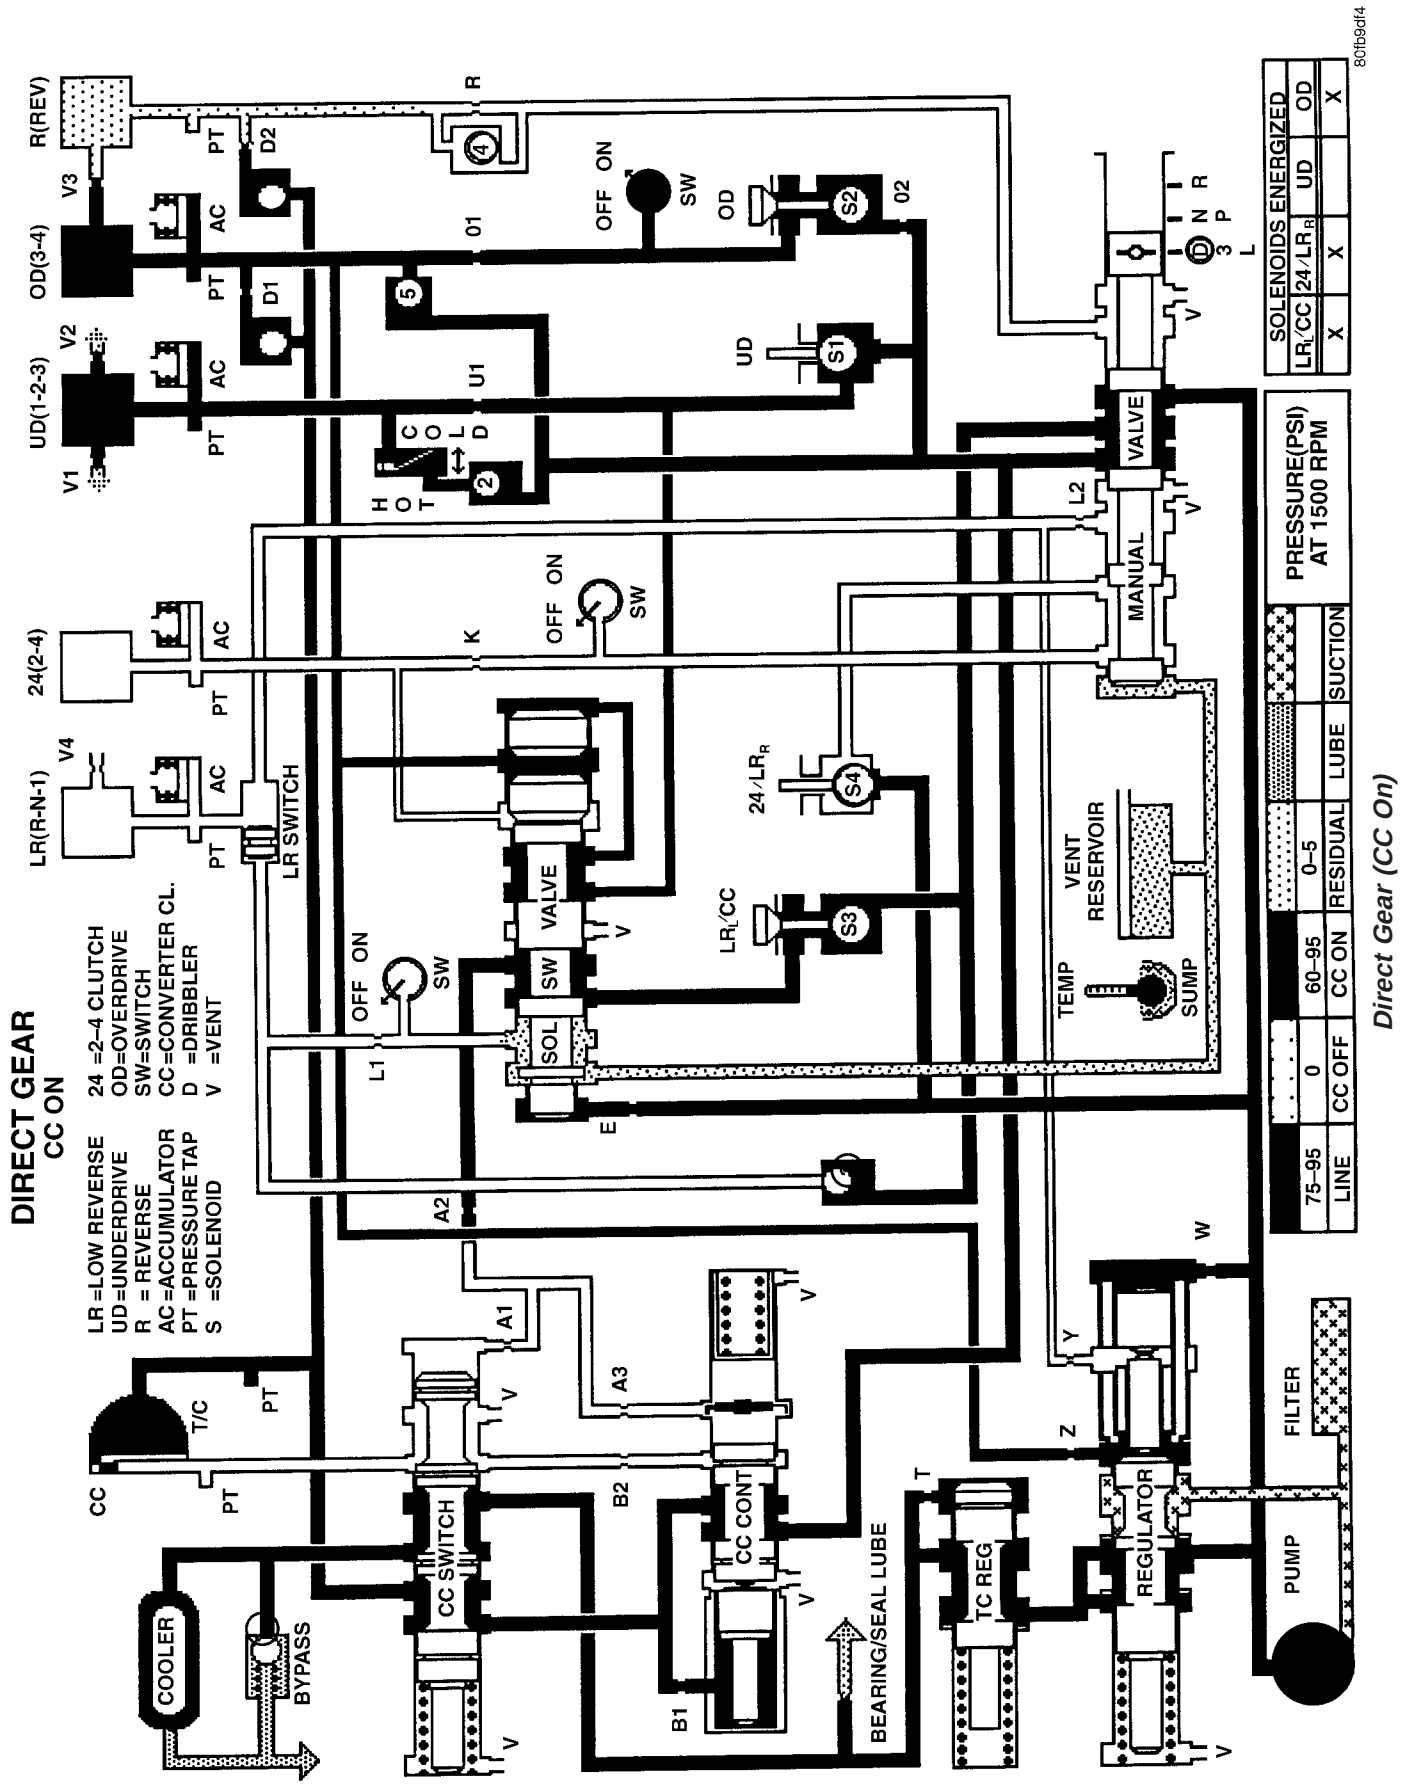AUTOMATIC TRANSMISSION - 42RLE (Continued)